


LEGENDA:	
	QUADRO ELÉTRICO DO EDIFÍCIO
	TOMADA ELÉTRICA 2P+T, 16A, ENCASTRAR
	TOMADA ELÉTRICA 2P+T, 16A, ENCASTRAR, C/TAMPA IP44
	TOMADA ELÉTRICA 2P+T, 16A, ESTANQUE IP65, ENCASTRAR
	TOMADA ELÉTRICA 2P+T, 16A, ESTANQUE IP65, SALIENTE
	TOMADA DE CHÃO ELETRICIDADE (2 módulos) 1x 2P+T 16A
	ALIMENTAÇÃO ELÉTRICA ESPECÍFICA
	DOWNLIGHT LED COMPACTO DE ENCASTRAR, 2,5W 3000K IP43 Ø27mm
	LUMINÁRIA LED TUBULAR SUSPensa, 4000K, 931mm ou 1493mm
	LUMINÁRIA TIPO RÉGUA SALIENTE, 1030,1530mm ou 2530mm, 3000K
	LUMINÁRIA LINEAR DE ENCASTRAR, 1530mm, 3000K
	CANDEIEIRO SUSPENSO, A DEFINIR
	APLIQUE DE PAREDE SALIENTE RETANGULAR, LUZ DESCENDENTE E ASCENDENTE
	Placa Superfície LED Quadrada 18W 225x225 mm; Ref. efectaLED 407
	LUMINÁRIA LED DE ENCASTRAR BALIZADOR, Ø33mm, 2,5W, 3000K, IP65 IK10
	CANDEIEIRO LED SUSPENSO, Ø1135mm, 2,5W, 3000K, IP65 IK10
	LUMINÁRIA LED CUBO SALIENTE IP65 3000K EXTERIOR
	Plafon LED 20W PHILIPS CL200; Ref. efectaLED 85955
	LUMINÁRIA LED DE ENCASTRAR, 5W, 3000K, IP65 IK10
	PONTO DE ILUMINAÇÃO EXTERIOR A DEFINIR, JARDIM, IP65<
	PONTO DE ILUMINAÇÃO TETO OU PAREDE - LUMINÁRIA A DEFINIR
	FITA LED EM PERFIL, ENCASTRÁVEL NO TETO FALSO, INTERIOR, 4000K
	FITA LED EM PERFIL, ENCASTRÁVEL NO TETO FALSO, EXTERIOR, IP44, 3000K
	INTERRUPTOR SIMPLES DE ENCASTRAR (A=1,10m)
	INTERRUPTOR SIMPLES ESTANQUE DE ENCASTRAR (A=1,10m)
	COMUTADOR DE LUSTRE DE ENCASTRAR (A=1,10m)
	COMUTADOR DE ESCADA DE ENCASTRAR (A=1,10m)
	COMUTADOR DE ESCADA DUPLO DE ENCASTRAR (A=1,10m)
	INVERSOR DE ESCADA SIMPLES DE ENCASTRAR (A=1,10m)
	INTERRUPTOR DE ESTORES DE ENCASTRAR (A=1,10m)
	DETETOR DE MOVIMENTO 360° DE ENCASTRAR
	DETETOR DE MOVIMENTO 180° SALIENTE

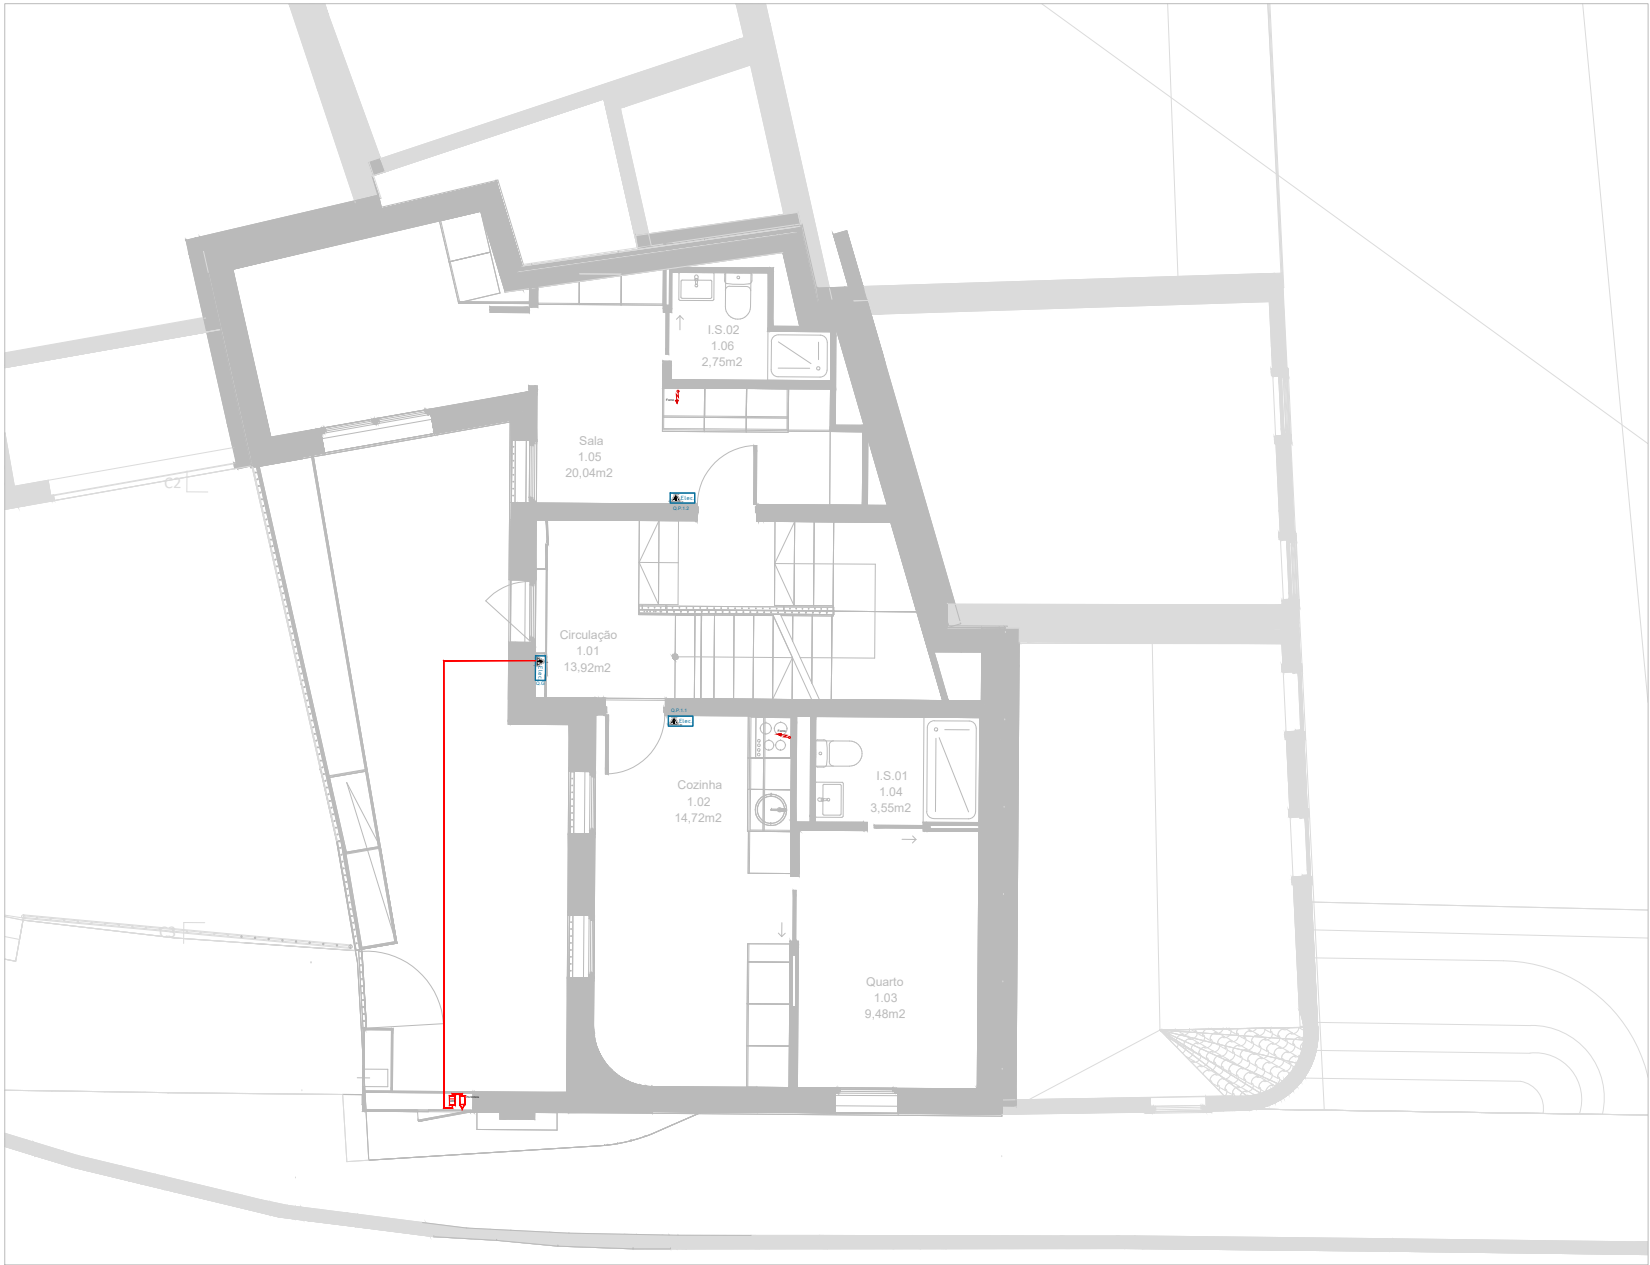

00	Entrega do Projeto de Execução	23.01.2026
Revisão	Descrição	Data

TUU

Requerente
BRUNO EXCELSO
Projeto
MBERAL
RUA EXCELSO, Nº 31,
00002 COIMBRA

Especialidade
PROJETO DE ELETRICIDADE

Projeto Base
Designação
DISTRIBUIÇÃO DE ENERGIA
ALIMENTAÇÕES ESPECÍFICAS
PISO 1

JANEIRO 2026
1:50

EL001

Observações
ESTE PROJETO DEVERÁ SER LIDO EM CONJUNTO COM AS PEÇAS ESCRITAS, ASSIM COMO, O PROJETO DE ARQUITETURA E AS RESTANTES ESPECIALIDADES.
QUAISQUER DISCREPÂNCIAS DEVERÃO SER COMUNICADAS AO PROJETISTA. TODAS AS MEDIDAS DESTES DESENHO SÃO DE PROJETO E MERAMENTE INDICATIVAS, NECESSITAM SER RETIFICADAS EM OBRA.

Nome Ficheiro
MBERAL_PB_ELE_PD_V00.DWG

Código
24932024

Equipa
EMA GOUVEIA | ENG CIVIL
ANA AGOSTINHO | ENG CIVIL

Reprodução proibida, Dec. Lei 45\85 de 17 de Setembro e código do direito de autor e direitos conexos.

TUU.BUILDING DESIGN MANAGEMENT

arquitetura@tuu.pt www.tuu.pt

LEGENDA:	
	QUADRO ELÉTRICO DO EDIFÍCIO
	TOMADA ELÉTRICA 2P+T, 16A, ENCASTRAR
	TOMADA ELÉTRICA 2P+T, 16A, ENCASTRAR, C/TAMPA IP44
	TOMADA ELÉTRICA 2P+T, 16A, ESTANQUE IP65, ENCASTRAR
	TOMADA ELÉTRICA 2P+T, 16A, ESTANQUE IP65, SALIENTE
	TOMADA DE CHÃO ELETRICIDADE (2 módulos) 1x 2P+T 16A
	ALIMENTAÇÃO ELÉTRICA ESPECÍFICA
	DOWNLIGHT LED COMPACTO DE ENCASTRAR, 2,5W 3000K IP43 Ø27mm
	LUMINÁRIA LED TUBULAR SUSPENSA, 4000K, 931mm ou 1493mm
	LUMINÁRIA TIPO RÉGUA SALIENTE, 1030,1530mm ou 2530mm, 3000K
	LUMINÁRIA LINEAR DE ENCASTRAR, 1530mm, 3000K
	CANDEEIRO SUSPENSO, A DEFINIR
	APLIQUE DE PAREDE SALIENTE RETANGULAR, LUZ DESCENDENTE E ASCENDENTE
	Placa Superfície LED Quadrada 18W 225x225 mm; Ref. efectLED 407
	LUMINÁRIA LED DE ENCASTRAR BALIZADOR, Ø33mm, 2,5W, 3000K, IP65 IK10
	CANDEEIRO LED SUSPENSO, Ø1135mm, 2,5W, 3000K, IP65 IK10
	LUMINÁRIA LED CUBO SALIENTE IP65 3000K EXTERIOR
	Plafon LED 20W PHILIPS CL200; Ref. efectLED 85955
	LUMINÁRIA LED DE ENCASTRAR, 5W, 3000K, IP65 IK10
	PONTO DE ILUMINAÇÃO EXTERIOR A DEFINIR, JARDIM, IP65<
	PONTO DE ILUMINAÇÃO TETO OU PAREDE - LUMINÁRIA A DEFINIR
	FITA LED EM PERFIL, ENCASTRÁVEL NO TETO FALSO, INTERIOR, 4000K
	FITA LED EM PERFIL, ENCASTRÁVEL NO TETO FALSO, EXTERIOR, IP44, 3000K
	INTERRUPTOR SIMPLES DE ENCASTRAR (A=1,10m)
	INTERRUPTOR SIMPLES ESTANQUE DE ENCASTRAR (A=1,10m)
	COMUTADOR DE LUSTRE DE ENCASTRAR (A=1,10m)
	COMUTADOR DE ESCADA DE ENCASTRAR (A=1,10m)
	COMUTADOR DE ESCADA DUPLO DE ENCASTRAR (A=1,10m)
	INVERSOR DE ESCADA SIMPLES DE ENCASTRAR (A=1,10m)
	INTERRUPTOR DE ESTORES DE ENCASTRAR (A=1,10m)
	DETETOR DE MOVIMENTO 360° DE ENCASTRAR
	DETETOR DE MOVIMENTO 180° SALIENTE



00	Entrega do Projeto de Execução	23.01.2026
Revisão	Descrição	Data

TUU

Requerente

BRU
NO
EXE
EMPL
O

Projeto

MBERAL

000 0-0 02 RU A EX EM PL O 5, Nº 31,
COIMBRA

Especialidade

PROJETO DE ELETRICIDADE

PROJETO BASE

Designação

DISTRIBUIÇÃO DE ENERGIA
ALIMENTAÇÕES ESPECÍFICAS
PISO 2

JANEIRO 2026

1:50

EL002

Observações

ESTE PROJETO DEVERÁ SER LIDO EM CONJUNTO COM AS PEÇAS
ESCRITAS, ASSIM COMO, O PROJETO DE ARQUITETURA E AS
REstantes ESPECIALIDADES.
QUAISQUER DISCREPÂNCIAS DEVERÃO SER COMUNICADAS AO
PROJETISTA. TODAS AS MEDIDAS DESTES DESENHO SÃO DE
PROJETO E MERAMENTE INDICATIVAS, NECESSITAM SER
RETIFICADAS EM OBRA.

Nome Ficheiro

MBERAL_PB_ELE_PD_V00.DWG

Código

24932024

Equipa

EMA GOUVEIA | ENG CIVIL
ANA AGOSTINHO | ENG CIVIL


Reprodução proibida, Dec. Lei 45\85 de 17 de
Setembro e código do direito de autor e
direitos conexos.

TUU.BUILDING DESIGN MANAGEMENT

arquitetura@tuu.pt

www.tuu.pt

LEGENDA:	
	QUADRO ELÉTRICO DO EDIFÍCIO
	TOMADA ELÉTRICA 2P+T, 16A, ENCASTRAR
	TOMADA ELÉTRICA 2P+T, 16A, ENCASTRAR, C/TAMPA IP44
	TOMADA ELÉTRICA 2P+T, 16A, ESTANQUE IP65, ENCASTRAR
	TOMADA ELÉTRICA 2P+T, 16A, ESTANQUE IP65, SALIENTE
	TOMADA DE CHÃO ELETRICIDADE (2 módulos) 1x 2P+T 16A
	ALIMENTAÇÃO ELÉTRICA ESPECÍFICA
	DOWNLIGHT LED COMPACTO DE ENCASTRAR, 2,5W 3000K IP43 Ø27mm
	LUMINÁRIA LED TUBULAR SUSPENSA, 4000K, 931mm ou 1493mm
	LUMINÁRIA TIPO RÉGUA SALIENTE, 1030,1530mm ou 2530mm, 3000K
	LUMINÁRIA LINEAR DE ENCASTRAR, 1530mm, 3000K
	CANDEEIRO SUSPENSO, A DEFINIR
	APLIQUE DE PAREDE SALIENTE RETANGULAR, LUZ DESCENDENTE E ASCENDENTE
	Placa Superfície LED Quadrada 18W 225x225 mm; Ref. efectLED 407
	LUMINÁRIA LED DE ENCASTRAR BALIZADOR, Ø33mm, 2,5W, 3000K, IP65 IK10
	CANDEEIRO LED SUSPENSO, Ø1135mm, 2,5W, 3000K, IP65 IK10
	LUMINÁRIA LED CUBO SALIENTE IP65 3000K EXTERIOR
	Plafon LED 20W PHILIPS CL200; Ref. efectLED 85955
	LUMINÁRIA LED DE ENCASTRAR, 5W, 3000K, IP65 IK10
	PONTO DE ILUMINAÇÃO EXTERIOR A DEFINIR, JARDIM, IP65<
	PONTO DE ILUMINAÇÃO TETO OU PAREDE - LUMINÁRIA A DEFINIR
	FITA LED EM PERFIL, ENCASTRÁVEL NO TETO FALSO, INTERIOR, 4000K
	FITA LED EM PERFIL, ENCASTRÁVEL NO TETO FALSO, EXTERIOR, IP44, 3000K
	INTERRUPTOR SIMPLES DE ENCASTRAR (A=1,10m)
	INTERRUPTOR SIMPLES ESTANQUE DE ENCASTRAR (A=1,10m)
	COMUTADOR DE LUSTRE DE ENCASTRAR (A=1,10m)
	COMUTADOR DE ESCADA DE ENCASTRAR (A=1,10m)
	COMUTADOR DE ESCADA DUPLO DE ENCASTRAR (A=1,10m)
	INVERSOR DE ESCADA SIMPLES DE ENCASTRAR (A=1,10m)
	INTERRUPTOR DE ESTORES DE ENCASTRAR (A=1,10m)
	DETETOR DE MOVIMENTO 360° DE ENCASTRAR
	DETETOR DE MOVIMENTO 180° SALIENTE

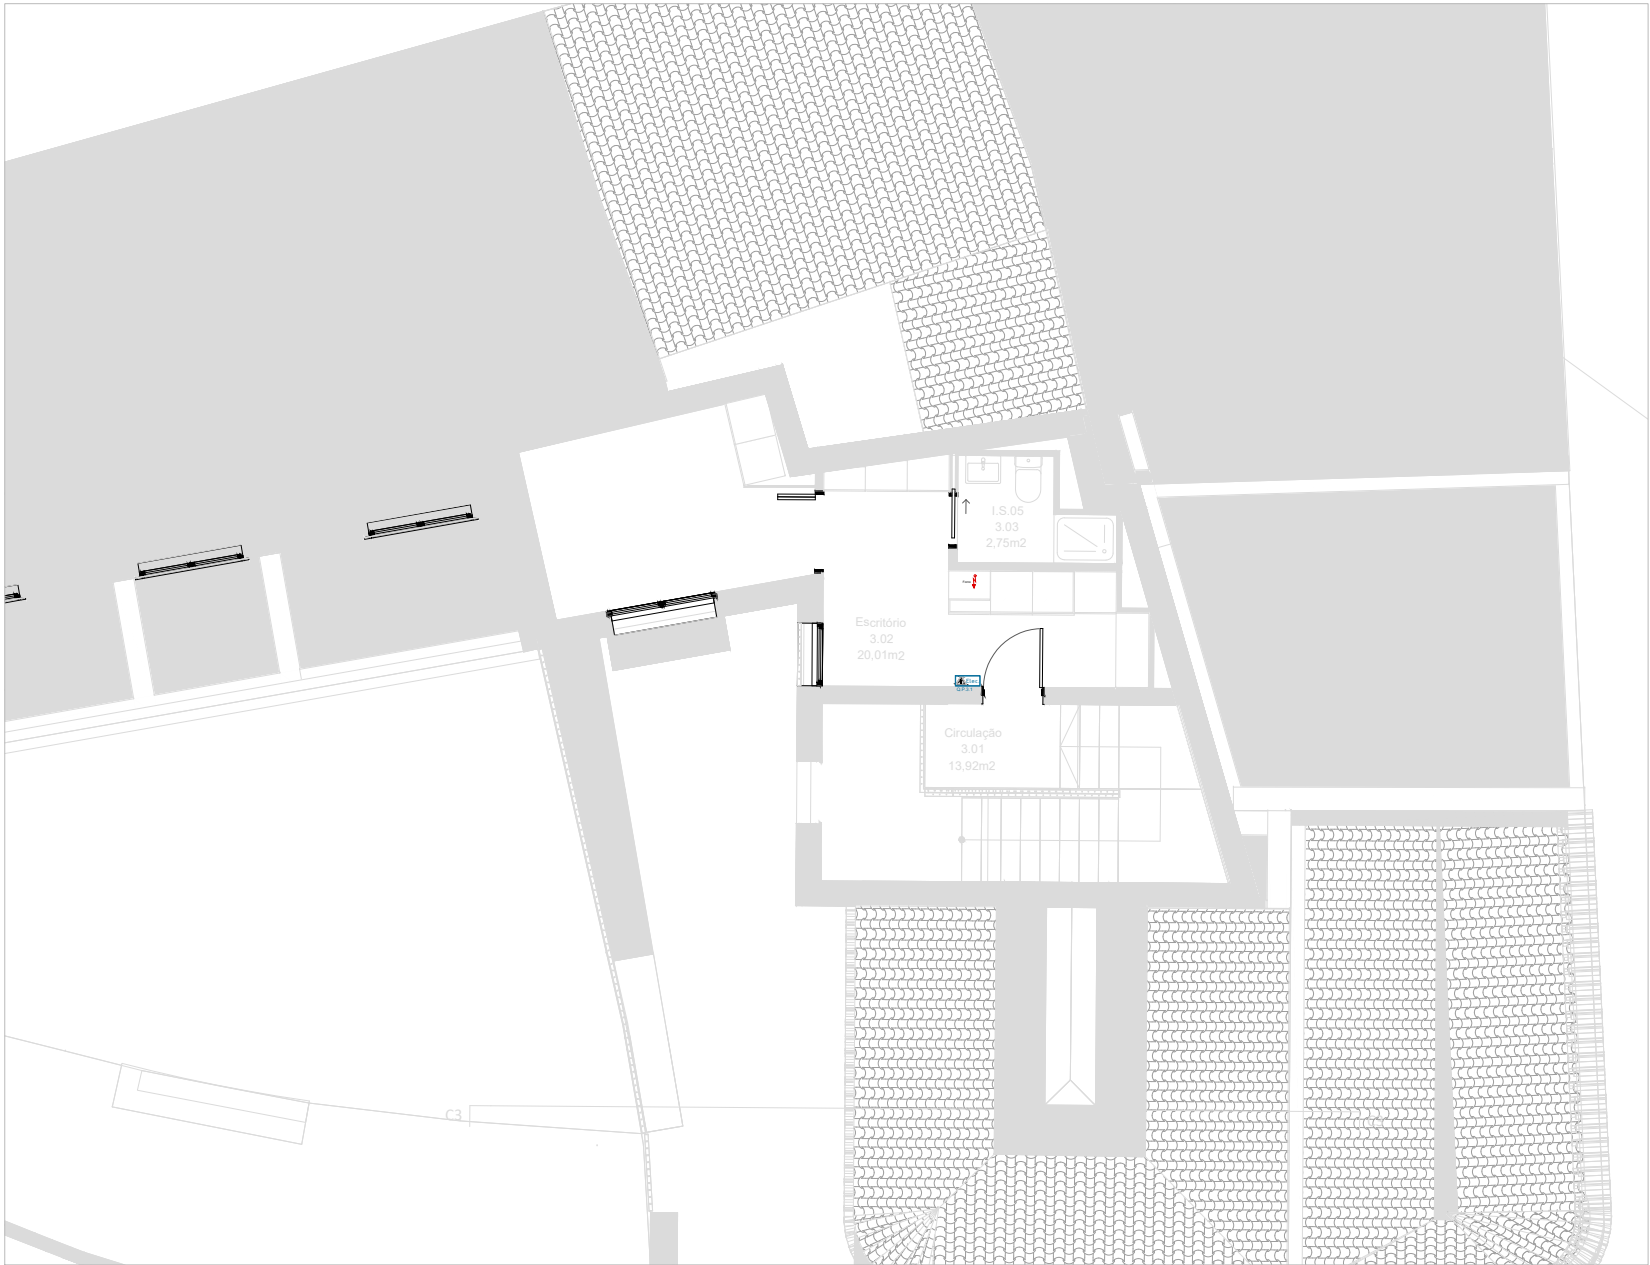

00	Entrega do Projeto de Execução	23.01.2026
Revisão	Descrição	Data

TUU

Requerente

BRU
NO
EXE
MPL
O

Projeto

MBERAL

000 0-0 02 RU A EX EM PL O 5, Nº 31,
COIMBRA

Especialidade

PROJETO DE ELETRICIDADE

PROJETO BASE

Designação

DISTRIBUIÇÃO DE ENERGIA
ALIMENTAÇÕES ESPECÍFICAS
PISO 3

JANEIRO 2026

1:50

EL003

Observações

ESTE PROJETO DEVERÁ SER LIDO EM CONJUNTO COM AS PEÇAS
ESCRITAS, ASSIM COMO, O PROJETO DE ARQUITETURA E AS
REstantes ESPECIALIDADES.
QUAISQUER DISCREPÂNCIAS DEVERÃO SER COMUNICADAS AO
PROJETISTA. TODAS AS MEDIDAS DESTES DESENHO SÃO DE
PROJETO E MERAMENTE INDICATIVAS, NECESSITAM SER
RETIFICADAS EM OBRA.

Nome Ficheiro

MBERAL_PB_ELE_PD_V00.DWG

Código

24932024

Equipa

EMA GOUVEIA | ENG CIVIL
ANA AGOSTINHO | ENG CIVIL

Reprodução proibida, Dec. Lei 45\85 de 17 de
Setembro e código do direito de autor e
direitos conexos.

TUU.BUILDING DESIGN MANAGEMENT

arquitetura@tuu.pt

www.tuu.pt

LEGENDA:	
	QUADRO ELÉTRICO DO EDIFÍCIO
	TOMADA ELÉTRICA 2P+T, 16A, ENCASTRAR
	TOMADA ELÉTRICA 2P+T, 16A, ENCASTRAR, C/TAMPA IP44
	TOMADA ELÉTRICA 2P+T, 16A, ESTANQUE IP65, ENCASTRAR
	TOMADA ELÉTRICA 2P+T, 16A, ESTANQUE IP65, SALIENTE
	TOMADA DE CHÃO ELETRICIDADE (2 módulos) 1x 2P+T 16A
	ALIMENTAÇÃO ELÉTRICA ESPECÍFICA
	DOWNLIGHT LED COMPACTO DE ENCASTRAR, 2,5W 3000K IP43 Ø27mm
	LUMINÁRIA LED TUBULAR SUSPensa, 4000K, 931mm ou 1493mm
	LUMINÁRIA TIPO RÉGUA SALIENTE, 1030,1530mm ou 2530mm, 3000K
	LUMINÁRIA LINEAR DE ENCASTRAR, 1530mm, 3000K
	CANDEEIRO SUSPENSO, A DEFINIR
	APLIQUE DE PAREDE SALIENTE RETANGULAR, LUZ DESCENDENTE E ASCENDENTE
	Placa Superfície LED Quadrada 18W 225x225 mm; Ref. efectaLED 407
	LUMINÁRIA LED DE ENCASTRAR BALIZADOR, Ø33mm, 2,5W, 3000K, IP65 IK10
	CANDEEIRO LED SUSPENSO, Ø1135mm, 2,5W, 3000K, IP65 IK10
	LUMINÁRIA LED CUBO SALIENTE IP65 3000K EXTERIOR
	Plafon LED 20W PHILIPS CL200; Ref. efectaLED 85955
	LUMINÁRIA LED DE ENCASTRAR, 5W, 3000K, IP65 IK10
	PONTO DE ILUMINAÇÃO EXTERIOR A DEFINIR, JARDIM, IP65<
	PONTO DE ILUMINAÇÃO TETO OU PAREDE - LUMINÁRIA A DEFINIR
	FITA LED EM PERFIL, ENCASTRÁVEL NO TETO FALSO, INTERIOR, 4000K
	FITA LED EM PERFIL, ENCASTRÁVEL NO TETO FALSO, EXTERIOR, IP44, 3000K
	INTERRUPTOR SIMPLES DE ENCASTRAR (A=1,10m)
	INTERRUPTOR SIMPLES ESTANQUE DE ENCASTRAR (A=1,10m)
	COMUTADOR DE LUSTRE DE ENCASTRAR (A=1,10m)
	COMUTADOR DE ESCADA DE ENCASTRAR (A=1,10m)
	COMUTADOR DE ESCADA DUPLO DE ENCASTRAR (A=1,10m)
	INVERSOR DE ESCADA SIMPLES DE ENCASTRAR (A=1,10m)
	INTERRUPTOR DE ESTORES DE ENCASTRAR (A=1,10m)
	DETETOR DE MOVIMENTO 360° DE ENCASTRAR
	DETETOR DE MOVIMENTO 180° SALIENTE



00	Entrega do Projeto de Execução	23.01.2026
Revisão	Descrição	Data

TUU

Requerente

BRUNO
NOBRE
ESTRELA
FILHO

Projeto

MBERAL

000 0-0 02 RU A EX EM PL O 5, Nº 31,
COIMBRA

Especialidade

PROJETO DE ELETRICIDADE

PROJETO BASE

Designação

TOMADAS DE USO GERAL
PISO 1

JANEIRO 2026

1:50

EL004

Observações

ESTE PROJETO DEVERÁ SER LIDO EM CONJUNTO COM AS PEÇAS ESCRITAS, ASSIM COMO, O PROJETO DE ARQUITETURA E AS RESTANTES ESPECIALIDADES. QUAISQUER DISCREPÂNCIAS DEVERÃO SER COMUNICADAS AO PROJETISTA. TODAS AS MEDIDAS DESTES DESENHOS SÃO DE PROJETO E MERAMENTE INDICATIVAS, NECESSITAM SER RETIFICADAS EM OBRA.

Nome Ficheiro

MBERAL_PB_ELE_PD_V00.DWG

Código

24932024

Equipa

EMA GOUVEIA | ENG CIVIL
ANA AGOSTINHO | ENG CIVIL

Reprodução proibida, Dec. Lei 45\85 de 17 de Setembro e código do direito de autor e direitos conexos.

TUU.BUILDING DESIGN MANAGEMENT

arquitetura@tuu.pt

www.tuu.pt

LEGENDA:	
	QUADRO ELÉTRICO DO EDIFÍCIO
	TOMADA ELÉTRICA 2P+T, 16A, ENCASTRAR
	TOMADA ELÉTRICA 2P+T, 16A, ENCASTRAR, C/TAMPA IP44
	TOMADA ELÉTRICA 2P+T, 16A, ESTANQUE IP65, ENCASTRAR
	TOMADA ELÉTRICA 2P+T, 16A, ESTANQUE IP65, SALIENTE
	TOMADA DE CHÃO ELETRICIDADE (2 módulos) 1x 2P+T 16A
	ALIMENTAÇÃO ELÉTRICA ESPECÍFICA
	DOWNLIGHT LED COMPACTO DE ENCASTRAR, 2,5W 3000K IP43 Ø27mm
	LUMINÁRIA LED TUBULAR SUSPensa, 4000K, 931mm ou 1493mm
	LUMINÁRIA TIPO RÉGUA SALIENTE, 1030,1530mm ou 2530mm, 3000K
	LUMINÁRIA LINEAR DE ENCASTRAR, 1530mm, 3000K
	CANDEEIRO SUSPENSO, A DEFINIR
	APLIQUE DE PAREDE SALIENTE RETANGULAR, LUZ DESCENDENTE E ASCENDENTE
	Placa Superfície LED Quadrada 18W 225x225 mm; Ref. efectLED 407
	LUMINÁRIA LED DE ENCASTRAR BALIZADOR, Ø33mm, 2,5W, 3000K, IP65 IK10
	CANDEEIRO LED SUSPENSO, Ø1135mm, 2,5W, 3000K, IP65 IK10
	LUMINÁRIA LED CUBO SALIENTE IP65 3000K EXTERIOR
	Plafon LED 20W PHILIPS CL200; Ref. efectLED 85955
	LUMINÁRIA LED DE ENCASTRAR, 5W, 3000K, IP65 IK10
	PONTO DE ILUMINAÇÃO EXTERIOR A DEFINIR, JARDIM, IP65<
	PONTO DE ILUMINAÇÃO TETO OU PAREDE - LUMINÁRIA A DEFINIR
	FITA LED EM PERFIL, ENCASTRÁVEL NO TETO FALSO, INTERIOR, 4000K
	FITA LED EM PERFIL, ENCASTRÁVEL NO TETO FALSO, EXTERIOR, IP44, 3000K
	INTERRUPTOR SIMPLES DE ENCASTRAR (A=1,10m)
	INTERRUPTOR SIMPLES ESTANQUE DE ENCASTRAR (A=1,10m)
	COMUTADOR DE LUSTRE DE ENCASTRAR (A=1,10m)
	COMUTADOR DE ESCADA DE ENCASTRAR (A=1,10m)
	COMUTADOR DE ESCADA DUPLO DE ENCASTRAR (A=1,10m)
	INVERSOR DE ESCADA SIMPLES DE ENCASTRAR (A=1,10m)
	INTERRUPTOR DE ESTORES DE ENCASTRAR (A=1,10m)
	DETETOR DE MOVIMENTO 360° DE ENCASTRAR
	DETETOR DE MOVIMENTO 180° SALIENTE



00	Entrega do Projeto de Execução	23.01.2026
Revisão	Descrição	Data

TUU

Requerente

BRU
NO
EXE
EMPL
O

Projeto

MBERAL

000 0-0 02 RU A EX EM PL O 5, Nº 31,
COIMBRA

Especialidade

PROJETO DE ELETRICIDADE

PROJETO BASE

Designação

TOMADAS DE USO GERAL
PISO 2

JANEIRO 2026

1:50

EL005

Observações

ESTE PROJETO DEVERÁ SER LIDO EM CONJUNTO COM AS PEÇAS
ESCRITAS, ASSIM COMO, O PROJETO DE ARQUITETURA E AS
REstantES ESPECIALIDADES.
QUAISQUER DISCREPÂNCIAS DEVERÃO SER COMUNICADAS AO
PROJETISTA. TODAS AS MEDIDAS DESTES DESENHO SÃO DE
PROJETO E MERAMENTE INDICATIVAS, NECESSITAM SER
RETIFICADAS EM OBRA.

Nome Ficheiro

MBERAL_PB_ELE_PD_V00.DWG

Código

24932024

Equipa

EMA GOUVEIA | ENG CIVIL
ANA AGOSTINHO | ENG CIVIL


Reprodução proibida, Dec. Lei 45\85 de 17 de
Setembro e código do direito de autor e
direitos conexos.

TUU.BUILDING DESIGN MANAGEMENT

arquitetura@tuu.pt

www.tuu.pt

LEGENDA:	
	QUADRO ELÉTRICO DO EDIFÍCIO
	TOMADA ELÉTRICA 2P+T, 16A, ENCASTRAR
	TOMADA ELÉTRICA 2P+T, 16A, ENCASTRAR, C/TAMPA IP44
	TOMADA ELÉTRICA 2P+T, 16A, ESTANQUE IP65, ENCASTRAR
	TOMADA ELÉTRICA 2P+T, 16A, ESTANQUE IP65, SALIENTE
	TOMADA DE CHÃO ELETRICIDADE (2 módulos) 1x 2P+T 16A
	ALIMENTAÇÃO ELÉTRICA ESPECÍFICA
	DOWNLIGHT LED COMPACTO DE ENCASTRAR, 2,5W 3000K IP43 Ø27mm
	LUMINÁRIA LED TUBULAR SUSPENSA, 4000K, 931mm ou 1493mm
	LUMINÁRIA TIPO RÉGUA SALIENTE, 1030,1530mm ou 2530mm, 3000K
	LUMINÁRIA LINEAR DE ENCASTRAR, 1530mm, 3000K
	CANDEEIRO SUSPENSO, A DEFINIR
	APLIQUE DE PAREDE SALIENTE RETANGULAR, LUZ DESCENDENTE E ASCENDENTE
	Placa Superfície LED Quadrada 18W 225x225 mm; Ref. efectLED 407
	LUMINÁRIA LED DE ENCASTRAR BALIZADOR, Ø33mm, 2,5W, 3000K, IP65 IK10
	CANDEEIRO LED SUSPENSO, Ø1135mm, 2,5W, 3000K, IP65 IK10
	LUMINÁRIA LED CUBO SALIENTE IP65 3000K EXTERIOR
	Plafon LED 20W PHILIPS CL200; Ref. efectLED 85955
	LUMINÁRIA LED DE ENCASTRAR, 5W, 3000K, IP65 IK10
	PONTO DE ILUMINAÇÃO EXTERIOR A DEFINIR, JARDIM, IP65<
	PONTO DE ILUMINAÇÃO TETO OU PAREDE - LUMINÁRIA A DEFINIR
	FITA LED EM PERFIL, ENCASTRÁVEL NO TETO FALSO, INTERIOR, 4000K
	FITA LED EM PERFIL, ENCASTRÁVEL NO TETO FALSO, EXTERIOR, IP44, 3000K
	INTERRUPTOR SIMPLES DE ENCASTRAR (A=1,10m)
	INTERRUPTOR SIMPLES ESTANQUE DE ENCASTRAR (A=1,10m)
	COMUTADOR DE LUSTRE DE ENCASTRAR (A=1,10m)
	COMUTADOR DE ESCADA DE ENCASTRAR (A=1,10m)
	COMUTADOR DE ESCADA DUPLO DE ENCASTRAR (A=1,10m)
	INVERSOR DE ESCADA SIMPLES DE ENCASTRAR (A=1,10m)
	INTERRUPTOR DE ESTORES DE ENCASTRAR (A=1,10m)
	DETETOR DE MOVIMENTO 360° DE ENCASTRAR
	DETETOR DE MOVIMENTO 180° SALIENTE

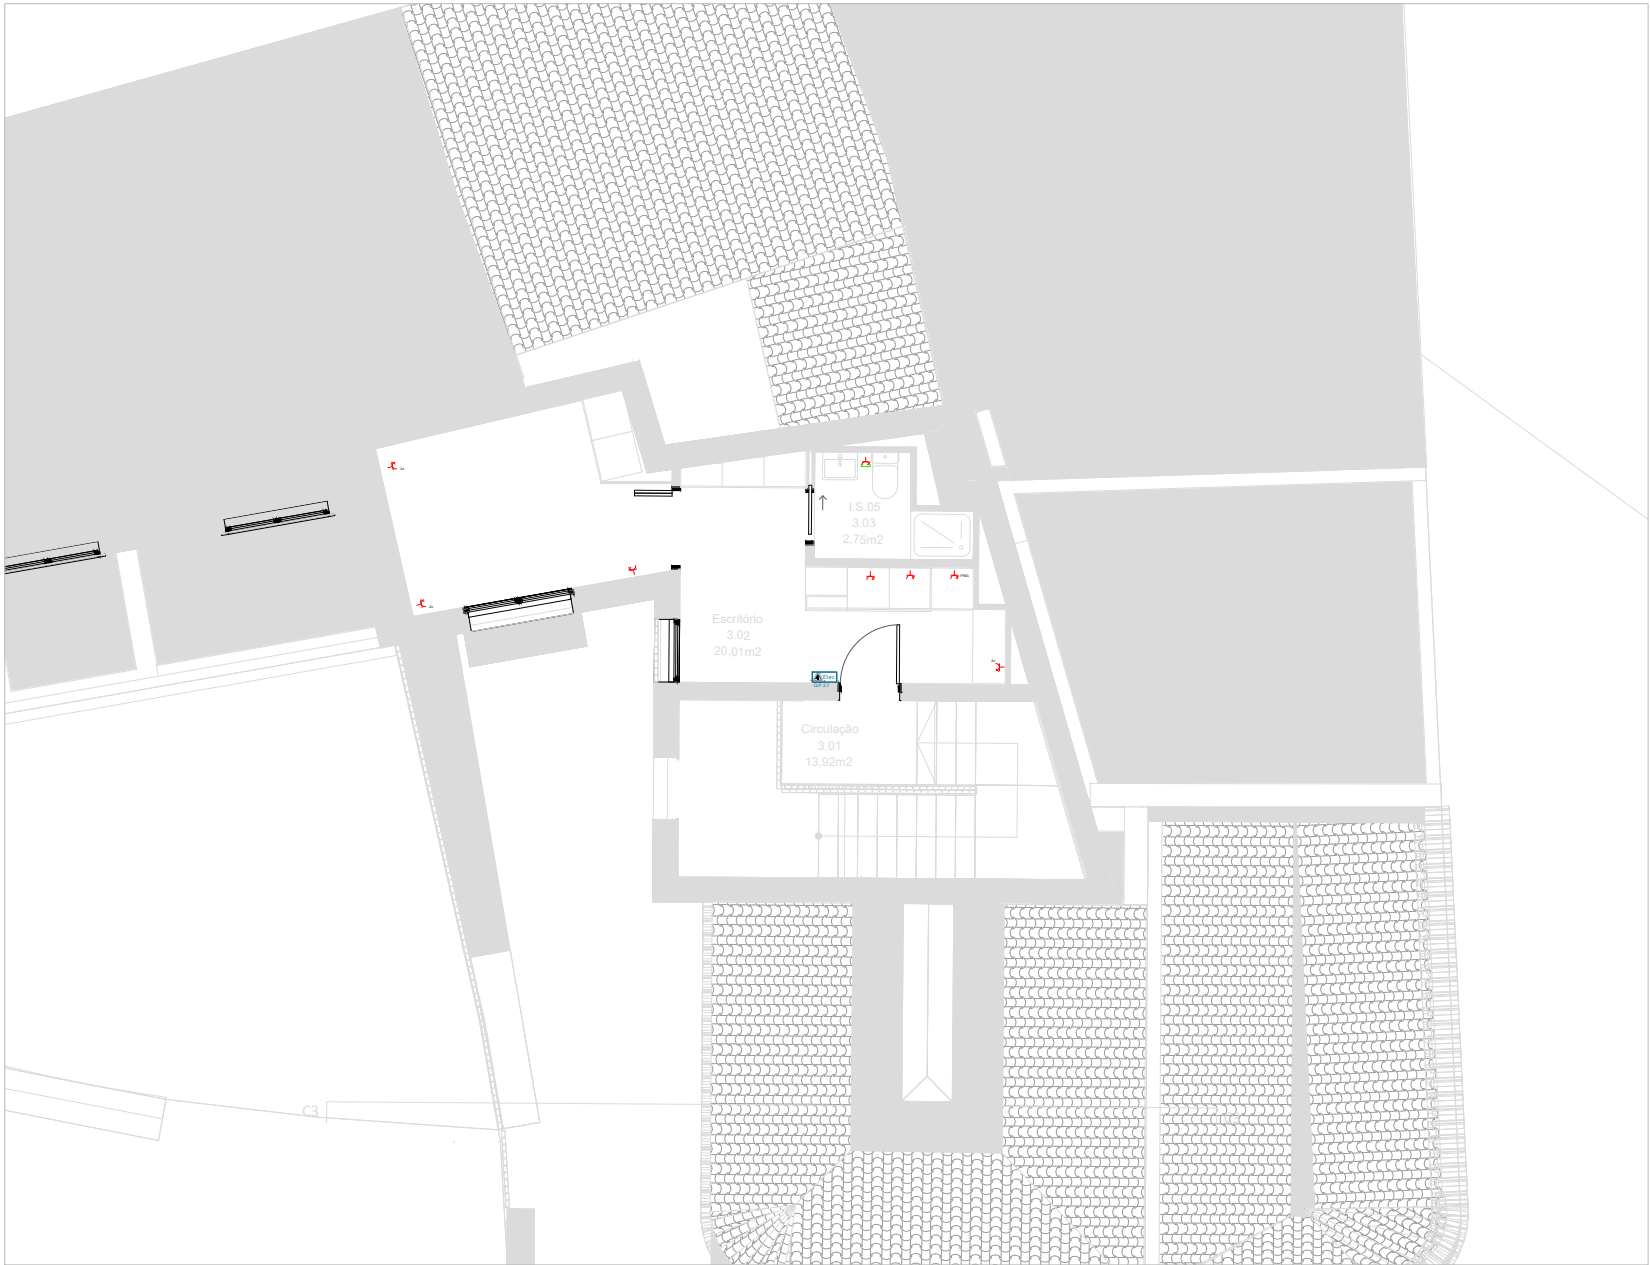

00	Entrega do Projeto de Execução	23.01.2026
Revisão	Descrição	Data

TUU

Requerente

BRU
NO
EXE
EMPL
O

Projeto

MBERAL

000 0-0 02 RU A EX EM PL O 5, Nº 31,
COIMBRA

Especialidade

PROJETO DE ELETRICIDADE

PROJETO BASE

Designação

TOMADAS DE USO GERAL
PISO 3

JANEIRO 2026

1:50

EL006

Observações

ESTE PROJETO DEVERÁ SER LIDO EM CONJUNTO COM AS PEÇAS
ESCRITAS, ASSIM COMO, O PROJETO DE ARQUITETURA E AS
REstantes ESPECIALIDADES.
QUAISQUER DISCREPÂNCIAS DEVERÃO SER COMUNICADAS AO
PROJETISTA. TODAS AS MEDIDAS DESTES DESENHO SÃO DE
PROJETO E MERAMENTE INDICATIVAS, NECESSITAM SER
RETIFICADAS EM OBRA.

Nome Ficheiro

MBERAL_PB_ELE_PD_V00.DWG

Código

24932024

Equipa

EMA GOUVEIA | ENG CIVIL
ANA AGOSTINHO | ENG CIVIL

Reprodução proibida, Dec. Lei 45\85 de 17 de
Setembro e código do direito de autor e
direitos conexos.

TUU.BUILDING DESIGN MANAGEMENT

arquitetura@tuu.pt

www.tuu.pt

LEGENDA:	
	QUADRO ELÉTRICO DO EDIFÍCIO
	TOMADA ELÉTRICA 2P+T, 16A, ENCASTRAR
	TOMADA ELÉTRICA 2P+T, 16A, ENCASTRAR, C/TAMPA IP44
	TOMADA ELÉTRICA 2P+T, 16A, ESTANQUE IP65, ENCASTRAR
	TOMADA ELÉTRICA 2P+T, 16A, ESTANQUE IP65, SALIENTE
	TOMADA DE CHÃO ELETRICIDADE (2 módulos) 1x 2P+T 16A
	ALIMENTAÇÃO ELÉTRICA ESPECÍFICA
	DOWNLIGHT LED COMPACTO DE ENCASTRAR, 2,5W 3000K IP43 Ø27mm
	LUMINÁRIA LED TUBULAR SUSPensa, 4000K, 931mm ou 1493mm
	LUMINÁRIA TIPO RÉGUA SALIENTE, 1030,1530mm ou 2530mm, 3000K
	LUMINÁRIA LINEAR DE ENCASTRAR, 1530mm, 3000K
	CANDEEIRO SUSPENSO, A DEFINIR
	APLIQUE DE PAREDE SALIENTE RETANGULAR, LUZ DESCENDENTE E ASCENDENTE
	Placa Superfície LED Quadrada 18W 225x225 mm; Ref. efectLED 407
	LUMINÁRIA LED DE ENCASTRAR BALIZADOR, Ø33mm, 2,5W, 3000K, IP65 IK10
	CANDEEIRO LED SUSPENSO, Ø1135mm, 2,5W, 3000K, IP65 IK10
	LUMINÁRIA LED CUBO SALIENTE IP65 3000K EXTERIOR
	Plafon LED 20W PHILIPS CL200; Ref. efectLED 85955
	LUMINÁRIA LED DE ENCASTRAR, 5W, 3000K, IP65 IK10
	PONTO DE ILUMINAÇÃO EXTERIOR A DEFINIR, JARDIM, IP65<
	PONTO DE ILUMINAÇÃO TETO OU PAREDE - LUMINÁRIA A DEFINIR
	FITA LED EM PERFIL, ENCASTRÁVEL NO TETO FALSO, INTERIOR, 4000K
	FITA LED EM PERFIL, ENCASTRÁVEL NO TETO FALSO, EXTERIOR, IP44, 3000K
	INTERRUPTOR SIMPLES DE ENCASTRAR (A=1,10m)
	INTERRUPTOR SIMPLES ESTANQUE DE ENCASTRAR (A=1,10m)
	COMUTADOR DE LUSTRE DE ENCASTRAR (A=1,10m)
	COMUTADOR DE ESCADA DE ENCASTRAR (A=1,10m)
	COMUTADOR DE ESCADA DUPLO DE ENCASTRAR (A=1,10m)
	INVERSOR DE ESCADA SIMPLES DE ENCASTRAR (A=1,10m)
	INTERRUPTOR DE ESTORES DE ENCASTRAR (A=1,10m)
	DETETOR DE MOVIMENTO 360° DE ENCASTRAR
	DETETOR DE MOVIMENTO 180° SALIENTE



00	Entrega do Projeto de Execução	23.01.2026
Revisão	Descrição	Data

TUU

Requerente
BRUNO EXEMPLADO
Projeto
MBERAL
000 0-0 02 COIMBRA, Nº 31,

Especialidade
PROJETO DE ELETRICIDADE

PROJETO BASE

Designação
ILUMINAÇÃO
PISO 1

JANEIRO 2026
1:50

EL007

Observações
ESTE PROJETO DEVERÁ SER LIDO EM CONJUNTO COM AS PEÇAS ESCRITAS, ASSIM COMO, O PROJETO DE ARQUITETURA E AS RESTANTES ESPECIALIDADES.
QUAISQUER DISCREPÂNCIAS DEVERÃO SER COMUNICADAS AO PROJETISTA. TODAS AS MEDIDAS DESTES DESENHOS SÃO DE PROJETO E MERAMENTE INDICATIVAS, NECESSITAM SER RETIFICADAS EM OBRA.

Nome Ficheiro
MBERAL_PB_ELE_PD_V00.DWG

Código
24932024

Equipa
EMA GOUVEIA | ENG CIVIL
ANA AGOSTINHO | ENG CIVIL

Reprodução proibida, Dec. Lei 45/85 de 17 de Setembro e código do direito de autor e direitos conexos.

TUU.BUILDING DESIGN MANAGEMENT

arquitetura@tuu.pt www.tuu.pt

LEGENDA:	
	QUADRO ELÉTRICO DO EDIFÍCIO
	TOMADA ELÉTRICA 2P+T, 16A, ENCASTRAR
	TOMADA ELÉTRICA 2P+T, 16A, ENCASTRAR, C/TAMPA IP44
	TOMADA ELÉTRICA 2P+T, 16A, ESTANQUE IP65, ENCASTRAR
	TOMADA ELÉTRICA 2P+T, 16A, ESTANQUE IP65, SALIENTE
	TOMADA DE CHÃO ELETRICIDADE (2 módulos) 1x 2P+T 16A
	ALIMENTAÇÃO ELÉTRICA ESPECÍFICA
	DOWNLIGHT LED COMPACTO DE ENCASTRAR, 2,5W 3000K IP43 Ø27mm
	LUMINÁRIA LED TUBULAR SUSPENSA, 4000K, 931mm ou 1493mm
	LUMINÁRIA TIPO RÉGUA SALIENTE, 1030,1530mm ou 2530mm, 3000K
	LUMINÁRIA LINEAR DE ENCASTRAR, 1530mm, 3000K
	CANDEEIRO SUSPENSO, A DEFINIR
	APLIQUE DE PAREDE SALIENTE RETANGULAR, LUZ DESCENDENTE E ASCENDENTE
	Placa Superfície LED Quadrada 18W 225x225 mm; Ref. efectoLED 407
	LUMINÁRIA LED DE ENCASTRAR BALIZADOR, Ø33mm, 2,5W, 3000K, IP65 IK10
	CANDEEIRO LED SUSPENSO, Ø1135mm, 2,5W, 3000K, IP65 IK10
	LUMINÁRIA LED CUBO SALIENTE IP65 3000K EXTERIOR
	Plafon LED 20W PHILIPS CL200; Ref. efectoLED 85955
	LUMINÁRIA LED DE ENCASTRAR, 5W, 3000K, IP65 IK10
	PONTO DE ILUMINAÇÃO EXTERIOR A DEFINIR, JARDIM, IP65<
	PONTO DE ILUMINAÇÃO TETO OU PAREDE - LUMINÁRIA A DEFINIR
	FITA LED EM PERFIL, ENCASTRÁVEL NO TETO FALSO, INTERIOR, 4000K
	FITA LED EM PERFIL, ENCASTRÁVEL NO TETO FALSO, EXTERIOR, IP44, 3000K
	INTERRUPTOR SIMPLES DE ENCASTRAR (A=1,10m)
	INTERRUPTOR SIMPLES ESTANQUE DE ENCASTRAR (A=1,10m)
	COMUTADOR DE LUSTRE DE ENCASTRAR (A=1,10m)
	COMUTADOR DE ESCADA DE ENCASTRAR (A=1,10m)
	COMUTADOR DE ESCADA DUPLO DE ENCASTRAR (A=1,10m)
	INVERSOR DE ESCADA SIMPLES DE ENCASTRAR (A=1,10m)
	INTERRUPTOR DE ESTORES DE ENCASTRAR (A=1,10m)
	DETETOR DE MOVIMENTO 360° DE ENCASTRAR
	DETETOR DE MOVIMENTO 180° SALIENTE



00	Entrega do Projeto de Execução	23.01.2026
Revisão	Descrição	Data

TUU

Requerente

BRU
NO
EXE
EMPL
O

Projeto

MBERAL

000 0-0 02 RU A EX EM PL O 5, Nº 31,
COIMBRA

Especialidade

PROJETO DE ELETRICIDADE

PROJETO BASE

Designação

ILUMINAÇÃO
PISO 2

JANEIRO 2026

1:50

EL008

Observações

ESTE PROJETO DEVERÁ SER LIDO EM CONJUNTO COM AS PEÇAS
ESCRITAS, ASSIM COMO, O PROJETO DE ARQUITETURA E AS
REstantes ESPECIALIDADES.
QUAISQUER DISCREPÂNCIAS DEVERÃO SER COMUNICADAS AO
PROJETISTA. TODAS AS MEDIDAS DESTES DESENHO SÃO DE
PROJETO E MERAMENTE INDICATIVAS, NECESSITAM SER
RETIFICADAS EM OBRA.

Nome Ficheiro

MBERAL_PB_ELE_PD_V00.DWG

Código

24932024

Equipa

EMA GOUVEIA | ENG CIVIL
ANA AGOSTINHO | ENG CIVIL

Reprodução proibida, Dec. Lei 45\85 de 17 de
Setembro e código do direito de autor e
direitos conexos.

TUU.BUILDING DESIGN MANAGEMENT

arquitetura@tuu.pt

www.tuu.pt

LEGENDA:	
	QUADRO ELÉTRICO DO EDIFÍCIO
	TOMADA ELÉTRICA 2P+T, 16A, ENCASTRAR
	TOMADA ELÉTRICA 2P+T, 16A, ENCASTRAR, C/TAMPA IP44
	TOMADA ELÉTRICA 2P+T, 16A, ESTANQUE IP65, ENCASTRAR
	TOMADA ELÉTRICA 2P+T, 16A, ESTANQUE IP65, SALIENTE
	TOMADA DE CHÃO ELETRICIDADE (2 módulos) 1x 2P+T 16A
	ALIMENTAÇÃO ELÉTRICA ESPECÍFICA
	DOWNLIGHT LED COMPACTO DE ENCASTRAR, 2,5W 3000K IP43 Ø27mm
	LUMINÁRIA LED TUBULAR SUSPensa, 4000K, 931mm ou 1493mm
	LUMINÁRIA TIPO RÉGUA SALIENTE, 1030,1530mm ou 2530mm, 3000K
	LUMINÁRIA LINEAR DE ENCASTRAR, 1530mm, 3000K
	CANDEEIRO SUSPENSO, A DEFINIR
	APLIQUE DE PAREDE SALIENTE RETANGULAR, LUZ DESCENDENTE E ASCENDENTE
	Placa Superfície LED Quadrada 18W 225x225 mm; Ref. efectLED 407
	LUMINÁRIA LED DE ENCASTRAR BALIZADOR, Ø33mm, 2,5W, 3000K, IP65 IK10
	CANDEEIRO LED SUSPENSO, Ø1135mm, 2,5W, 3000K, IP65 IK10
	LUMINÁRIA LED CUBO SALIENTE IP65 3000K EXTERIOR
	Plafon LED 20W PHILIPS CL200; Ref. efectLED 85955
	LUMINÁRIA LED DE ENCASTRAR, 5W, 3000K, IP65 IK10
	PONTO DE ILUMINAÇÃO EXTERIOR A DEFINIR, JARDIM, IP65<
	PONTO DE ILUMINAÇÃO TETO OU PAREDE - LUMINÁRIA A DEFINIR
	FITA LED EM PERFIL, ENCASTRÁVEL NO TETO FALSO, INTERIOR, 4000K
	FITA LED EM PERFIL, ENCASTRÁVEL NO TETO FALSO, EXTERIOR, IP44, 3000K
	INTERRUPTOR SIMPLES DE ENCASTRAR (A=1,10m)
	INTERRUPTOR SIMPLES ESTANQUE DE ENCASTRAR (A=1,10m)
	COMUTADOR DE LUSTRE DE ENCASTRAR (A=1,10m)
	COMUTADOR DE ESCADA DE ENCASTRAR (A=1,10m)
	COMUTADOR DE ESCADA DUPLO DE ENCASTRAR (A=1,10m)
	INVERSOR DE ESCADA SIMPLES DE ENCASTRAR (A=1,10m)
	INTERRUPTOR DE ESTORES DE ENCASTRAR (A=1,10m)
	DETETOR DE MOVIMENTO 360° DE ENCASTRAR
	DETETOR DE MOVIMENTO 180° SALIENTE



00	Entrega do Projeto de Execução	23.01.2026
Revisão	Descrição	Data

TUU

Requerente
BRUNO EXEMPLADO
Projeto
MBERAL
000 0-0 02 COIMBRA, Nº 31,
Rua Alexandre de Gusmão, 31, 4.º andar, 3010-001 Coimbra, Portugal
Especialidade
PROJETO DE ELETRICIDADE
PROJETO BASE
Designação
ILUMINAÇÃO
PISO 3

JANEIRO 2026
1:50

EL009

Observações
ESTE PROJETO DEVERÁ SER LIDO EM CONJUNTO COM AS PEÇAS ESCRITAS, ASSIM COMO, O PROJETO DE ARQUITETURA E AS RESTANTES ESPECIALIDADES.
QUAISQUER DISCREPÂNCIAS DEVERÃO SER COMUNICADAS AO PROJETISTA. TODAS AS MEDIDAS DESTES DESENHOS SÃO DE PROJETO E MERAMENTE INDICATIVAS, NECESSITAM SER RETIFICADAS EM OBRA.

Nome Ficheiro
MBERAL_PB_ELE_PD_V00.DWG

Código
24932024

Equipa
EMA GOUVEIA | ENG CIVIL
ANA AGOSTINHO | ENG CIVIL

Reprodução proibida, Dec. Lei 45/85 de 17 de Setembro e código do direito de autor e direitos conexos.

TUU.BUILDING DESIGN MANAGEMENT
arquitetura@tuu.pt www.tuu.pt

LEGENDA:	
	QUADRO ELÉTRICO DO EDIFÍCIO
	TOMADA ELÉTRICA 2P+T, 16A, ENCASTRAR
	TOMADA ELÉTRICA 2P+T, 16A, ENCASTRAR, C/TAMPA IP44
	TOMADA ELÉTRICA 2P+T, 16A, ESTANQUE IP65, ENCASTRAR
	TOMADA ELÉTRICA 2P+T, 16A, ESTANQUE IP65, SALIENTE
	TOMADA DE CHÃO ELETRICIDADE (2 módulos) 1x 2P+T 16A
	ALIMENTAÇÃO ELÉTRICA ESPECÍFICA
	DOWNLIGHT LED COMPACTO DE ENCASTRAR, 2,5W 3000K IP43 Ø27mm
	LUMINÁRIA LED TUBULAR SUSPENSA, 4000K, 931mm ou 1493mm
	LUMINÁRIA TIPO RÉGUA SALIENTE, 1030,1530mm ou 2530mm, 3000K
	LUMINÁRIA LINEAR DE ENCASTRAR, 1530mm, 3000K
	CANDEEIRO SUSPENSO, A DEFINIR
	APLIQUE DE PAREDE SALIENTE RETANGULAR, LUZ DESCENDENTE E ASCENDENTE
	Placa Superfície LED Quadrada 18W 225x225 mm; Ref. efectLED 407
	LUMINÁRIA LED DE ENCASTRAR BALIZADOR, Ø33mm, 2,5W, 3000K, IP65 IK10
	CANDEEIRO LED SUSPENSO, Ø1135mm, 2,5W, 3000K, IP65 IK10
	LUMINÁRIA LED CUBO SALIENTE IP65 3000K EXTERIOR
	Plafon LED 20W PHILIPS CL200; Ref. efectLED 85955
	LUMINÁRIA LED DE ENCASTRAR, 5W, 3000K, IP65 IK10
	PONTO DE ILUMINAÇÃO EXTERIOR A DEFINIR, JARDIM, IP65<
	PONTO DE ILUMINAÇÃO TETO OU PAREDE - LUMINÁRIA A DEFINIR
	FITA LED EM PERFIL, ENCASTRÁVEL NO TETO FALSO, INTERIOR, 4000K
	FITA LED EM PERFIL, ENCASTRÁVEL NO TETO FALSO, EXTERIOR, IP44, 3000K
	INTERRUPTOR SIMPLES DE ENCASTRAR (A=1,10m)
	INTERRUPTOR SIMPLES ESTANQUE DE ENCASTRAR (A=1,10m)
	COMUTADOR DE LUSTRE DE ENCASTRAR (A=1,10m)
	COMUTADOR DE ESCADA DE ENCASTRAR (A=1,10m)
	COMUTADOR DE ESCADA DUPLO DE ENCASTRAR (A=1,10m)
	INVERSOR DE ESCADA SIMPLES DE ENCASTRAR (A=1,10m)
	INTERRUPTOR DE ESTORES DE ENCASTRAR (A=1,10m)
	DETETOR DE MOVIMENTO 360° DE ENCASTRAR
	DETETOR DE MOVIMENTO 180° SALIENTE



00	Entrega do Projeto de Execução	23.01.2026
Revisão	Descrição	Data

TUU

Requerente

BRU
NO
EXE
EMPL
O

Projeto

MBERAL

000 0-0 02 RU A EX EM PL O 5, Nº 31,
COIMBRA

Especialidade

PROJETO DE ELETRICIDADE

PROJETO BASE

Designação

ESTORES
PISO 1

JANEIRO 2026

1:50

EL010

Observações

ESTE PROJETO DEVERÁ SER LIDO EM CONJUNTO COM AS PEÇAS
ESCRITAS, ASSIM COMO, O PROJETO DE ARQUITETURA E AS
REstantes ESPECIALIDADES.
QUAISQUER DISCREPÂNCIAS DEVERÃO SER COMUNICADAS AO
PROJETISTA. TODAS AS MEDIDAS DESTES DESENHO SÃO DE
PROJETO E MERAMENTE INDICATIVAS, NECESSITAM SER
RETIFICADAS EM OBRA.

Nome Ficheiro

MBERAL_PB_ELE_PD_V00.DWG

Código

24932024

Equipa

EMA GOUVEIA | ENG CIVIL
ANA AGOSTINHO | ENG CIVIL

Reprodução proibida, Dec. Lei 45\85 de 17 de
Setembro e código do direito de autor e
direitos conexos.

TUU.BUILDING DESIGN MANAGEMENT

arquitetura@tuu.pt

www.tuu.pt

LEGENDA:	
	QUADRO ELÉTRICO DO EDIFÍCIO
	TOMADA ELÉTRICA 2P+T, 16A, ENCASTRAR
	TOMADA ELÉTRICA 2P+T, 16A, ENCASTRAR, C/TAMPA IP44
	TOMADA ELÉTRICA 2P+T, 16A, ESTANQUE IP65, ENCASTRAR
	TOMADA ELÉTRICA 2P+T, 16A, ESTANQUE IP65, SALIENTE
	TOMADA DE CHÃO ELETRICIDADE (2 módulos) 1x 2P+T 16A
	ALIMENTAÇÃO ELÉTRICA ESPECÍFICA
	DOWNLIGHT LED COMPACTO DE ENCASTRAR, 2,5W 3000K IP43 Ø27mm
	LUMINÁRIA LED TUBULAR SUSPENSA, 4000K, 931mm ou 1493mm
	LUMINÁRIA TIPO RÉGUA SALIENTE, 1030,1530mm ou 2530mm, 3000K
	LUMINÁRIA LINEAR DE ENCASTRAR, 1530mm, 3000K
	CANDEEIRO SUSPENSO, A DEFINIR
	APLIQUE DE PAREDE SALIENTE RETANGULAR, LUZ DESCENDENTE E ASCENDENTE
	Placa Superfície LED Quadrada 18W 225x225 mm; Ref. efectLED 407
	LUMINÁRIA LED DE ENCASTRAR BALIZADOR, Ø33mm, 2,5W, 3000K, IP65 IK10
	CANDEEIRO LED SUSPENSO, Ø1135mm, 2,5W, 3000K, IP65 IK10
	LUMINÁRIA LED CUBO SALIENTE IP65 3000K EXTERIOR
	Plafon LED 20W PHILIPS CL200; Ref. efectLED 85955
	LUMINÁRIA LED DE ENCASTRAR, 5W, 3000K, IP65 IK10
	PONTO DE ILUMINAÇÃO EXTERIOR A DEFINIR, JARDIM, IP65<
	PONTO DE ILUMINAÇÃO TETO OU PAREDE - LUMINÁRIA A DEFINIR
	FITA LED EM PERFIL, ENCASTRÁVEL NO TETO FALSO, INTERIOR, 4000K
	FITA LED EM PERFIL, ENCASTRÁVEL NO TETO FALSO, EXTERIOR, IP44, 3000K
	INTERRUPTOR SIMPLES DE ENCASTRAR (A=1,10m)
	INTERRUPTOR SIMPLES ESTANQUE DE ENCASTRAR (A=1,10m)
	COMUTADOR DE LUSTRE DE ENCASTRAR (A=1,10m)
	COMUTADOR DE ESCADA DE ENCASTRAR (A=1,10m)
	COMUTADOR DE ESCADA DUPLO DE ENCASTRAR (A=1,10m)
	INVERSOR DE ESCADA SIMPLES DE ENCASTRAR (A=1,10m)
	INTERRUPTOR DE ESTORES DE ENCASTRAR (A=1,10m)
	DETETOR DE MOVIMENTO 360° DE ENCASTRAR
	DETETOR DE MOVIMENTO 180° SALIENTE



00	Entrega do Projeto de Execução	23.01.2026
Revisão	Descrição	Data

TUU

Requerente

BRU
NO
EXE
EMPL
O

Projeto

MBERAL

000 0-0 02 RU A EX EM PL O 5, Nº 31,
COIMBRA

Especialidade

PROJETO DE ELETRICIDADE

PROJETO BASE

Designação

ESTORES
PISO 2

JANEIRO 2026

1:50

EL011

Observações

ESTE PROJETO DEVERÁ SER LIDO EM CONJUNTO COM AS PEÇAS
ESCRITAS, ASSIM COMO, O PROJETO DE ARQUITETURA E AS
REstantes ESPECIALIDADES.
QUAISQUER DISCREPÂNCIAS DEVERÃO SER COMUNICADAS AO
PROJETISTA. TODAS AS MEDIDAS DESTES DESENHO SÃO DE
PROJETO E MERAMENTE INDICATIVAS, NECESSITAM SER
RETIFICADAS EM OBRA.

Nome Ficheiro

MBERAL_PB_ELE_PD_V00.DWG

Código

24932024

Equipa

EMA GOUVEIA | ENG CIVIL
ANA AGOSTINHO | ENG CIVIL


Reprodução proibida, Dec. Lei 45\85 de 17 de
Setembro e código do direito de autor e
direitos conexos.

TUU.BUILDING DESIGN MANAGEMENT

arquitetura@tuu.pt

www.tuu.pt

LEGENDA:	
	QUADRO ELÉTRICO DO EDIFÍCIO
	TOMADA ELÉTRICA 2P+T, 16A, ENCASTRAR
	TOMADA ELÉTRICA 2P+T, 16A, ENCASTRAR, C/TAMPA IP44
	TOMADA ELÉTRICA 2P+T, 16A, ESTANQUE IP65, ENCASTRAR
	TOMADA ELÉTRICA 2P+T, 16A, ESTANQUE IP65, SALIENTE
	TOMADA DE CHÃO ELETRICIDADE (2 módulos) 1x 2P+T 16A
	ALIMENTAÇÃO ELÉTRICA ESPECÍFICA
	DOWNLIGHT LED COMPACTO DE ENCASTRAR, 2,5W 3000K IP43 Ø27mm
	LUMINÁRIA LED TUBULAR SUSPENSA, 4000K, 931mm ou 1493mm
	LUMINÁRIA TIPO RÉGUA SALIENTE, 1030,1530mm ou 2530mm, 3000K
	LUMINÁRIA LINEAR DE ENCASTRAR, 1530mm, 3000K
	CANDEEIRO SUSPENSO, A DEFINIR
	APLIQUE DE PAREDE SALIENTE RETANGULAR, LUZ DESCENDENTE E ASCENDENTE
	Placa Superfície LED Quadrada 18W 225x225 mm; Ref. efectLED 407
	LUMINÁRIA LED DE ENCASTRAR BALIZADOR, Ø33mm, 2,5W, 3000K, IP65 IK10
	CANDEEIRO LED SUSPENSO, Ø1135mm, 2,5W, 3000K, IP65 IK10
	LUMINÁRIA LED CUBO SALIENTE IP65 3000K EXTERIOR
	Plafon LED 20W PHILIPS CL200; Ref. efectLED 85955
	LUMINÁRIA LED DE ENCASTRAR, 5W, 3000K, IP65 IK10
	PONTO DE ILUMINAÇÃO EXTERIOR A DEFINIR, JARDIM, IP65<
	PONTO DE ILUMINAÇÃO TETO OU PAREDE - LUMINÁRIA A DEFINIR
	FITA LED EM PERFIL, ENCASTRÁVEL NO TETO FALSO, INTERIOR, 4000K
	FITA LED EM PERFIL, ENCASTRÁVEL NO TETO FALSO, EXTERIOR, IP44, 3000K
	INTERRUPTOR SIMPLES DE ENCASTRAR (A=1,10m)
	INTERRUPTOR SIMPLES ESTANQUE DE ENCASTRAR (A=1,10m)
	COMUTADOR DE LUSTRE DE ENCASTRAR (A=1,10m)
	COMUTADOR DE ESCADA DE ENCASTRAR (A=1,10m)
	COMUTADOR DE ESCADA DUPLO DE ENCASTRAR (A=1,10m)
	INVERSOR DE ESCADA SIMPLES DE ENCASTRAR (A=1,10m)
	INTERRUPTOR DE ESTORES DE ENCASTRAR (A=1,10m)
	DETETOR DE MOVIMENTO 360° DE ENCASTRAR
	DETETOR DE MOVIMENTO 180° SALIENTE

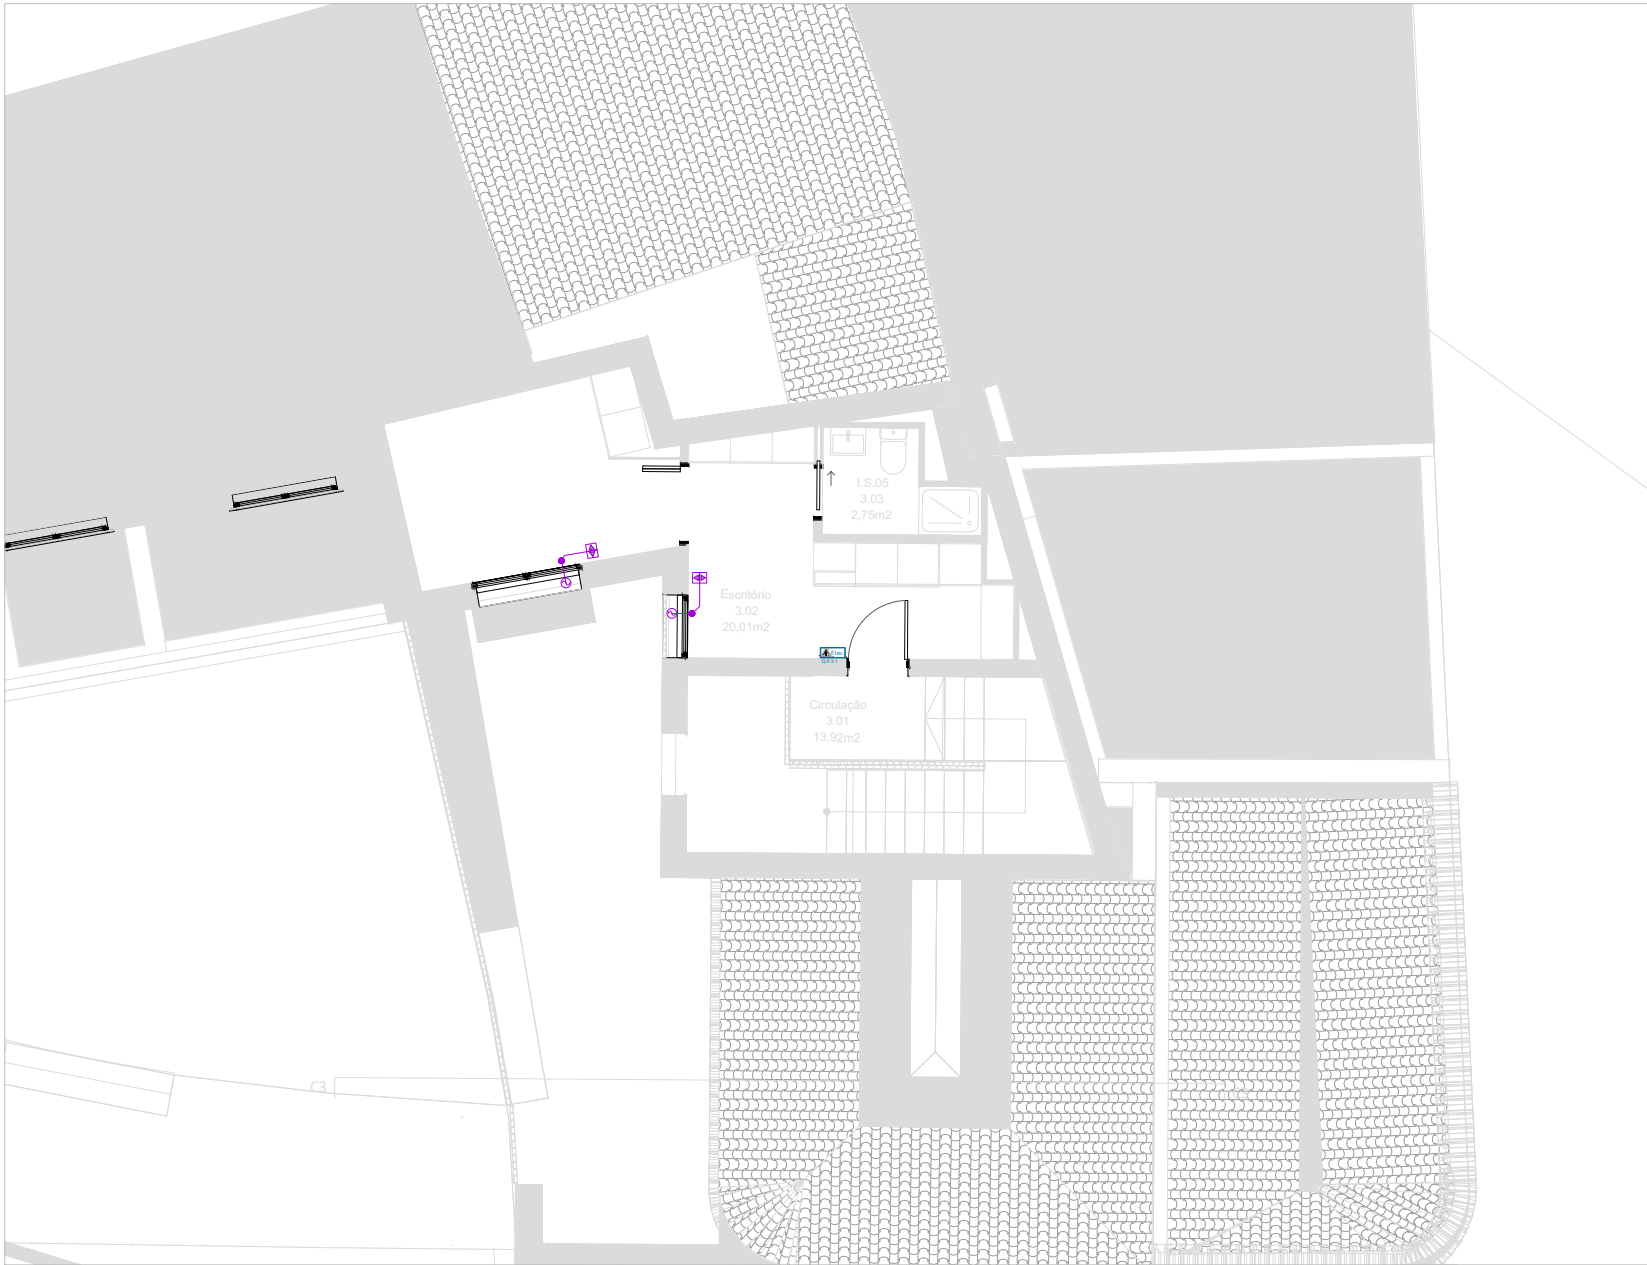

00	Entrega do Projeto de Execução	23.01.2026
Revisão	Descrição	Data

TUU

Requerente

BRUNO EXEMPLADO

Projeto
MBERAL

000 0-0 02 RU A EX EM PL O 5, Nº 31,
COIMBRA

Especialidade
PROJETO DE ELETRICIDADE

PROJETO BASE

Designação
ESTORES
PISO 3

JANEIRO 2026
1:50

EL012

Observações
ESTE PROJETO DEVERÁ SER LIDO EM CONJUNTO COM AS PEÇAS ESCRITAS, ASSIM COMO, O PROJETO DE ARQUITETURA E AS RESTANTES ESPECIALIDADES.
QUAISQUER DISCREPÂNCIAS DEVERÃO SER COMUNICADAS AO PROJETISTA. TODAS AS MEDIDAS DESTES DESENHOS SÃO DE PROJETO E MERAMENTE INDICATIVAS, NECESSITAM SER RETIFICADAS EM OBRA.

Nome Ficheiro
MBERAL_PB_ELE_PD_V00.DWG

Código
24932024

Equipa
EMA GOUVEIA | ENG CIVIL
ANA AGOSTINHO | ENG CIVIL

Reprodução proibida, Dec. Lei 45\85 de 17 de Setembro e código do direito de autor e direitos conexos.

TUU.BUILDING DESIGN MANAGEMENT

arquitetura@tuu.pt www.tuu.pt

LEGENDA:	
	QUADRO ELÉTRICO DO EDIFÍCIO
	TOMADA ELÉTRICA 2P+T, 16A, ENCASTRAR
	TOMADA ELÉTRICA 2P+T, 16A, ENCASTRAR, C/TAMPA IP44
	TOMADA ELÉTRICA 2P+T, 16A, ESTANQUE IP65, ENCASTRAR
	TOMADA ELÉTRICA 2P+T, 16A, ESTANQUE IP65, SALIENTE
	TOMADA DE CHÃO ELETRICIDADE (2 módulos) 1x 2P+T 16A
	ALIMENTAÇÃO ELÉTRICA ESPECÍFICA
	DOWNLIGHT LED COMPACTO DE ENCASTRAR, 2,5W 3000K IP43 Ø27mm
	LUMINÁRIA LED TUBULAR SUSPensa, 4000K, 931mm ou 1493mm
	LUMINÁRIA TIPO RÉGUA SALIENTE, 1030,1530mm ou 2530mm, 3000K
	LUMINÁRIA LINEAR DE ENCASTRAR, 1530mm, 3000K
	CANDEEIRO SUSPENSO, A DEFINIR
	APLIQUE DE PAREDE SALIENTE RETANGULAR, LUZ DESCENDENTE E ASCENDENTE
	Placa Superfície LED Quadrada 18W 225x225 mm; Ref. efectaLED 407
	LUMINÁRIA LED DE ENCASTRAR BALIZADOR, Ø33mm, 2,5W, 3000K, IP65 IK10
	CANDEEIRO LED SUSPENSO, Ø1135mm, 2,5W, 3000K, IP65 IK10
	LUMINÁRIA LED CUBO SALIENTE IP65 3000K EXTERIOR
	Plafon LED 20W PHILIPS CL200; Ref. efectaLED 85955
	LUMINÁRIA LED DE ENCASTRAR, 5W, 3000K, IP65 IK10
	PONTO DE ILUMINAÇÃO EXTERIOR A DEFINIR, JARDIM, IP65<
	PONTO DE ILUMINAÇÃO TETO OU PAREDE - LUMINÁRIA A DEFINIR
	FITA LED EM PERFIL, ENCASTRÁVEL NO TETO FALSO, INTERIOR, 4000K
	FITA LED EM PERFIL, ENCASTRÁVEL NO TETO FALSO, EXTERIOR, IP44, 3000K
	INTERRUPTOR SIMPLES DE ENCASTRAR (A=1,10m)
	INTERRUPTOR SIMPLES ESTANQUE DE ENCASTRAR (A=1,10m)
	COMUTADOR DE LUSTRE DE ENCASTRAR (A=1,10m)
	COMUTADOR DE ESCADA DE ENCASTRAR (A=1,10m)
	COMUTADOR DE ESCADA DUPLO DE ENCASTRAR (A=1,10m)
	INVERSOR DE ESCADA SIMPLES DE ENCASTRAR (A=1,10m)
	INTERRUPTOR DE ESTORES DE ENCASTRAR (A=1,10m)
	DETETOR DE MOVIMENTO 360° DE ENCASTRAR
	DETETOR DE MOVIMENTO 180° SALIENTE



00	Entrega do Projeto de Execução	23.01.2026
Revisão	Descrição	Data

TUU

Requerente
BRUNO EXEMPLADO
Projeto
MBERAL
000 02 COIMBRA, Nº 31,
Rua da Exim, 05
Especialidade
PROJETO DE ELETRICIDADE
PROJETO BASE
Designação
REDE DE TERRAS
PISO 1

JANEIRO 2026
1:50

EL013

Observações
ESTE PROJETO DEVERÁ SER LIDO EM CONJUNTO COM AS PEÇAS ESCRITAS, ASSIM COMO, O PROJETO DE ARQUITETURA E AS RESTANTES ESPECIALIDADES.
QUAISQUER DISCREPÂNCIAS DEVERÃO SER COMUNICADAS AO PROJETISTA. TODAS AS MEDIDAS DESTES DESENHOS SÃO DE PROJETO E MERAMENTE INDICATIVAS, NECESSITAM SER RETIFICADAS EM OBRA.

Nome Ficheiro
MBERAL_PB_ELE_PD_V00.DWG

Código
24932024

Equipa
EMA GOUVEIA | ENG CIVIL
ANA AGOSTINHO | ENG CIVIL

Reprodução proibida, Dec. Lei 45/85 de 17 de Setembro e código do direito de autor e direitos conexos.

TUU.BUILDING DESIGN MANAGEMENT
arquitetura@tuu.pt www.tuu.pt