

00	Entrega do Projeto de Execução	30.06.2026
Revisão	Descrição	Data

TUU

Requerente

BRUNO EXEMPLO

Projeto
MBERAL

Rua Esmeralda, 1000, COIMBRA

Especialidade
PROJETO DE ELETRICIDADE
PROJETO DE EXECUÇÃO

Designação

ÍNDICE

JUNHO 2026
S/ESCALA

EL001

Observações

ESTE PROJETO DEVERÁ SER LIDO EM CONJUNTO COM AS PEÇAS ESCRITAS, ASSIM COMO, O PROJETO DE ARQUITETURA E AS RESTANTES ESPECIALIDADES. QUAISQUER DISCREPÂNCIAS DEVERÃO SER COMUNICADAS AO PROJETISTA. TODAS AS MEDIDAS DESTES DESENHO SÃO DE PROJETO E MERAMENTE INDICATIVAS, NECESSITAM SER RETIFICADAS EM OBRA.

Nome Ficheiro
TUU_MBERAL_PE_ELE_PD_V00.DWG

Código
24932024

Equipa
ENG ELETROTÉCNICO
EMANUEL SILVA | ENG ELETROTÉCNICO

Reprodução proibida, Dec. Lei 45/85 de 17 de DEZEMBRO e código do direito de autor e direitos conexos.

TUU.BUILDING DESIGN MANAGEMENT

arquitetura@tuu.pt www.tuu.pt

	TÍTULO	DATA	REV
EL001	ÍNDICE	06/26	-
EL002	PISO 1 - DISTRIBUIÇÃO DE ENERGIA	06/26	-
EL003	PISO 2 - DISTRIBUIÇÃO DE ENERGIA	06/26	-
EL004	PISO 3 - DISTRIBUIÇÃO DE ENERGIA	06/26	-
EL005	PISO 1 - TOMADAS	06/26	-
EL006	PISO 2 - TOMADAS	06/26	-
EL007	PISO 3 - TOMADAS	06/26	-
EL008	PISO 1 - ILUMINAÇÃO	06/26	-
EL009	PISO 2 - ILUMINAÇÃO	06/26	-
EL010	PISO 3 - ILUMINAÇÃO	06/26	-
EL011	REDE DE TERRAS	06/26	-
EL012	PISO 1 - VÍDEO PORTEIRO	06/26	-
EL013	PISO 2 - VÍDEO PORTEIRO	06/26	-
EL014	PISO 3 - VÍDEO PORTEIRO	06/26	-
EL015	ESQUEMAS QUADROS ELÉTRICOS	06/26	-
EL016	ESQUEMAS QUADROS ELÉTRICOS	06/26	-
EL017	DIAGRAMA DE DISTRIBUIÇÃO QUADROS ELÉTRICOS	06/26	-

00	Entrega do Projeto de Execução	30.06.2026
Revisão	Descrição	Data

TUU

Requerente

BRUNO EXEMPLO

Projeto
MBERAL

Rua Exemplo 03
000000000, COIMBRA

Especialidade
PROJETO DE ELETRICIDADE
PROJETO DE EXECUÇÃO

Designação

DISTRIBUIÇÃO DE ENERGIA
ALIMENTAÇÕES ESPECÍFICAS
CLASSIFICAÇÃO DE LOCAIS
PISO 1

JUNHO 2026
1:100

EL002

Observações

ESTE PROJETO DEVERÁ SER LIDO EM CONJUNTO COM AS PEÇAS
ESCRITAS, ASSIM COMO, O PROJETO DE ARQUITETURA E AS
REstantes ESPECIALIDADES.
QUAISQUER DISCREPÂNCIAS DEVERÃO SER COMUNICADAS AO
PROJETISTA. TODAS AS MEDIDAS DESTES DESENHO SÃO DE
PROJETO E MERAMENTE INDICATIVAS, NECESSITAM SER
RETIFICADAS EM OBRA.

Nome Ficheiro

TUU_MBERAL_PE_ELE_PD_V00.DWG

Código

24932024

Equipa

ENG ELETROTÉCNICO
EMANUEL SILVA | ENG ELETROTÉCNICO

Reprodução proibida, Dec. Lei 45/85 de 17 de
DEZEMBRO e código do direito de autor e
direitos conexos.

TUU.BUILDING DESIGN MANAGEMENT

arquitetura@tuu.pt

www.tuu.pt

LEGENDA:

	QUADRO ELÉTRICO DO EDIFÍCIO
	TOMADA ELÉTRICA 2P+T, 16A, ENCASTRAR
	TOMADA ELÉTRICA 2P+T, 16A, ENCASTRAR, C/TAMPA IP44
	TOMADA ELÉTRICA 2P+T, 16A, ESTANQUE IP65, ENCASTRAR
	TOMADA ELÉTRICA 2P+T, 16A, ESTANQUE IP65, SALIENTE
	TOMADA DE CHÃO ELETRICIDADE (2 módulos) 1x 2P+T 16A
	ALIMENTAÇÃO ELÉTRICA ESPECÍFICA
	DOWLIGHT LED COMPACTO DE ENCASTRAR, 2,5W 3000K IP43 Ø27mm
	APLIQUE DE PAREDE SALIENTE RETANGULAR, LUZ DESCENDENTE E ASCENDENTE
	Placa Superfície LED Quadrada 18W 225x225 mm; Ref. efectLED 407
	LUMINÁRIA LED DE ENCASTRAR BALIZADOR, Ø33mm, 2,5W, 3000K, IP65 IK10
	Plafon LED 20W PHILIPS CL200; Ref. efectLED 85955
	LUMINÁRIA LED DE ENCASTRAR, 5W, 3000K, IP65 IK10
	INTERRUPTOR SIMPLES DE ENCASTRAR (A=1,10m)
	COMUTADOR DE ESCADA DE ENCASTRAR (A=1,10m)
	DETETOR DE MOVIMENTO 360° DE ENCASTRAR
	DETETOR DE MOVIMENTO 180° SALIENTE
	BOTÃO DE PRESSÃO DE ENCASTRAR (A=1,10m)
	BLOCO DE ILUMINAÇÃO DE SEGURANÇA, >1h, 100lm, IP42/65

LEGENDA VIDEOPORTEIRO

	BOTONEIRA VP EXTERIOR
	TRINCO ELÉTRICO
	MONITOR VP INTERIOR
	ALIMENTADOR VP



Classificação dos Locais Quanto ao Ambiente

Designação	Classificação	Locais	Índice de Proteção
A1	AA4 + AD1 + AE1 + BA1 + BC1 + BD1 + XX1	Circulações, Quartos, Salas e Cozinha (Zona Geral)	IP20 - IK04
A2	AA4 + AD2 + AE1 + BA1 + BC1 + BD1 + XX1	Cozinha (Zona da Banca - Raio 0.6cm)	IP44 - IK04
A3	Volume 3 - AA4+AB4+AD2+BB2+BC3+XX1	Instalações Sanitárias	IP21 - IK04
	Volume 2 - AA4+AB4+AD3+BB3+BC3+XX1		IP24 - IK04
	Volume 1 - AA4+AB4+AD4+BB3+BC3+XX1		IP25 - IK04
	Volume 0 - AA4+AB4+AD7+BB3+BC3+XX1		IP27 - IK04
A4	AA8 + AB8 + AD4 + AN3 + BC2 + XX1	Zonas Exterior	IP44 - IK04

00	Entrega do Projeto de Execução	30.06.2026
Revisão	Descrição	Data

TUU

Requerente

BRUNO
O EXEMPLO

Projeto
MBERAL

Rua
Exemplo
03
000 0-00 2, COIMBRA

Especialidade
PROJETO DE ELETRICIDADE
PROJETO DE EXECUÇÃO

Designação

DISTRIBUIÇÃO DE ENERGIA
ALIMENTAÇÕES ESPECÍFICAS
CLASSIFICAÇÃO DE LOCAIS
PISO 2

JUNHO 2026
1:100

EL003

Observações

ESTE PROJETO DEVERÁ SER LIDO EM CONJUNTO COM AS PEÇAS
ESCRITAS, ASSIM COMO, O PROJETO DE ARQUITETURA E AS
REMANESCENTES ESPECIALIDADES.
QUAISQUER DISCREPÂNCIAS DEVERÃO SER COMUNICADAS AO
PROJETISTA. TODAS AS MEDIDAS DESTES DESENHOS SÃO DE
PROJETO E MERAMENTE INDICATIVAS, NECESSITAM SER
RETIFICADAS EM OBRA.

Nome Ficheiro

TUU_MBERAL_PE_ELE_PD_V00.DWG

Código

24932024

Equipa


MANUEL SILVA | ENG ELETROTÉCNICO
EMANUEL SILVA | ENG ELETROTÉCNICO

Reprodução proibida, Dec. Lei 45/85 de 17 de
DEZEMBRO e código do direito de autor e
direitos conexos.

TUU.BUILDING DESIGN MANAGEMENT

arquitetura@tuu.pt

www.tuu.pt

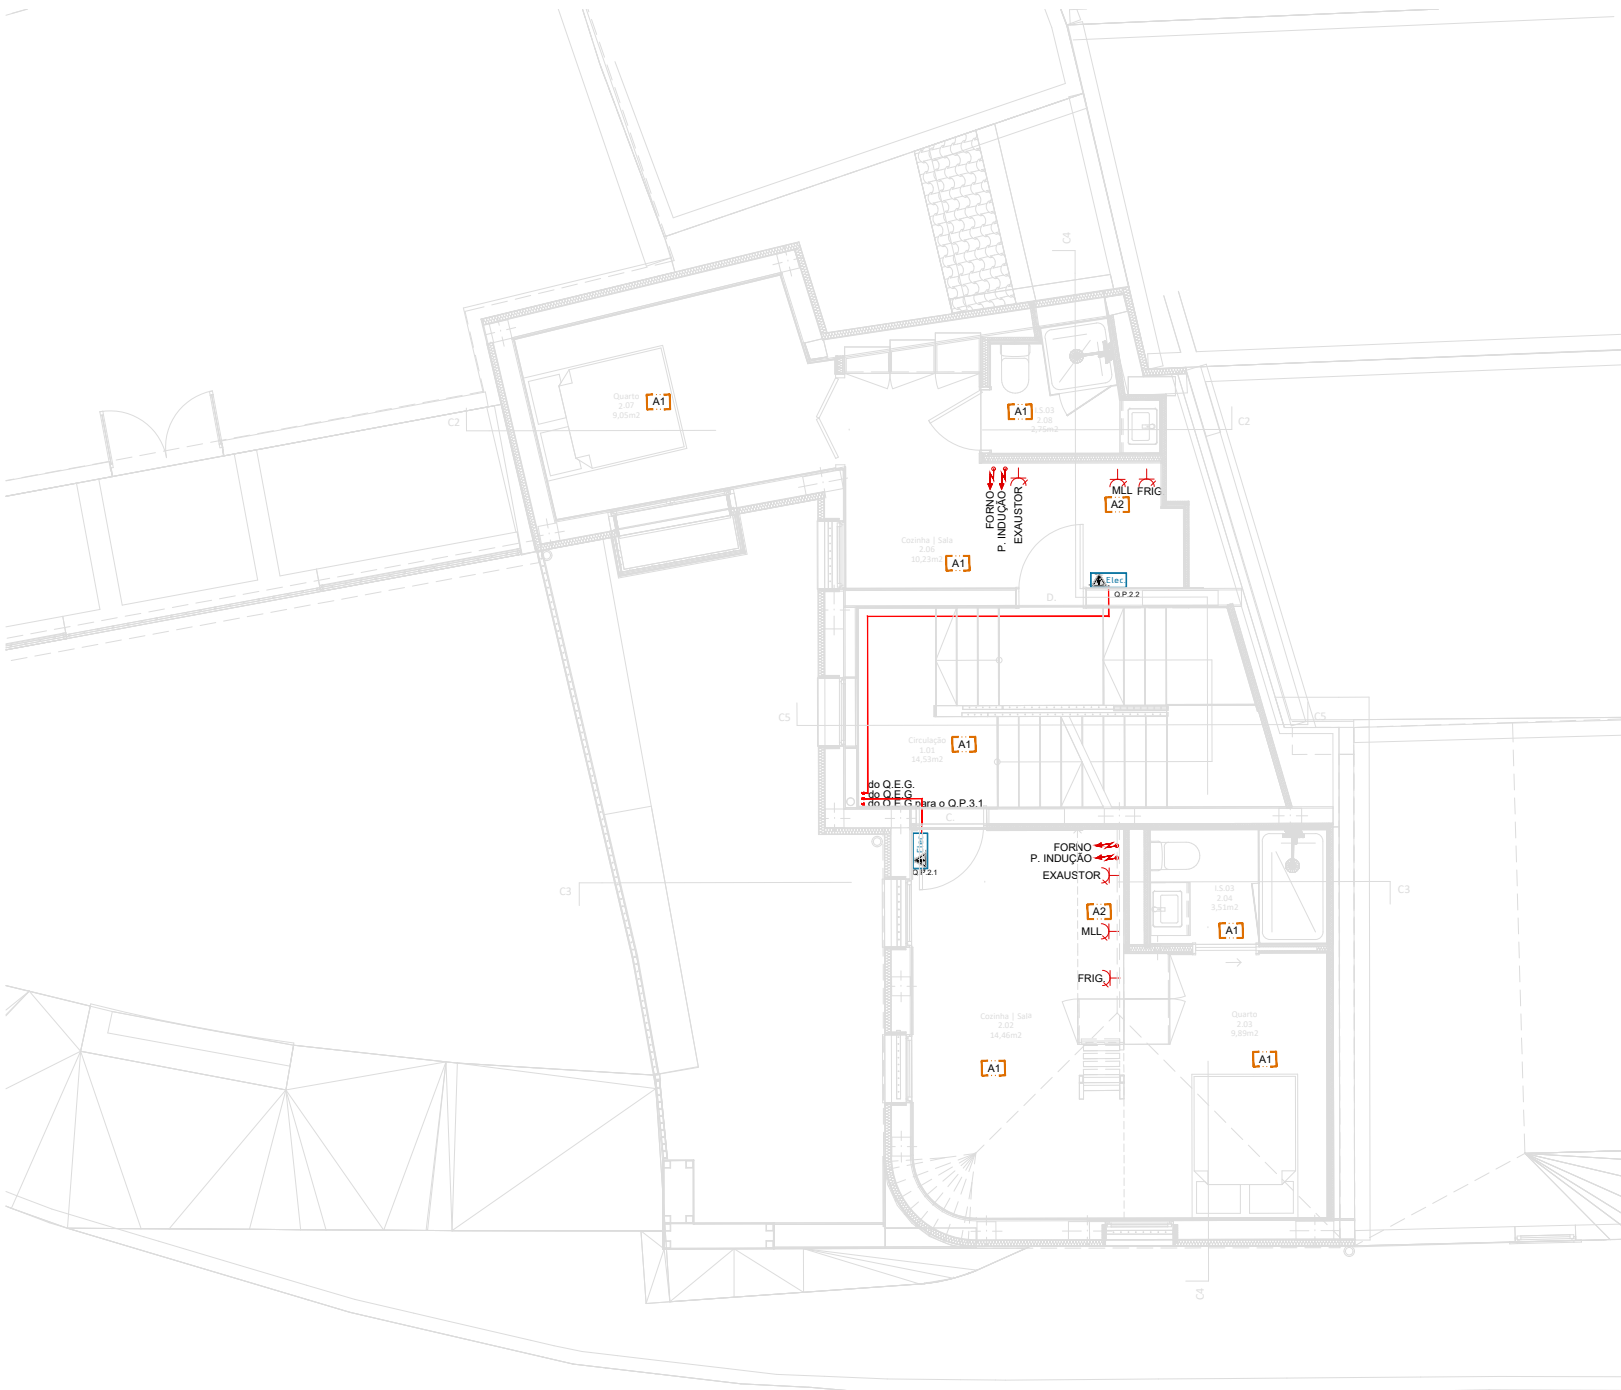

LEGENDA:

	QUADRO ELÉTRICO DO EDIFÍCIO
	TOMADA ELÉTRICA 2P+T, 16A, ENCASTRAR
	TOMADA ELÉTRICA 2P+T, 16A, ENCASTRAR, C/TAMPA IP44
	TOMADA ELÉTRICA 2P+T, 16A, ESTANQUE IP65, ENCASTRAR
	TOMADA ELÉTRICA 2P+T, 16A, ESTANQUE IP65, SALIENTE
	TOMADA DE CHÃO ELETRICIDADE (2 módulos) 1x 2P+T 16A
	ALIMENTAÇÃO ELÉTRICA ESPECÍFICA
	DOWNLIGHT LED COMPACTO DE ENCASTRAR, 2.5W 3000K IP43 Ø27mm
	APLIQUE DE PAREDE SALIENTE RETANGULAR, LUZ DESCENDENTE E ASCENDENTE
	Placa Superfície LED Quadrada 18W 225x225 mm; Ref. efectoLED 407
	LUMINÁRIA LED DE ENCASTRAR BALIZADOR, Ø33mm, 2.5W, 3000K, IP65 IK10
	Piafon LED 20W PHILIPS CL200; Ref. efectoLED 85955
	LUMINÁRIA LED DE ENCASTRAR, 5W, 3000K, IP65 IK10
	INTERRUPTOR SIMPLES DE ENCASTRAR (A=1,10m)
	COMUTADOR DE ESCADA DE ENCASTRAR (A=1,10m)
	DETETOR DE MOVIMENTO 360° DE ENCASTRAR
	DETETOR DE MOVIMENTO 180° SALIENTE
	BOTÃO DE PRESSÃO DE ENCASTRAR (A=1,10m)
	BLOCO DE ILUMINAÇÃO DE SEGURANÇA, >1h, 100lm, IP42/65

LEGENDA VIDEOPORTEIRO

	BOTONEIRA VP EXTERIOR
	TRINCO ELÉTRICO
	MONITOR VP INTERIOR
	ALIMENTADOR VP

Classificação dos Locais Quanto ao Ambiente

Designação	Classificação	Locais	Índice de Proteção
A1	AA4 + AD1 + AE1 + BA1 + BC1 + BD1 + XX1	Circulações, Quartos, Salas e Cozinha (Zona Geral)	IP20 - IK04
A2	AA4 + AD2 + AE1 + BA1 + BC1 + BD1 + XX1	Cozinha (Zona da Banca - Raio 0.6cm)	IP44 - IK04
A3	Volume 3 - AA4+AB4+AD2+BB2+BC3+XX1	Instalações Sanitárias	IP21 - IK04
	Volume 2 - AA4+AB4+AD3+BB3+BC3+XX1		IP24 - IK04
	Volume 1 - AA4+AB4+AD4+BB3+BC3+XX1		IP25 - IK04
	Volume 0 - AA4+AB4+AD7+BB3+BC3+XX1		IP27 - IK04
A4	AA8 + AB8 + AD4 + AN3 + BC2 + XX1	Zonas Exterior	IP44 - IK04

TUW

BRUN
O
EXEM
PLO

000
0-00
2 , COIMBRA

Designação

JUNHO 2026
1:100

EL004


Nome Ficheiro
TUU_MBERAL_PE_ELE_PD_V00.DWG

Equipa

ANEXO EM PL O | ENG ELETROTÉCNICO
EMANUEL SILVA | ENG ELETROTÉCNICO

Reprodução proibida, Dec. Lei 45\85 de 17 de
DEZEMBRO e código do direito de autor e
direitos conexos.

arquitetura@tuu.pt www.tuu.pt

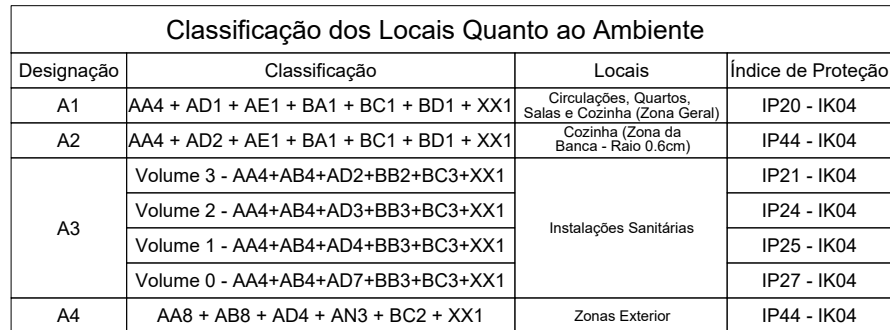

	QUADRO ELÉTRICO DO EDIFÍCIO
	TOMADA ELÉTRICA 2P+T, 16A, ENCASTRAR
	TOMADA ELÉTRICA 2P+T, 16A, ENCASTRAR, C/TAMPA IP44
	TOMADA ELÉTRICA 2P+T, 16A, ESTANQUE IP65, ENCASTRAR
	TOMADA ELÉTRICA 2P+T, 16A, ESTANQUE IP65, SALIENTE
	TOMADA DE CHÃO ELETRICIDADE (2 módulos) 1x 2P+T 16A
	ALIMENTAÇÃO ELÉTRICA ESPECÍFICA
	DOWNLIGHT LED COMPACTO DE ENCASTRAR, 2,5W 3000K IP43 Ø27mm
	APLIQUE DE PAREDE SALIENTE RETANGULAR, LUZ DESCENDENTE E ASCENDENTE
	Placa Superfície LED Quadrada 18W 225x225 mm, Ref. efectoLED 407
	LUMINÁRIA LED DE ENCASTRAR BALIZADOR, Ø33mm, 2,5W, 3000K, IP65 IK10
	Plafon LED 20W PHILIPS CL200, Ref. efectoLED 85955
	LUMINÁRIA LED DE ENCASTRAR, 5W, 3000K, IP65 IK10
	INTERRUPTOR SIMPLES DE ENCASTRAR (A=1,10m)
	COMUTADOR DE ESCADA DE ENCASTRAR (A=1,10m)
	DETETOR DE MOVIMENTO 360° DE ENCASTRAR
	DETETOR DE MOVIMENTO 180° SALIENTE
	BOTÃO DE PRESSÃO DE ENCASTRAR (A=1,10m)
	BLOCO DE ILUMINAÇÃO DE SEGURANÇA, >1h, 100lm, IP42/65

 Botoneira VP	BOTONEIRA VP EXTERIOR
	TRINCO ELÉTRICO
VP	MONITOR VP INTERIOR
	ALIMENTADOR VP

00	Entrega do Projeto de Execução	30.06.2026
Revisão	Descrição	Data

TUW

Requerente

BRUN
O
EXEM
PLO

Projeto
MBERAL

000
0-00
2
, COIMBRA

Especialidade
PROJETO DE ELETRICIDADE
PROJETO DE EXECUÇÃO

Designação

TOMADAS DE USO GERAL
PISO 1

JUNHO 2026
1:100

EL005

Observações

ESTE PROJETO DEVERÁ SER LIDO EM CONJUNTO COM AS PEÇAS
ESCRITAS, ASSIM COMO, O PROJETO DE ARQUITETURA E AS
RENTANTES ESPECIALIDADES.
QUAISQUER DISCREPÂNCIAS DEVERÃO SER COMUNICADAS AO
PROJETISTA. TODAS AS MEDIDAS DESTES DESENHOS SÃO DE
PROJETO E MERAMENTE INDICATIVAS, NECESSITAM SER
RETIIFICADAS EM OBRA.

Nome Ficheiro

TUU_MBERAL_PE_ELE_PD_V00.DWG

Código

24932024

Equipa

ANEXO | ENG ELETROTÉCNICO
EMANUEL SILVA | ENG ELETROTÉCNICO

Reprodução proibida, Dec. Lei 45\85 de 17 de DEZEMBRO e código do direito de autor e direitos conexos.

TUU.BUILDING DESIGN MANAGEMENT

arquitetura@tuu.pt

www.tuu.pt

LEGENDA:

	QUADRO ELÉTRICO DO EDIFÍCIO
	TOMADA ELÉTRICA 2P+T, 16A, ENCASTRAR
	TOMADA ELÉTRICA 2P+T, 16A, ENCASTRAR, C/TAMPA IP44
	TOMADA ELÉTRICA 2P+T, 16A, ESTANQUE IP65, ENCASTRAR
	TOMADA ELÉTRICA 2P+T, 16A, ESTANQUE IP65, SALIENTE
	TOMADA DE CHÃO ELETTRICIDADE (2 módulos) 1x 2P+T 16A
	ALIMENTAÇÃO ELÉTRICA ESPECÍFICA
	L1 DOWNLIGHT LED COMPACTO DE ENCASTRAR, 2.5W 3000K IP43 Ø27mm
	L7 APLIQUE DE PAREDE SALIENTE RETANGULAR, LUZ DESCENDENTE E ASCENDENTE
	L8 Placa Superfície LED Quadrada 18W 225x225 mm; Ref. efectoLED 407
	L9 LUMINÁRIA LED DE ENCASTRAR BALIZADOR, Ø33mm, 2,5W, 3000K, IP65 IK10
	L14 Plafon LED 20W PHILIPS CL200; Ref. efectoLED 85955
	L15 LUMINÁRIA LED DE ENCASTRAR, 5W, 3000K, IP65 IK10
	INTERRUPTOR SIMPLES DE ENCASTRAR (A=1,10m)
	COMUTADOR DE ESCADA DE ENCASTRAR (A=1,10m)
	DETETOR DE MOVIMENTO 360° DE ENCASTRAR
	DETETOR DE MOVIMENTO 180° SALIENTE
	BOTÃO DE PRESSÃO DE ENCASTRAR (A=1,10m)
	
	BLOCO DE ILUMINAÇÃO DE SEGURANÇA, >1h, 100lm, IP42/65

LEGENDA VIDEOPORTEIRO

	BOTONEIRA VP EXTERIOR
	TRINCO ELÉTRICO
 VP	MONITOR VP INTERIOR
	ALIMENTADOR VP

00	Entrega do Projeto de Execução	30.06.2026
Revisão	Descrição	Data

TUU

Requerente

BRUNO
O EXEMPLO

Projeto
MBERAL

Rua
Exemplar
03
000 0-00 2, COIMBRA

Especialidade
PROJETO DE ELETRICIDADE
PROJETO DE EXECUÇÃO

Designação

TOMADAS DE USO GERAL
PISO 2

JUNHO 2026
1:100

EL006

Observações
ESTE PROJETO DEVERÁ SER LIDO EM CONJUNTO COM AS PEÇAS
ESCRITAS, ASSIM COMO, O PROJETO DE ARQUITETURA E AS
REstantes ESPECIALIDADES.
QUAISQUER DISCREPÂNCIAS DEVERÃO SER COMUNICADAS AO
PROJETISTA. TODAS AS MEDIDAS DESTES DESENHOS SÃO DE
PROJETO E MERAMENTE INDICATIVAS, NECESSITAM SER
RETIFICADAS EM OBRA.

Nome Ficheiro
TUU_MBERAL_PE_ELE_PD_V00.DWG


Código
24932024

Equipa
MANUEL SILVA | ENG ELETROTÉCNICO
EMANUEL SILVA | ENG ELETROTÉCNICO

Reprodução proibida, Dec. Lei 45/85 de 17 de
DEZEMBRO e código do direito de autor e
direitos conexos.

TUU.BUILDING DESIGN MANAGEMENT

arquitetura@tuu.pt www.tuu.pt

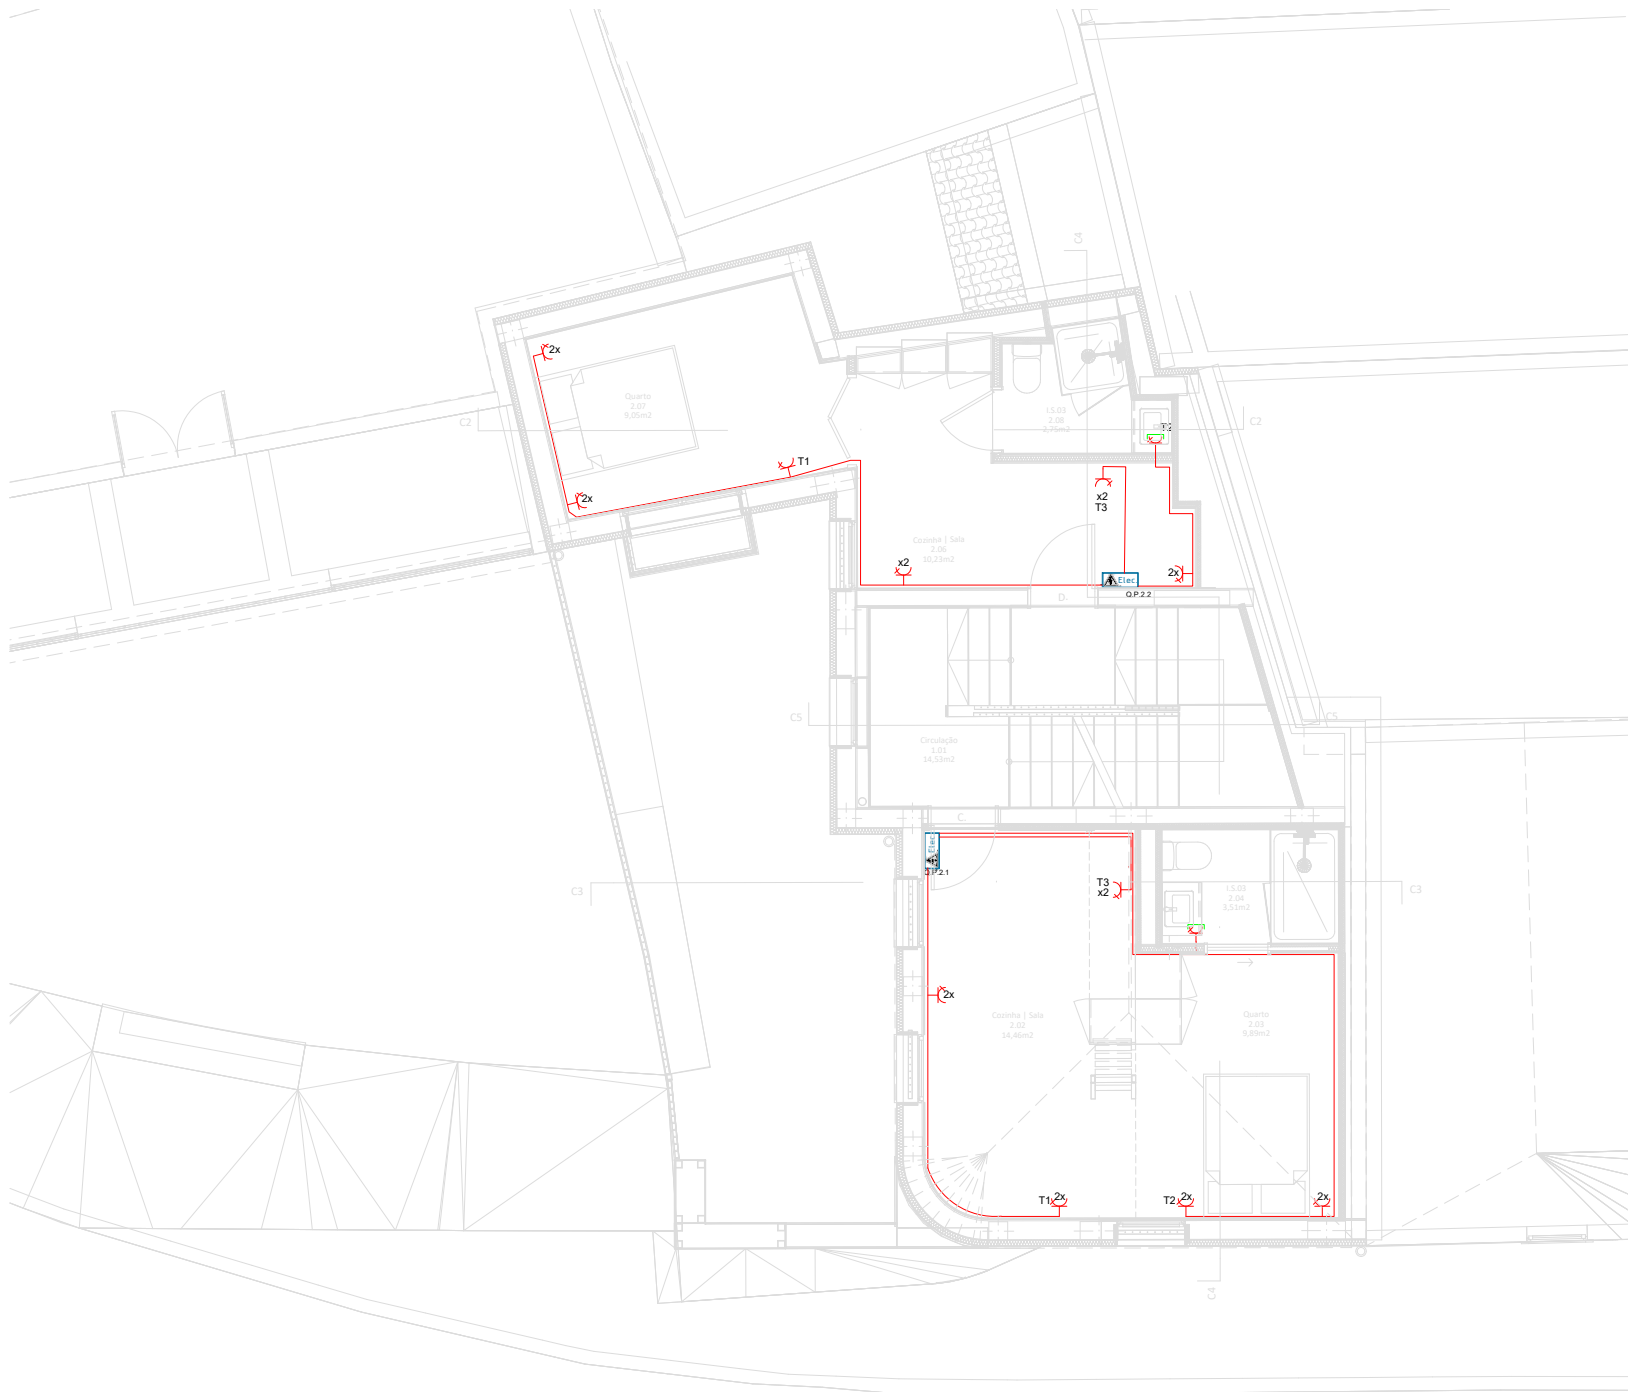

LEGENDA:

	QUADRO ELÉTRICO DO EDIFÍCIO
	TOMADA ELÉTRICA 2P+T, 16A, ENCASTRAR
	TOMADA ELÉTRICA 2P+T, 16A, ENCASTRAR, C/TAMPA IP44
	TOMADA ELÉTRICA 2P+T, 16A, ESTANQUE IP65, ENCASTRAR
	TOMADA ELÉTRICA 2P+T, 16A, ESTANQUE IP65, SALIENTE
	TOMADA DE CHÃO ELETRICIDADE (2 módulos) 1x 2P+T 16A
	ALIMENTAÇÃO ELÉTRICA ESPECÍFICA
	DOWNLIGHT LED COMPACTO DE ENCASTRAR, 2,5W 3000K IP43 Ø27mm
	APLIQUE DE PAREDE SALIENTE RETANGULAR, LUZ DESCENDENTE E ASCENDENTE
	Placa Superfície LED Quadrada 18W 225x225 mm; Ref. efectLED 407
	LUMINÁRIA LED DE ENCASTRAR BALIZADOR, Ø33mm, 2,5W, 3000K, IP65 IK10
	Plafon LED 20W PHILIPS CL200; Ref. efectLED 85955
	LUMINÁRIA LED DE ENCASTRAR, 5W, 3000K, IP65 IK10
	INTERRUPTOR SIMPLES DE ENCASTRAR (A=1,10m)
	COMUTADOR DE ESCADA DE ENCASTRAR (A=1,10m)
	DETETOR DE MOVIMENTO 360° DE ENCASTRAR
	DETETOR DE MOVIMENTO 180° SALIENTE
	BOTÃO DE PRESSÃO DE ENCASTRAR (A=1,10m)
	BLOCO DE ILUMINAÇÃO DE SEGURANÇA, >1h, 100lm, IP42/65

LEGENDA VIDEOPORTEIRO

	BOTONEIRA VP EXTERIOR
	TRINCO ELÉTRICO
	MONITOR VP INTERIOR
	ALIMENTADOR VP

00	Entrega do Projeto de Execução	30.06.2026
Revisão	Descrição	Data

TUU

Requerente

BRUNO EXEMPLO

Projeto
MBERAL

000 0-00 2 , COIMBRA
Rua
Esq
mg
03

Especialidade
PROJETO DE ELETRICIDADE
PROJETO DE EXECUÇÃO

Designação

TOMADAS DE USO GERAL
PISO 3

JUNHO 2026
1:100

EL007

Observações

ESTE PROJETO DEVERÁ SER LIDO EM CONJUNTO COM AS PEÇAS
ESCRITAS, ASSIM COMO, O PROJETO DE ARQUITETURA E AS
REstantes ESPECIALIDADES.
QUAISQUER DISCREPÂNCIAS DEVERÃO SER COMUNICADAS AO
PROJETISTA. TODAS AS MEDIDAS DESTES DESENHO SÃO DE
PROJETO E MERAMENTE INDICATIVAS, NECESSITAM SER
RETIFICADAS EM OBRA.

Nome Ficheiro

TUU_MBERAL_PE_ELE_PD_V00.DWG

Código

24932024

Equipa


🇧🇷 🇵🇹 🇵🇸 🇵🇸 🇵🇸 🇵🇸 | ENG ELETROTÉCNICO
EMANUEL SILVA | ENG ELETROTÉCNICO

Reprodução proibida, Dec. Lei 45/85 de 17 de
DEZEMBRO e código do direito de autor e
direitos conexos.

TUU.BUILDING DESIGN MANAGEMENT

arquitetura@tuu.pt

www.tuu.pt

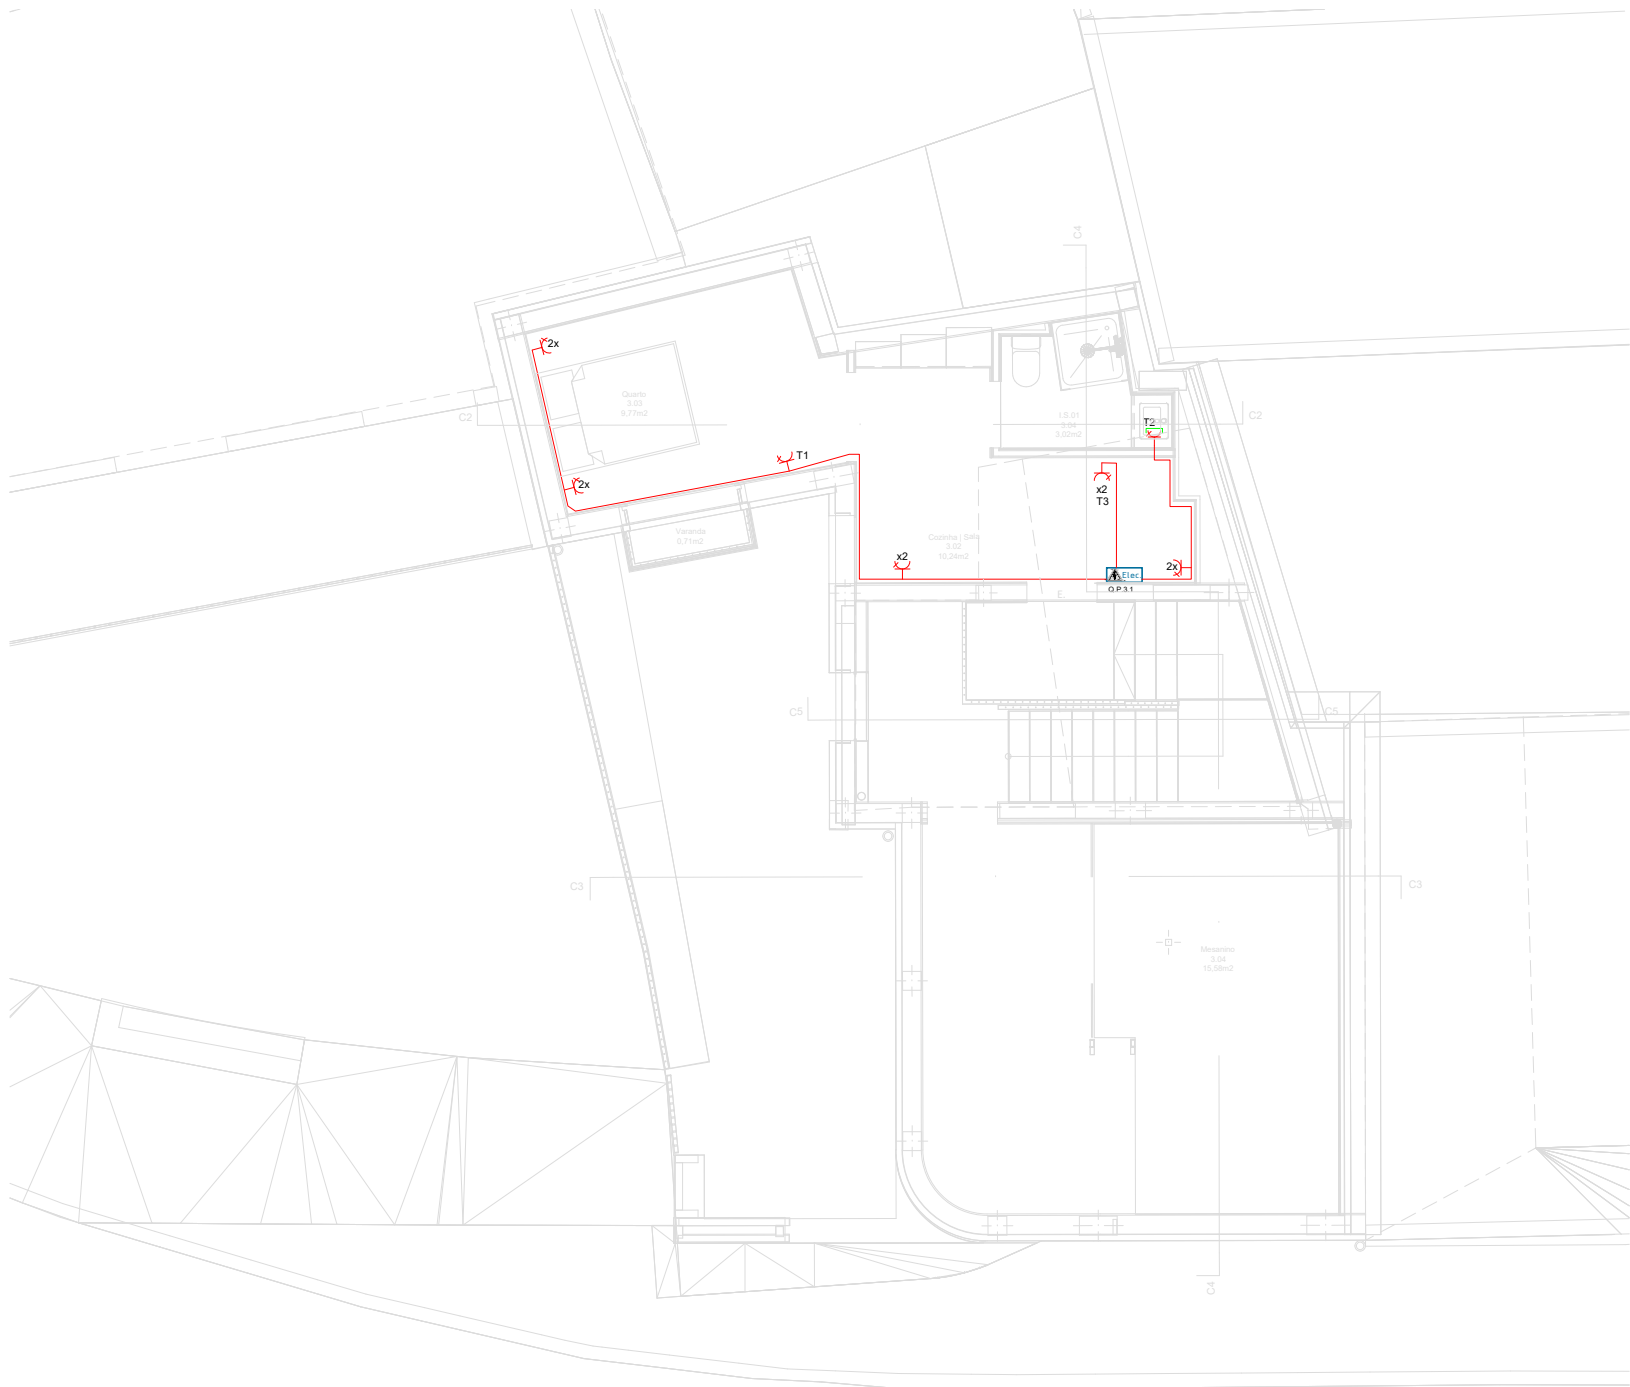

LEGENDA:

	QUADRO ELÉTRICO DO EDIFÍCIO
	TOMADA ELÉTRICA 2P+T, 16A, ENCASTRAR
	TOMADA ELÉTRICA 2P+T, 16A, ENCASTRAR, C/TAMPA IP44
	TOMADA ELÉTRICA 2P+T, 16A, ESTANQUE IP65, ENCASTRAR
	TOMADA ELÉTRICA 2P+T, 16A, ESTANQUE IP65, SALIENTE
	TOMADA DE CHÃO ELETRICIDADE (2 módulos) 1x 2P+T 16A
	ALIMENTAÇÃO ELÉTRICA ESPECÍFICA
	DOWNLIGHT LED COMPACTO DE ENCASTRAR, 2,5W 3000K IP43 Ø27mm
	APLIQUE DE PAREDE SALIENTE RETANGULAR, LUZ DESCENDENTE E ASCENDENTE
	Placa Superfície LED Quadrada 18W 225x225 mm; Ref. efectLED 407
	LUMINÁRIA LED DE ENCASTRAR BALIZADOR, Ø33mm, 2,5W, 3000K, IP65 IK10
	Plafon LED 20W PHILIPS CL200; Ref. efectLED 85955
	LUMINÁRIA LED DE ENCASTRAR, 5W, 3000K, IP65 IK10
	INTERRUPTOR SIMPLES DE ENCASTRAR (A=1,10m)
	COMUTADOR DE ESCADA DE ENCASTRAR (A=1,10m)
	DETETOR DE MOVIMENTO 360° DE ENCASTRAR
	DETETOR DE MOVIMENTO 180° SALIENTE
	BOTÃO DE PRESSÃO DE ENCASTRAR (A=1,10m)
	BLOCO DE ILUMINAÇÃO DE SEGURANÇA, >1h, 100lm, IP42/65

LEGENDA VIDEOPORTEIRO

	BOTONEIRA VP EXTERIOR
	TRINCO ELÉTRICO
	MONITOR VP INTERIOR
	ALIMENTADOR VP

00	Entrega do Projeto de Execução	30.06.2026
Revisão	Descrição	Data

TUU

Requerente

BRUNO
O EXEMPLO

Projeto
MBERAL

Rua
Ese
mp
03
000 0-00 2 , COIMBRA

Especialidade
PROJETO DE ELETRICIDADE
PROJETO DE EXECUÇÃO

Designação

ILUMINAÇÃO
PISO 1

JUNHO 2026
1:100

EL008

Observações

ESTE PROJETO DEVERÁ SER LIDO EM CONJUNTO COM AS PEÇAS
ESCRITAS, ASSIM COMO, O PROJETO DE ARQUITETURA E AS
REstantes ESPECIALIDADES.
QUAISQUER DISCREPÂNCIAS DEVERÃO SER COMUNICADAS AO
PROJETISTA. TODAS AS MEDIDAS DESTES DESENHO SÃO DE
PROJETO E MERAMENTE INDICATIVAS, NECESSITAM SER
RETIFICADAS EM OBRA.

Nome Ficheiro

TUU_MBERAL_PE_ELE_PD_V00.DWG

Código

24932024

Equipa

ENG ELETROTÉCNICO
EMANUEL SILVA | ENG ELETROTÉCNICO

Reprodução proibida, Dec. Lei 45/85 de 17 de
DEZEMBRO e código do direito de autor e
direitos conexos.

TUU.BUILDING DESIGN MANAGEMENT

arquitetura@tuu.pt

www.tuu.pt

LEGENDA:

	QUADRO ELÉTRICO DO EDIFÍCIO
	TOMADA ELÉTRICA 2P+T, 16A, ENCASTRAR
	TOMADA ELÉTRICA 2P+T, 16A, ENCASTRAR, C/TAMPA IP44
	TOMADA ELÉTRICA 2P+T, 16A, ESTANQUE IP65, ENCASTRAR
	TOMADA ELÉTRICA 2P+T, 16A, ESTANQUE IP65, SALIENTE
	TOMADA DE CHÃO ELETRICIDADE (2 módulos) 1x 2P+T 16A
	ALIMENTAÇÃO ELÉTRICA ESPECÍFICA
	DOWNLIGHT LED COMPACTO DE ENCASTRAR, 2,5W 3000K IP43 Ø27mm
	APLIQUE DE PAREDE SALIENTE RETANGULAR, LUZ DESCENDENTE E ASCENDENTE
	Placa Superfície LED Quadrada 18W 225x225 mm; Ref. efectLED 407
	LUMINÁRIA LED DE ENCASTRAR BALIZADOR, Ø33mm, 2,5W, 3000K, IP65 IK10
	Plafon LED 20W PHILIPS CL200; Ref. efectLED 85955
	LUMINÁRIA LED DE ENCASTRAR, 5W, 3000K, IP65 IK10
	INTERRUPTOR SIMPLES DE ENCASTRAR (A=1,10m)
	COMUTADOR DE ESCADA DE ENCASTRAR (A=1,10m)
	DETETOR DE MOVIMENTO 360° DE ENCASTRAR
	DETETOR DE MOVIMENTO 180° SALIENTE
	BOTÃO DE PRESSÃO DE ENCASTRAR (A=1,10m)
	BLOCO DE ILUMINAÇÃO DE SEGURANÇA, >1h, 100lm, IP42/65

LEGENDA VIDEOPORTEIRO

	BOTONEIRA VP EXTERIOR
	TRINCO ELÉTRICO
	MONITOR VP INTERIOR
	ALIMENTADOR VP

*AL - Alimentação do Bloco Autónomo feita a partir do circuito de iluminação local



00	Entrega do Projeto de Execução	30.06.2026
Revisão	Descrição	Data

TUU

Requerente

BRUNO
O EXEMPLO

Projeto
MBERAL

000 0-00 2 , COIMBRA
Rua
Ese
mg
03

Especialidade
PROJETO DE ELETRICIDADE
PROJETO DE EXECUÇÃO

Designação

ILUMINAÇÃO
PISO 2

JUNHO 2026
1:100

EL009

Observações

ESTE PROJETO DEVERÁ SER LIDO EM CONJUNTO COM AS PEÇAS
ESCRITAS, ASSIM COMO, O PROJETO DE ARQUITETURA E AS
REstantes ESPECIALIDADES.
QUAISQUER DISCREPÂNCIAS DEVERÃO SER COMUNICADAS AO
PROJETISTA. TODAS AS MEDIDAS DESTES DESENHOS SÃO DE
PROJETO E MERAMENTE INDICATIVAS, NECESSITAM SER
RETIFICADAS EM OBRA.

Nome Ficheiro

TUU_MBERAL_PE_ELE_PD_V00.DWG

Código

24932024

Equipa

ENG ELETROTÉCNICO
EMANUEL SILVA | ENG ELETROTÉCNICO

Reprodução proibida, Dec. Lei 45/85 de 17 de
DEZEMBRO e código do direito de autor e
direitos conexos.

TUU.BUILDING DESIGN MANAGEMENT

arquitetura@tuu.pt

www.tuu.pt



LEGENDA:

	QUADRO ELÉTRICO DO EDIFÍCIO
	TOMADA ELÉTRICA 2P+T, 16A, ENCASTRAR
	TOMADA ELÉTRICA 2P+T, 16A, ENCASTRAR, C/TAMPA IP44
	TOMADA ELÉTRICA 2P+T, 16A, ESTANQUE IP65, ENCASTRAR
	TOMADA ELÉTRICA 2P+T, 16A, ESTANQUE IP65, SALIENTE
	TOMADA DE CHÃO ELETRICIDADE (2 módulos) 1x 2P+T 16A
	ALIMENTAÇÃO ELÉTRICA ESPECÍFICA
	DOWNLIGHT LED COMPACTO DE ENCASTRAR, 2,5W 3000K IP43 Ø27mm
	APLIQUE DE PAREDE SALIENTE RETANGULAR, LUZ DESCENDENTE E ASCENDENTE
	Placa Superfície LED Quadrada 18W 225x225 mm; Ref. efectLED 407
	LUMINÁRIA LED DE ENCASTRAR BALIZADOR, Ø33mm, 2,5W, 3000K, IP65 IK10
	Plafon LED 20W PHILIPS CL200; Ref. efectLED 85955
	LUMINÁRIA LED DE ENCASTRAR, 5W, 3000K, IP65 IK10
	INTERRUPTOR SIMPLES DE ENCASTRAR (A=1,10m)
	COMUTADOR DE ESCADA DE ENCASTRAR (A=1,10m)
	DETETOR DE MOVIMENTO 360° DE ENCASTRAR
	DETETOR DE MOVIMENTO 180° SALIENTE
	BOTÃO DE PRESSÃO DE ENCASTRAR (A=1,10m)
	BLOCO DE ILUMINAÇÃO DE SEGURANÇA, >1h, 100lm, IP42/65

LEGENDA VIDEOPORTEIRO

	BOTONEIRA VP EXTERIOR
	TRINCO ELÉTRICO
	MONITOR VP INTERIOR
	ALIMENTADOR VP

*AL - Alimentação do Bloco Autónomo feita a partir do circuito de iluminação local

00	Entrega do Projeto de Execução	30.06.2026
Revisão	Descrição	Data

TUU

Requerente

BRUNO
O EXEMPLO

Projeto
MBERAL

000 0-00 2 , COIMBRA
Rua
Ese
mp
03

Especialidade
PROJETO DE ELETRICIDADE
PROJETO DE EXECUÇÃO

Designação

ILUMINAÇÃO
PISO 3

JUNHO 2026
1:100

EL010

Observações

ESTE PROJETO DEVERÁ SER LIDO EM CONJUNTO COM AS PEÇAS
ESCRITAS, ASSIM COMO, O PROJETO DE ARQUITETURA E AS
RESTANTES ESPECIALIDADES.
QUAISQUER DISCREPÂNCIAS DEVERÃO SER COMUNICADAS AO
PROJETISTA. TODAS AS MEDIDAS DESTES DESENHOS SÃO DE
PROJETO E MERAMENTE INDICATIVAS, NECESSITAM SER
RETIFICADAS EM OBRA.

Nome Ficheiro

TUU_MBERAL_PE_ELE_PD_V00.DWG

Código

24932024

Equipa

ENG ELETROTÉCNICO
EMANUEL SILVA | ENG ELETROTÉCNICO

Reprodução proibida, Dec. Lei 45/85 de 17 de
DEZEMBRO e código do direito de autor e
direitos conexos.

TUU.BUILDING DESIGN MANAGEMENT

arquitetura@tuu.pt

www.tuu.pt



LEGENDA:

	QUADRO ELÉTRICO DO EDIFÍCIO
	TOMADA ELÉTRICA 2P+T, 16A, ENCASTRAR
	TOMADA ELÉTRICA 2P+T, 16A, ENCASTRAR, C/TAMPA IP44
	TOMADA ELÉTRICA 2P+T, 16A, ESTANQUE IP65, ENCASTRAR
	TOMADA ELÉTRICA 2P+T, 16A, ESTANQUE IP65, SALIENTE
	TOMADA DE CHÃO ELETRICIDADE (2 módulos) 1x 2P+T 16A
	ALIMENTAÇÃO ELÉTRICA ESPECÍFICA
	DOWNLIGHT LED COMPACTO DE ENCASTRAR, 2,5W 3000K IP43 Ø27mm
	APLIQUE DE PAREDE SALIENTE RETANGULAR, LUZ DESCENDENTE E ASCENDENTE
	Placa Superfície LED Quadrada 18W 225x225 mm; Ref. efectLED 407
	LUMINÁRIA LED DE ENCASTRAR BALIZADOR, Ø33mm, 2,5W, 3000K, IP65 IK10
	Piafon LED 20W PHILIPS CL200; Ref. efectLED 85955
	LUMINÁRIA LED DE ENCASTRAR, 5W, 3000K, IP65 IK10
	INTERRUPTOR SIMPLES DE ENCASTRAR (A=1,10m)
	COMUTADOR DE ESCADA DE ENCASTRAR (A=1,10m)
	DETETOR DE MOVIMENTO 360° DE ENCASTRAR
	DETETOR DE MOVIMENTO 180° SALIENTE
	BOTÃO DE PRESSÃO DE ENCASTRAR (A=1,10m)
	BLOCO DE ILUMINAÇÃO DE SEGURANÇA, >1h, 100lm, IP42/65

LEGENDA VIDEOPORTEIRO

	BOTONEIRA VP EXTERIOR
	TRINCO ELÉTRICO
	MONITOR VP INTERIOR
	ALIMENTADOR VP

*AL - Alimentação do Bloco Autónomo feita a partir do circuito de iluminação local

TUU

BRUN
O
EXEM
PLO

0000
0000
2
, COIMBRA

REDE DE TERRAS
PISO 1

EL011

Nome Ficheiro
TUU_MBERAL_PE_ELE_PD_V00.DWG

Equipa

AN A EX EM PL O | ENG ELETROTÉCNICO
EMANUEL SILVA | ENG ELETROTÉCNICO

Reprodução proibida, Dec. Lei 45\85 de 17 de
DEZEMBRO e código do direito de autor e
direitos conexos.

arquitetura@tuu.pt www.tuu.pt

	QUADRO ELÉTRICO DO EDIFÍCIO
	TOMADA ELÉTRICA 2P+T, 16A, ENCASTRAR
	TOMADA ELÉTRICA 2P+T, 16A, ENCASTRAR, C/TAMPA IP44
	TOMADA ELÉTRICA 2P+T, 16A, ESTANQUE IP65, ENCASTRAR
	TOMADA ELÉTRICA 2P+T, 16A, ESTANQUE IP65, SALIENTE
	TOMADA DE CHÃO ELETTRICIDADE (2 módulos) 1x 2P+T 16A
	ALIMENTAÇÃO ELÉTRICA ESPECÍFICA
	DOWNLIGHT LED COMPACTO DE ENCASTRAR, 2,5W 3000K IP43 Ø27mm
	APLIQUE DE PAREDE SALIENTE RETANGULAR, LUZ DESCENDENTE E ASCENDENTE
	Placa Superfície LED Quadrada 18W 225x225 mm; Ref. efectLED 407
	LUMINÁRIA LED DE ENCASTRAR BALIZADOR, Ø33mm, 2,5W, 3000K, IP65 IK10
	Plafon LED 20W PHILIPS CL200; Ref. efectLED 85955
	LUMINÁRIA LED DE ENCASTRAR, 5W, 3000K, IP65 IK10
	INTERRUPTOR SIMPLES DE ENCASTRAR (A=1,10m)
	COMUTADOR DE ESCADA DE ENCASTRAR (A=1,10m)
	DETECTOR DE MOVIMENTO 360° DE ENCASTRAR
	DETECTOR DE MOVIMENTO 180° SALIENTE
	BOTÃO DE PRESSÃO DE ENCASTRAR (A=1,10m)
	BLOCO DE ILUMINAÇÃO DE SEGURANÇA, >1h, 100lm, IP42/85

LEGENDA VIDEOPORTEIRO	
 Botoneira VP	BOTONEIRA VP EXTERIOR
	TRINCO ELÉTRICO
 VP	MONITOR VP INTERIOR
	ALIMENTADOR VP

00	Entrega do Projeto de Execução	30.06.2026
Revisão	Descrição	Data

TUU

Requerente

BRUNO
O EXEMPLO

Projeto
MBERAL

Rua Eng. Miguel
03
000 0-00 2, COIMBRA

Especialidade
PROJETO DE ELETRICIDADE
PROJETO DE EXECUÇÃO

Designação

VIDEOPORTEIRO
PISO 1

JUNHO 2026
1:100

EL012

Observações

ESTE PROJETO DEVERÁ SER LIDO EM CONJUNTO COM AS PEÇAS
ESCRITAS, ASSIM COMO, O PROJETO DE ARQUITETURA E AS
REMANESCENTES ESPECIALIDADES.
QUAISQUER DISCREPÂNCIAS DEVERÃO SER COMUNICADAS AO
PROJETISTA. TODAS AS MEDIDAS DESTES DESENHOS SÃO DE
PROJETO E MERAMENTE INDICATIVAS, NECESSITAM SER
RETIFICADAS EM OBRA.

Nome Ficheiro

TUU_MBERAL_PE_ELE_PD_V00.DWG

Código

24932024

Equipa

ENG ELETROTÉCNICO
EMANUEL SILVA | ENG ELETROTÉCNICO

Reprodução proibida, Dec. Lei 45/85 de 17 de
DEZEMBRO e código do direito de autor e
direitos conexos.

TUU.BUILDING DESIGN MANAGEMENT

arquitetura@tuu.pt

www.tuu.pt

LEGENDA:

	QUADRO ELÉTRICO DO EDIFÍCIO
	TOMADA ELÉTRICA 2P+T, 16A, ENCASTRAR
	TOMADA ELÉTRICA 2P+T, 16A, ENCASTRAR, C/TAMPA IP44
	TOMADA ELÉTRICA 2P+T, 16A, ESTANQUE IP65, ENCASTRAR
	TOMADA ELÉTRICA 2P+T, 16A, ESTANQUE IP65, SALIENTE
	TOMADA DE CHÃO ELETRICIDADE (2 módulos) 1x 2P+T 16A
	ALIMENTAÇÃO ELÉTRICA ESPECÍFICA
	DOWLIGHT LED COMPACTO DE ENCASTRAR, 2,5W 3000K IP43 Ø27mm
	APLIQUE DE PAREDE SALIENTE RETANGULAR, LUZ DESCENDENTE E ASCENDENTE
	Placa Superfície LED Quadrada 18W 225x225 mm; Ref. efectoLED 407
	LUMINÁRIA LED DE ENCASTRAR BALIZADOR, Ø33mm, 2,5W, 3000K, IP65 IK10
	Plafon LED 20W PHILIPS CL200; Ref. efectoLED 85955
	LUMINÁRIA LED DE ENCASTRAR, 5W, 3000K, IP65 IK10
	INTERRUPTOR SIMPLES DE ENCASTRAR (A=1,10m)
	COMUTADOR DE ESCADA DE ENCASTRAR (A=1,10m)
	DETETOR DE MOVIMENTO 360° DE ENCASTRAR
	DETETOR DE MOVIMENTO 180° SALIENTE
	BOTÃO DE PRESSÃO DE ENCASTRAR (A=1,10m)
	BLOCO DE ILUMINAÇÃO DE SEGURANÇA, >1h, 100lm, IP42/65

LEGENDA VIDEOPORTEIRO

	BOTONEIRA VP EXTERIOR
	TRINCO ELÉTRICO
	MONITOR VP INTERIOR
	ALIMENTADOR VP



00	Entrega do Projeto de Execução	30.06.2026
Revisão	Descrição	Data

TUU

Requerente

BRUNO
O EXEMPLO

Projeto
MBERAL

Especialidade

PROJETO DE ELETRICIDADE
PROJETO DE EXECUÇÃO

Designação

VIDEOPORTEIRO
PISO 2

JUNHO 2026
1:100

EL013

Observações

ESTE PROJETO DEVERÁ SER LIDO EM CONJUNTO COM AS PEÇAS
ESCRITAS, ASSIM COMO, O PROJETO DE ARQUITETURA E AS
REstantes ESPECIALIDADES.
QUAISQUER DISCREPÂNCIAS DEVERÃO SER COMUNICADAS AO
PROJETISTA. TODAS AS MEDIDAS DESTES DESENHOS SÃO DE
PROJETO E MERAMENTE INDICATIVAS, NECESSITAM SER
RETIFICADAS EM OBRA.

Nome Ficheiro

TUU_MBERAL_PE_ELE_PD_V00.DWG

Código

24932024

Equipa

MANUEL SILVA | ENG ELETROTÉCNICO
EMANUEL SILVA | ENG ELETROTÉCNICO

Reprodução proibida, Dec. Lei 45/85 de 17 de
DEZEMBRO e código do direito de autor e
direitos conexos.

TUU.BUILDING DESIGN MANAGEMENT

arquitetura@tuu.pt

www.tuu.pt

LEGENDA:

	QUADRO ELÉTRICO DO EDIFÍCIO
	TOMADA ELÉTRICA 2P+T, 16A, ENCASTRAR
	TOMADA ELÉTRICA 2P+T, 16A, ENCASTRAR, C/TAMPA IP44
	TOMADA ELÉTRICA 2P+T, 16A, ESTANQUE IP65, ENCASTRAR
	TOMADA ELÉTRICA 2P+T, 16A, ESTANQUE IP65, SALIENTE
	TOMADA DE CHÃO ELETRICIDADE (2 módulos) 1x 2P+T 16A
	ALIMENTAÇÃO ELÉTRICA ESPECÍFICA
	DOWNLIGHT LED COMPACTO DE ENCASTRAR, 2,5W 3000K IP43 Ø27mm
	APLIQUE DE PAREDE SALIENTE RETANGULAR, LUZ DESCENDENTE E ASCENDENTE
	Placa Superfície LED Quadrada 18W 225x225 mm; Ref. efectLED 407
	LUMINÁRIA LED DE ENCASTRAR BALIZADOR, Ø33mm, 2,5W, 3000K, IP65 IK10
	Plafon LED 20W PHILIPS CL200; Ref. efectLED 85955
	LUMINÁRIA LED DE ENCASTRAR, 5W, 3000K, IP65 IK10
	INTERRUPTOR SIMPLES DE ENCASTRAR (A=1,10m)
	COMUTADOR DE ESCADA DE ENCASTRAR (A=1,10m)
	DETETOR DE MOVIMENTO 360° DE ENCASTRAR
	DETETOR DE MOVIMENTO 180° SALIENTE
	BOTÃO DE PRESSÃO DE ENCASTRAR (A=1,10m)
	BLOCO DE ILUMINAÇÃO DE SEGURANÇA, >1h, 100lm, IP42/65

LEGENDA VIDEOPORTEIRO

	BOTONEIRA VP EXTERIOR
	TRINCO ELÉTRICO
	MONITOR VP INTERIOR
	ALIMENTADOR VP



00	Entrega do Projeto de Execução	30.06.2026
Revisão	Descrição	Data

TUU

Requerente

BRUNO EXEMPLO

Projeto
MBERAL

Rua Eng. João de Deus, 100
3000-000, COIMBRA

Especialidade
PROJETO DE ELETRICIDADE
PROJETO DE EXECUÇÃO

Designação

VIDEOPORTEIRO
PISO 3

JUNHO 2026
1:100

EL014

Observações

ESTE PROJETO DEVERÁ SER LIDO EM CONJUNTO COM AS PEÇAS ESCRITAS, ASSIM COMO, O PROJETO DE ARQUITETURA E AS RESTANTES ESPECIALIDADES. QUAISQUER DISCREPÂNCIAS DEVERÃO SER COMUNICADAS AO PROJETISTA. TODAS AS MEDIDAS DESTES DESENHOS SÃO DE PROJETO E MERAMENTE INDICATIVAS, NECESSITAM SER RETIFICADAS EM OBRA.

Nome Ficheiro

TUU_MBERAL_PE_ELE_PD_V00.DWG

Código

24932024

Equipa

MANUEL SILVA | ENG ELETROTÉCNICO
EMANUEL SILVA | ENG ELETROTÉCNICO

Reprodução proibida, Dec. Lei 45/85 de 17 de DEZEMBRO e código do direito de autor e direitos conexos.

TUU.BUILDING DESIGN MANAGEMENT

arquitetura@tuu.pt

www.tuu.pt

LEGENDA:

	QUADRO ELÉTRICO DO EDIFÍCIO
	TOMADA ELÉTRICA 2P+T, 16A, ENCASTRAR
	TOMADA ELÉTRICA 2P+T, 16A, ENCASTRAR, C/TAMPA IP44
	TOMADA ELÉTRICA 2P+T, 16A, ESTANQUE IP65, ENCASTRAR
	TOMADA ELÉTRICA 2P+T, 16A, ESTANQUE IP65, SALIENTE
	TOMADA DE CHÃO ELETRICIDADE (2 módulos) 1x 2P+T 16A
	ALIMENTAÇÃO ELÉTRICA ESPECÍFICA
	DOWNLIGHT LED COMPACTO DE ENCASTRAR, 2,5W 3000K IP43 Ø27mm
	APLIQUE DE PAREDE SALIENTE RETANGULAR, LUZ DESCENDENTE E ASCENDENTE
	Placa Superfície LED Quadrada 18W 225x225 mm; Ref. efectLED 407
	LUMINÁRIA LED DE ENCASTRAR BALIZADOR, Ø33mm, 2,5W, 3000K, IP65 IK10
	Piafon LED 20W PHILIPS CL200; Ref. efectLED 85955
	LUMINÁRIA LED DE ENCASTRAR, 5W, 3000K, IP65 IK10
	INTERRUPTOR SIMPLES DE ENCASTRAR (A=1,10m)
	COMUTADOR DE ESCADA DE ENCASTRAR (A=1,10m)
	DETETOR DE MOVIMENTO 360° DE ENCASTRAR
	DETETOR DE MOVIMENTO 180° SALIENTE
	BOTÃO DE PRESSÃO DE ENCASTRAR (A=1,10m)
	BLOCO DE ILUMINAÇÃO DE SEGURANÇA, >1h, 100lm, IP42/65

LEGENDA VIDEOPORTEIRO

	BOTONEIRA VP EXTERIOR
	TRINCO ELÉTRICO
	MONITOR VP INTERIOR
	ALIMENTADOR VP



PODER DE CORTE DOS DISJUNTORES
NÃO INFERIOR A 50A (IEC-10088-1)

A CAIXA EXTERIOR DO QUADRO DE
CLASSE II DE ISOLAMENTO

Q.E.G.(N)

Classe II
IP42 IK04
Icc = 6kA

Da Portinhola
RV-K - 4x16mm²

3F+N, 230/400V
50Hz, In=50A

NºCirc.	Fase	Pot. (VA)	CANALIZAÇÃO	DESTINO
IL1	L1	---	3x H07V-K 15mm ²	Illumin. Circulações - I1.1, I1.2
IS1	L1	---	3x H07V-K 15mm ²	Illuminação Segurança
IL2	L1	---	3x H07V-K 15mm ²	Illumin. Circulação - I2.1, I2.2, I2.3
IS2	L1	---	3x H07V-K 15mm ²	Illuminação Segurança
IL3	L1	---	3x H07V-K 15mm ²	Illumin. Circulação - I3.1
IS3	L1	---	3x H07V-K 15mm ²	Illuminação Segurança
T3	L1	---	3x H07V-K 2,5mm ²	Vídeo Porteiro
T3	L1	---	3x H07V-K 2,5mm ²	ATI
				Reserva Não Equipada
				Reserva Não Equipada
ALE1	L2	---	3x H07V-K 10mm ²	Alimentação Q.P.1.1
ALE2	L2	---	3x H07V-K 10mm ²	Alimentação Q.P.1.2
ALE3	L3	---	3x H07V-K 10mm ²	Alimentação Q.P.2.1
ALE4	L3	---	3x H07V-K 10mm ²	Alimentação Q.P.2.2
ALE5	L1	---	3x H07V-K 10mm ²	Alimentação Q.P.3.1
				Reserva Não Equipada

Q.P.1.1

Classe II
IP42 IK04
Icc = 6kA

POTER DE CORTE DOS DISJUNTORES
PACHENSBROU A-K-REC 08B-1

A CAIXA EXTERIOR DO QUADRO DE
CLASSE II DE ISOLAMENTO

NºCirc.	Fase	Pot. (VA)	CANALIZAÇÃO	DESTINO
IL1	L2	---	3x H07V-K 1,5mm²	Iluminação - IT1, IT2
IL2	L2	---	3x H07V-K 1,5mm²	Iluminação - IZ1, IZ2
IL3	L2	---	---	Reserva Não Equipada
T1	L2	---	3x H07V-K 2,5mm²	Tomadas Iso Geral - T1
T2	L2	---	3x H07V-K 2,5mm²	Tomadas Iso Geral - T2
T3	L2	---	3x H07V-K 2,5mm²	Tomadas Iso Geral Cozinha
T4	L2	---	---	Reserva Não Equipada
ALE1	L2	---	3x H07V-K 4mm²	Forno
ALE2	L2	---	3x H07V-K 4mm²	Placa de Indução
ALE3	L2	---	3x H07V-K 2,5mm²	Tomada Exaustor
ALE4	L2	---	3x H07V-K 2,5mm²	Tomadas Frigorífico
ALE5	L2	---	3x H07V-K 2,5mm²	Tomada Máquina Lavar Roupa
ALE6	L2	---	---	Reserva Não Equipada
ALE7	L2	---	RV-K 3G52,5mm²	Termoacumulador Elétrico 180L
ALE8	L2	---	RV-K 3G52,5mm²	Unidade Exterior 1
ALE9	L2	---	3x H07V-K 1,5mm²	Ventilador de Extração 1
ALE10	L2	---	3x H07V-K 1,5mm²	Hotte Doméstico 1

Q.P. 1.2

Classe II
IP42 IK04
Icc = 6kA

POTER DE CORTE DOS DISJUNTORES
NÃO SUPERAR A VALOR (GSH-1)

A CABA EXTERIOR DO QUADRO DE CLASSE II DE ISOLAMENTO

NºCirc.	Fase	Pot. (VA)	CANALIZAÇÃO	DESTINO
IL1	L2	---	3x H07V-K 1,5mm ²	Iluminação - IT1, IT2
IL2	L2	---	3x H07V-K 1,5mm ²	Iluminação - IZ1, IZ2
IL3	L2	---	3x H07V-K 1,5mm ²	Reserva Não Equipada
T1	L2	---	3x H07V-K 2,5mm ²	Tomadas Iso Geral - T1
T2	L2	---	3x H07V-K 2,5mm ²	Tomadas Iso Geral - T2
T3	L2	---	3x H07V-K 2,5mm ²	Tomadas Iso Geral Cozinha
T4	L2	---	3x H07V-K 2,5mm ²	Reserva Não Equipada
ALE1	L2	---	3x H07V-K 4mm ²	Forno
ALE2	L2	---	3x H07V-K 4mm ²	Placa de Indução
ALE3	L2	---	3x H07V-K 2,5mm ²	Tomada Exaustor
ALE4	L2	---	3x H07V-K 2,5mm ²	Tomadas Fridgeiro
ALE5	L2	---	3x H07V-K 2,5mm ²	Tomada Máquina Lavar Roupas
ALE6	L2	---	RV-K 3G52,5mm ²	Reserva Não Equipada
ALE7	L2	---	RV-K 3G52,5mm ²	Termoacumulador Elétrico 2 BBL
ALE8	L2	---	RV-K 3G52,5mm ²	Unidade Exterior 2
ALE9	L2	---	3x H07V-K 1,5mm ²	Ventilador de Extração 2
ALE10	L2	---	3x H07V-K 1,5mm ²	Hote Doméstico 2

00	Entrega do Projeto de Execução	30.06.2026
Revisão	Descrição	Data

TUU

Requerente

BRUN
O
EXEM
PLO

Projeto
MBERAL

0000
0000
2
, COIMBRA

Especialidade
PROJETO DE ELETRICIDADE
PROJETO DE EXECUÇÃO

Designação
**ESQUEMAS DOS QUADROS
ELÉTRICOS**

JUNHO 2026
S/ESCALA

EL015

Observações

ESTE PROJETO DEVERÁ SER LIDO EM CONJUNTO COM AS PEÇAS
ESCRITAS, ASSIM COMO, O PROJETO DE ARQUITETURA E AS
REMANESCENTES ESPECIALIDADES.

QUAISQUER DISCREPÂNCIAS DEVERÃO SER COMUNICADAS AO
PROJETISTA. TODAS AS MEDIDAS DESTES DESENHOS SÃO DE
PROJETO E MERAMENTE INDICATIVAS, NECESSITAM SER
RETIFICADAS EM OBRA.

Nome Ficheiro

TUU_MBERAL_PE_ELE_PD_V00.DWG

Código

24932024

Equipa

ANEXO | ENG ELETROTÉCNICO
EMANUEL SILVA | ENG ELETROTÉCNICO


Reprodução proibida, Dec. Lei 45\85 de 17 de DEZEMBRO e código do direito de autor e direitos conexos.

TUU.BUILDING DESIGN MANAGEMENT


arquitetura@tuu.pt

www.tuu.pt


Quadro Parcial 2.1

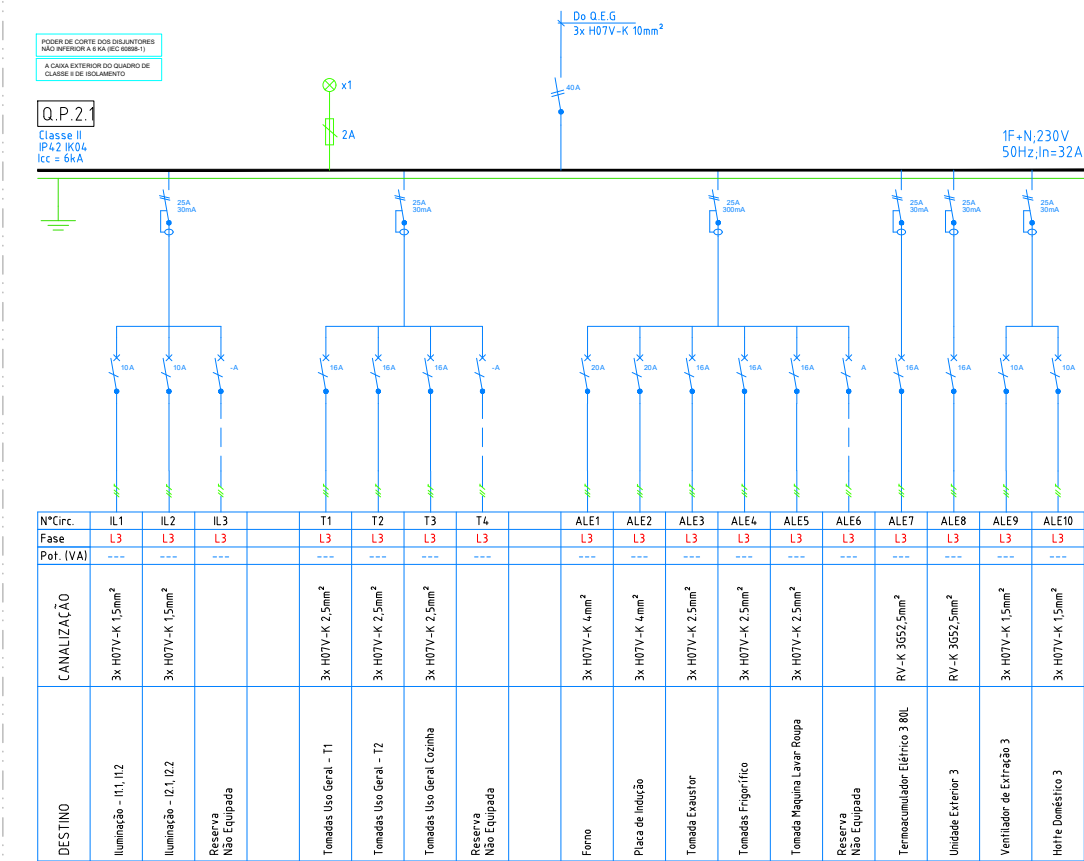

Quadro Parcial 2.2

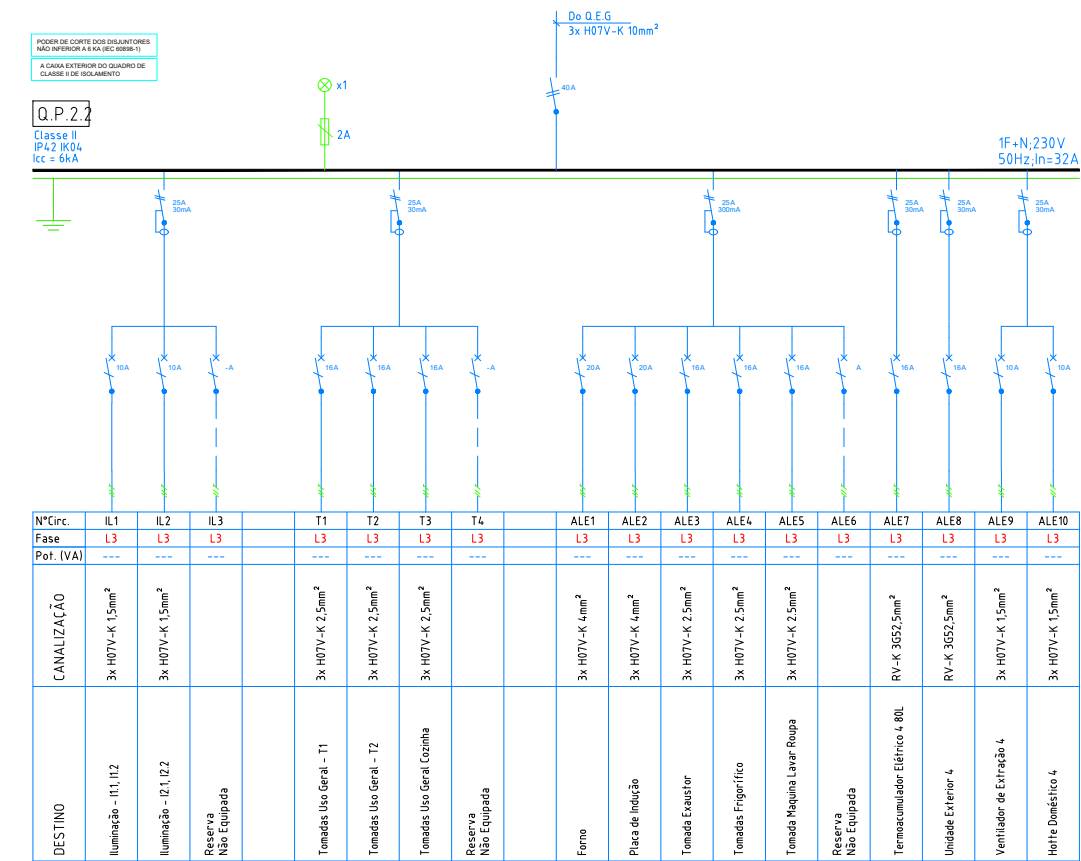

Quadro Parcial 3.1

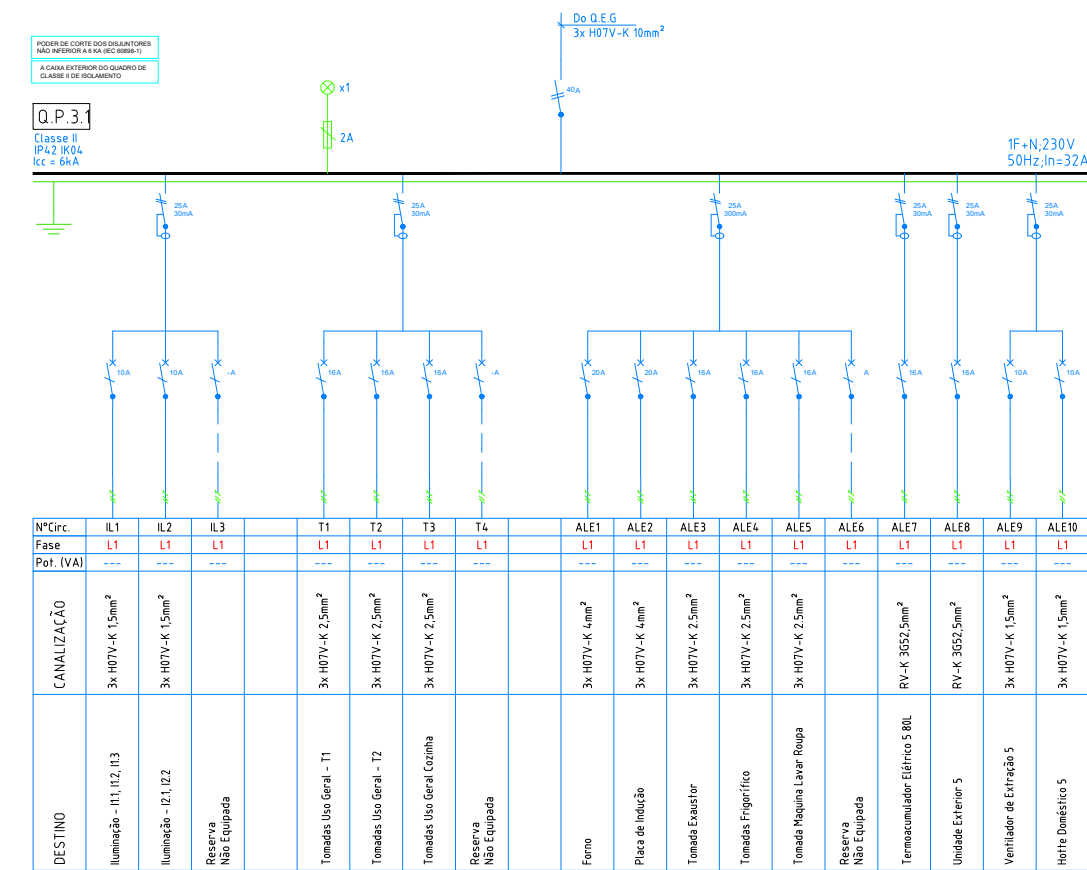

TUU

Requerente

BRUNO
O EXEMPLO

Projeto

MBERAL

Especialidade

PROJETO DE ELETRICIDADE
PROJETO DE EXECUÇÃO

Designação

ESQUEMAS DOS QUADROS
ELÉTRICOS

JUNHO 2026

S/ESCALA

EL016

Observações

ESTE PROJETO DEVERÁ SER LIDO EM CONJUNTO COM AS PEÇAS ESCRITAS, ASSIM COMO, O PROJETO DE ARQUITETURA E AS RESTANTES ESPECIALIDADES.
QUAISQUER DISCREPÂNCIAS DEVERÃO SER COMUNICADAS AO PROJETISTA. TODAS AS MEDIDAS DESTES DESENHO SÃO DE PROJETO E MERAMENTE INDICATIVAS, NECESSITAM SER RETIFICADAS EM OBRA.

Nome Ficheiro

TUU_MBERAL_PE_ELE_PD_V00.DWG

Código

24932024

Equipa

ENG ELETROTÉCNICO
EMANUEL SILVA | ENG ELETROTÉCNICO

Reprodução proibida, Dec. Lei 45/85 de 17 de DEZEMBRO e código do direito de autor e direitos conexos.

TUU.BUILDING DESIGN MANAGEMENT

arquitetura@tuu.pt

www.tuu.pt