

00	Entrega do Projeto de Execução	30.06.2026
Revisão	Descrição	Data

TUU

Requerente

BRUNO EXEMPLO

Projeto
MBERAL

Rua Esmeralda, 1000, COIMBRA

Especialidade
PROJETO DE ELETRICIDADE
PROJETO DE EXECUÇÃO

Designação

ÍNDICE

JUNHO 2026
S/ESCALA

EL001

Observações

ESTE PROJETO DEVERÁ SER LIDO EM CONJUNTO COM AS PEÇAS ESCRITAS, ASSIM COMO, O PROJETO DE ARQUITETURA E AS RESTANTES ESPECIALIDADES. QUAISQUER DISCREPÂNCIAS DEVERÃO SER COMUNICADAS AO PROJETISTA. TODAS AS MEDIDAS DESTES DESENHOS SÃO DE PROJETO E MERAMENTE INDICATIVAS, NECESSITAM SER RETIFICADAS EM OBRA.

Nome Ficheiro
TUU_MBERAL_PE_ELE_PD_V00.DWG

Código
24932024

Equipa
MANUEL SILVA | ENG ELETROTÉCNICO
EMANUEL SILVA | ENG ELETROTÉCNICO

Reprodução proibida, Dec. Lei 45/85 de 17 de DEZEMBRO e código do direito de autor e direitos conexos.

TUU.BUILDING DESIGN MANAGEMENT

arquitetura@tuu.pt www.tuu.pt

	TÍTULO	DATA	REV
EL001	ÍNDICE	06/26	-
EL002	PISO 1 - DISTRIBUIÇÃO DE ENERGIA	06/26	-
EL003	PISO 2 - DISTRIBUIÇÃO DE ENERGIA	06/26	-
EL004	PISO 3 - DISTRIBUIÇÃO DE ENERGIA	06/26	-
EL005	PISO 1 - TOMADAS	06/26	-
EL006	PISO 2 - TOMADAS	06/26	-
EL007	PISO 3 - TOMADAS	06/26	-
EL008	PISO 1 - ILUMINAÇÃO	06/26	-
EL009	PISO 2 - ILUMINAÇÃO	06/26	-
EL010	PISO 3 - ILUMINAÇÃO	06/26	-
EL011	REDE DE TERRAS	06/26	-
EL012	PISO 1 - VÍDEO PORTEIRO	06/26	-
EL013	PISO 2 - VÍDEO PORTEIRO	06/26	-
EL014	PISO 3 - VÍDEO PORTEIRO	06/26	-
EL015	ESQUEMAS QUADROS ELÉTRICOS	06/26	-
EL016	ESQUEMAS QUADROS ELÉTRICOS	06/26	-
EL017	DIAGRAMA DE DISTRIBUIÇÃO QUADROS ELÉTRICOS	06/26	-

TUW


BRUN
O
EXEM
PLO

000
0-00
2 , COIMBRA

JUNHO 2026
1:100

EL002

arquitetura@tuu.pt www.tuu.pt

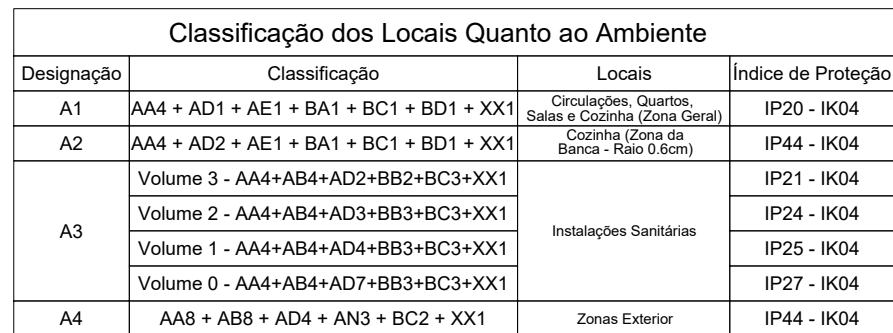

	QUADRO ELÉTRICO DO EDIFÍCIO
	TOMADA ELÉTRICA 2P+T, 16A, ENCASTRAR
	TOMADA ELÉTRICA 2P+T, 16A, ENCASTRAR, C/TAMPA IP44
	TOMADA ELÉTRICA 2P+T, 16A, ESTANQUE IP65, ENCASTRAR
	TOMADA ELÉTRICA 2P+T, 16A, ESTANQUE IP65, SALIENTE
	TOMADA DE CHÃO ELETRICIDADE (2 módulos) 1x 2P+T 16A
	ALIMENTAÇÃO ELÉTRICA ESPECÍFICA
	DOWNLIGHT LED COMPACTO DE ENCASTRAR, 2,5W 3000K IP43 Ø27mm
	APLIQUE DE PAREDE SALIENTE RETANGULAR, LUZ DESCENDENTE E ASCENDENTE
	Placa Superfície LED Quadrada 18W 225x225 mm; Ref. efectLED 407
	LUMINÁRIA LED DE ENCASTRAR BALIZADOR, Ø33mm, 2,5W, 3000K, IP65 IK10
	Plafon LED 20W PHILIPS CL200; Ref. efectLED 85955
	LUMINÁRIA LED DE ENCASTRAR, 5W, 3000K, IP65 IK10
	INTERRUPTOR SIMPLES DE ENCASTRAR (A=1,10m)
	COMUTADOR DE ESCADA DE ENCASTRAR (A=1,10m)
	DETECTOR DE MOVIMENTO 360° DE ENCASTRAR
	DETECTOR DE MOVIMENTO 180° SALIENTE
	BOTÃO DE PRESSÃO DE ENCASTRAR (A=1,10m)
	BLOCO DE ILUMINAÇÃO DE SEGURANÇA, >1h, 100lm; IP42/65

 Botoneira VP	BOTONEIRA VP EXTERIOR
	TRINCO ELÉTRICO
VP	MONITOR VP INTERIOR
	ALIMENTADOR VP

TUW

BRUN
O
EXEM
PLO

Rua
Exe
mpl
03
000
0-00
2
, COIMBRA

Designação

JUNHO 2026
1:100

EL003

TUU_MBERAL_PE_ELE_PD_V00.DWG

24932024

ANEXO | ENG ELETROTÉCNICO
EMANUEL SILVA | ENG ELETROTÉCNICO

arquitetura@tuu.pt

www.tuu.pt

	QUADRO ELÉTRICO DO EDIFÍCIO
	TOMADA ELÉTRICA 2P+T, 16A, ENCASTRAR
	TOMADA ELÉTRICA 2P+T, 16A, ENCASTRAR, C/TAMPA IP44
	TOMADA ELÉTRICA 2P+T, 16A, ESTANQUE IP65, ENCASTRAR
	TOMADA ELÉTRICA 2P+T, 16A, ESTANQUE IP65, SALIENTE
	TOMADA DE CHÃO ELETRICIDADE (2 módulos) 1x 2P+T 16A
	ALIMENTAÇÃO ELÉTRICA ESPECÍFICA
	L1 DOWNLIGHT LED COMPACTO DE ENCASTRAR, 2,5W 3000K IP43 Ø27mm
	L7 APLIQUE DE PAREDE SALIENTE RETANGULAR, LUZ DESCENDENTE E ASCENDENTE
	L8 Placa Superfície LED Quadrada 18W 225x225 mm; Ref. efectoLED 407
	L9 LUMINÁRIA LED DE ENCASTRAR BALIZADOR, Ø33mm, 2,5W, 3000K, IP65 IK10
	L14 Plafon LED 20W PHILIPS CL200; Ref. efectoLED 85955
	L15 LUMINÁRIA LED DE ENCASTRAR, 5W, 3000K, IP65 IK10
	INTERRUPTOR SIMPLES DE ENCASTRAR (A=1,10m)
	COMUTADOR DE ESCADA DE ENCASTRAR (A=1,10m)
	DETETOR DE MOVIMENTO 360° DE ENCASTRAR
	DETETOR DE MOVIMENTO 180° SALIENTE
	BOTÃO DE PRESSÃO DE ENCASTRAR (A=1,10m)
	BLOCO DE ILUMINAÇÃO DE SEGURANÇA, >1h, 100lm, IP42/65

	BOTONEIRA VP EXTERIOR
	TRINCO ELÉTRICO
	MONITOR VP INTERIOR
	ALIMENTADOR VP

Designação	Classificação	Locais	Índice de Proteção
A1	AA4 + AD1 + AE1 + BA1 + BC1 + BD1 + XX1	Circulações, Quartos, Salas e Cozinha (Zona Geral)	IP20 - IK04
A2	AA4 + AD2 + AE1 + BA1 + BC1 + BD1 + XX1	Cozinha (Zona da Banca - Raio 0,6cm)	IP44 - IK04
A3	Volume 3 - AA4+AB4+AD2+BB2+BC3+XX1	Instalações Sanitárias	IP21 - IK04
	Volume 2 - AA4+AB4+AD3+BB3+BC3+XX1		IP24 - IK04
	Volume 1 - AA4+AB4+AD4+BB3+BC3+XX1		IP25 - IK04
	Volume 0 - AA4+AB4+AD7+BB3+BC3+XX1		IP27 - IK04
A4	AA8 + AB8 + AD4 + AN3 + BC2 + XX1	Zonas Exterior	IP44 - IK04

TUU

BRUN
O
EXEM
PLO

000
0-00
2 , COIMBRA

JUNHO 2026
1:100

EL004

arquitetura@tuu.pt www.tuu.pt

	QUADRO ELÉTRICO DO EDIFÍCIO
	TOMADA ELÉTRICA 2P+T, 16A, ENCASTRAR
	TOMADA ELÉTRICA 2P+T, 16A, ENCASTRAR, C/TAMPA IP44
	TOMADA ELÉTRICA 2P+T, 16A, ESTANQUE IP65, ENCASTRAR
	TOMADA ELÉTRICA 2P+T, 16A, ESTANQUE IP65, SALIENTE
	TOMADA DE CHÃO ELETRICIDADE (2 módulos) 1x 2P+T 16A
	ALIMENTAÇÃO ELÉTRICA ESPECÍFICA
	DOWNLIGHT LED COMPACTO DE ENCASTRAR, 2,5W 3000K IP43 Ø27mm
	APLIQUE DE PAREDE SALIENTE RETANGULAR, LUZ DESCENDENTE E ASCENDENTE
	Placa Superfície LED Quadrada 18W 225x225 mm, Ref. efectoLED 407
	LUMINÁRIA LED DE ENCASTRAR BALIZADOR, Ø33mm, 2,5W, 3000K, IP65 IK10
	Plafon LED 20W PHILIPS CL200, Ref. efectoLED 85955
	LUMINÁRIA LED DE ENCASTRAR, 5W, 3000K, IP65 IK10
	INTERRUPTOR SIMPLES DE ENCASTRAR (A=1,10m)
	COMUTADOR DE ESCADA DE ENCASTRAR (A=1,10m)
	DETETOR DE MOVIMENTO 360° DE ENCASTRAR
	DETETOR DE MOVIMENTO 180° SALIENTE
	BOTÃO DE PRESSÃO DE ENCASTRAR (A=1,10m)
	BLOCO DE ILUMINAÇÃO DE SEGURANÇA, >1h, 100lm, IP42/65

LEGENDA VIDEOPORTEIRO	
	BOTONEIRA VP EXTERIOR
	TRINCO ELÉTRICO
	MONITOR VP INTERIOR
	ALIMENTADOR VP

Classificação dos Locais Quanto ao Ambiente			
Designação	Classificação	Locais	Índice de Proteção
A1	AA4 + AD1 + AE1 + BA1 + BC1 + BD1 + XX1	Circulações, Quartos, Salas e Cozinha (Zona Geral)	IP20 - IK04
A2	AA4 + AD2 + AE1 + BA1 + BC1 + BD1 + XX1	Cozinha (Zona da Banca - Raio 0.6cm)	IP44 - IK04
A3	Volume 3 - AA4+AB4+AD2+BB2+BC3+XX1	Instalações Sanitárias	IP21 - IK04
	Volume 2 - AA4+AB4+AD3+BB3+BC3+XX1		IP24 - IK04
	Volume 1 - AA4+AB4+AD4+BB3+BC3+XX1		IP25 - IK04
	Volume 0 - AA4+AB4+AD7+BB3+BC3+XX1		IP27 - IK04
A4	AA8 + AB8 + AD4 + AN3 + BC2 + XX1	Zonas Exterior	IP44 - IK04

00	Entrega do Projeto de Execução	30.06.2026
Revisão	Descrição	Data

TUU

Requerente

BRUNO
O EXEMPLO

Projeto
MBERAL

Rua Eng. Miguel
03000-000, COIMBRA

Especialidade
PROJETO DE ELETRICIDADE
PROJETO DE EXECUÇÃO

Designação

TOMADAS DE USO GERAL
PISO 1

JUNHO 2026
1:100

EL005

Observações

ESTE PROJETO DEVERÁ SER LIDO EM CONJUNTO COM AS PEÇAS
ESCRITAS, ASSIM COMO, O PROJETO DE ARQUITETURA E AS
REstantes ESPECIALIDADES.
QUAISQUER DISCREPÂNCIAS DEVERÃO SER COMUNICADAS AO
PROJETISTA. TODAS AS MEDIDAS DESTES DESENHOS SÃO DE
PROJETO E MERAMENTE INDICATIVAS, NECESSITAM SER
RETIFICADAS EM OBRA.

Nome Ficheiro

TUU_MBERAL_PE_ELE_PD_V00.DWG

Código

24932024

Equipa

MANUEL SILVA | ENG. ELETROTÉCNICO
EMANUEL SILVA | ENG. ELETROTÉCNICO

Reprodução proibida, Dec. Lei 45/85 de 17 de
DEZEMBRO e código do direito de autor e
direitos conexos.

TUU.BUILDING DESIGN MANAGEMENT

arquitetura@tuu.pt

www.tuu.pt



LEGENDA:

	QUADRO ELÉTRICO DO EDIFÍCIO
	TOMADA ELÉTRICA 2P+T, 16A, ENCASTRAR
	TOMADA ELÉTRICA 2P+T, 16A, ENCASTRAR, C/TAMPA IP44
	TOMADA ELÉTRICA 2P+T, 16A, ESTANQUE IP65, ENCASTRAR
	TOMADA ELÉTRICA 2P+T, 16A, ESTANQUE IP65, SALIENTE
	TOMADA DE CHÃO ELETRICIDADE (2 módulos) 1x 2P+T 16A
	ALIMENTAÇÃO ELÉTRICA ESPECÍFICA
	DOWNLIGHT LED COMPACTO DE ENCASTRAR, 2,5W 3000K IP43 Ø27mm
	APLIQUE DE PAREDE SALIENTE RETANGULAR, LUZ DESCENDENTE E ASCENDENTE
	Placa Superfície LED Quadrada 18W 225x225 mm; Ref. efectoLED 407
	LUMINÁRIA LED DE ENCASTRAR BALIZADOR, Ø33mm, 2,5W, 3000K, IP65 IK10
	Plafon LED 20W PHILIPS CL200; Ref. efectoLED 85955
	LUMINÁRIA LED DE ENCASTRAR, 5W, 3000K, IP65 IK10
	INTERRUPTOR SIMPLES DE ENCASTRAR (A=1,10m)
	COMUTADOR DE ESCADA DE ENCASTRAR (A=1,10m)
	DETETOR DE MOVIMENTO 360° DE ENCASTRAR
	DETETOR DE MOVIMENTO 180° SALIENTE
	BOTÃO DE PRESSÃO DE ENCASTRAR (A=1,10m)
	BLOCO DE ILUMINAÇÃO DE SEGURANÇA, >1h, 100lm, IP42/65

LEGENDA VIDEOPORTEIRO

	BOTONEIRA VP EXTERIOR
	TRINCO ELÉTRICO
	MONITOR VP INTERIOR
	ALIMENTADOR VP

00	Entrega do Projeto de Execução	30.06.2026
Revisão	Descrição	Data

TUU

Requerente

BRUNO
O EXEMPLO

Projeto
MBERAL

Rua
Exemplar
03
000 0-00 2 , COIMBRA

Especialidade
PROJETO DE ELETRICIDADE
PROJETO DE EXECUÇÃO

Designação

TOMADAS DE USO GERAL
PISO 2

JUNHO 2026
1:100

EL006

Observações

ESTE PROJETO DEVERÁ SER LIDO EM CONJUNTO COM AS PEÇAS
ESCRITAS, ASSIM COMO, O PROJETO DE ARQUITETURA E AS
REstantes ESPECIALIDADES.
QUAISQUER DISCREPÂNCIAS DEVERÃO SER COMUNICADAS AO
PROJETISTA. TODAS AS MEDIDAS DESTES DESENHOS SÃO DE
PROJETO E MERAMENTE INDICATIVAS, NECESSITAM SER
RETIFICADAS EM OBRA.

Nome Ficheiro

TUU_MBERAL_PE_ELE_PD_V00.DWG

Código

24932024

Equipa

MANUEL SILVA | ENG ELETROTÉCNICO
EMANUEL SILVA | ENG ELETROTÉCNICO

Reprodução proibida, Dec. Lei 45/85 de 17 de
DEZEMBRO e código do direito de autor e
direitos conexos.

TUU.BUILDING DESIGN MANAGEMENT

arquitetura@tuu.pt


www.tuu.pt

LEGENDA:

	QUADRO ELÉTRICO DO EDIFÍCIO
	TOMADA ELÉTRICA 2P+T, 16A, ENCASTRAR
	TOMADA ELÉTRICA 2P+T, 16A, ENCASTRAR, C/TAMPA IP44
	TOMADA ELÉTRICA 2P+T, 16A, ESTANQUE IP65, ENCASTRAR
	TOMADA ELÉTRICA 2P+T, 16A, ESTANQUE IP65, SALIENTE
	TOMADA DE CHÃO ELETRICIDADE (2 módulos) 1x 2P+T 16A
	ALIMENTAÇÃO ELÉTRICA ESPECÍFICA
	DOWNLIGHT LED COMPACTO DE ENCASTRAR, 2,5W 3000K IP43 Ø27mm
	APLIQUE DE PAREDE SALIENTE RETANGULAR, LUZ DESCENDENTE E ASCENDENTE
	Placa Superfície LED Quadrada 18W 225x225 mm; Ref. efectoLED 407
	LUMINÁRIA LED DE ENCASTRAR BALIZADOR, Ø33mm, 2,5W, 3000K, IP65 IK10
	Plafon LED 20W PHILIPS CL200; Ref. efectoLED 85955
	LUMINÁRIA LED DE ENCASTRAR, 5W, 3000K, IP65 IK10
	INTERRUPTOR SIMPLES DE ENCASTRAR (A=1,10m)
	COMUTADOR DE ESCADA DE ENCASTRAR (A=1,10m)
	DETETOR DE MOVIMENTO 360° DE ENCASTRAR
	DETETOR DE MOVIMENTO 180° SALIENTE
	BOTÃO DE PRESSÃO DE ENCASTRAR (A=1,10m)
	BLOCO DE ILUMINAÇÃO DE SEGURANÇA, >1h, 100lm, IP42/65

LEGENDA VIDEOPORTEIRO

	BOTONEIRA VP EXTERIOR
	TRINCO ELÉTRICO
	MONITOR VP INTERIOR
	ALIMENTADOR VP

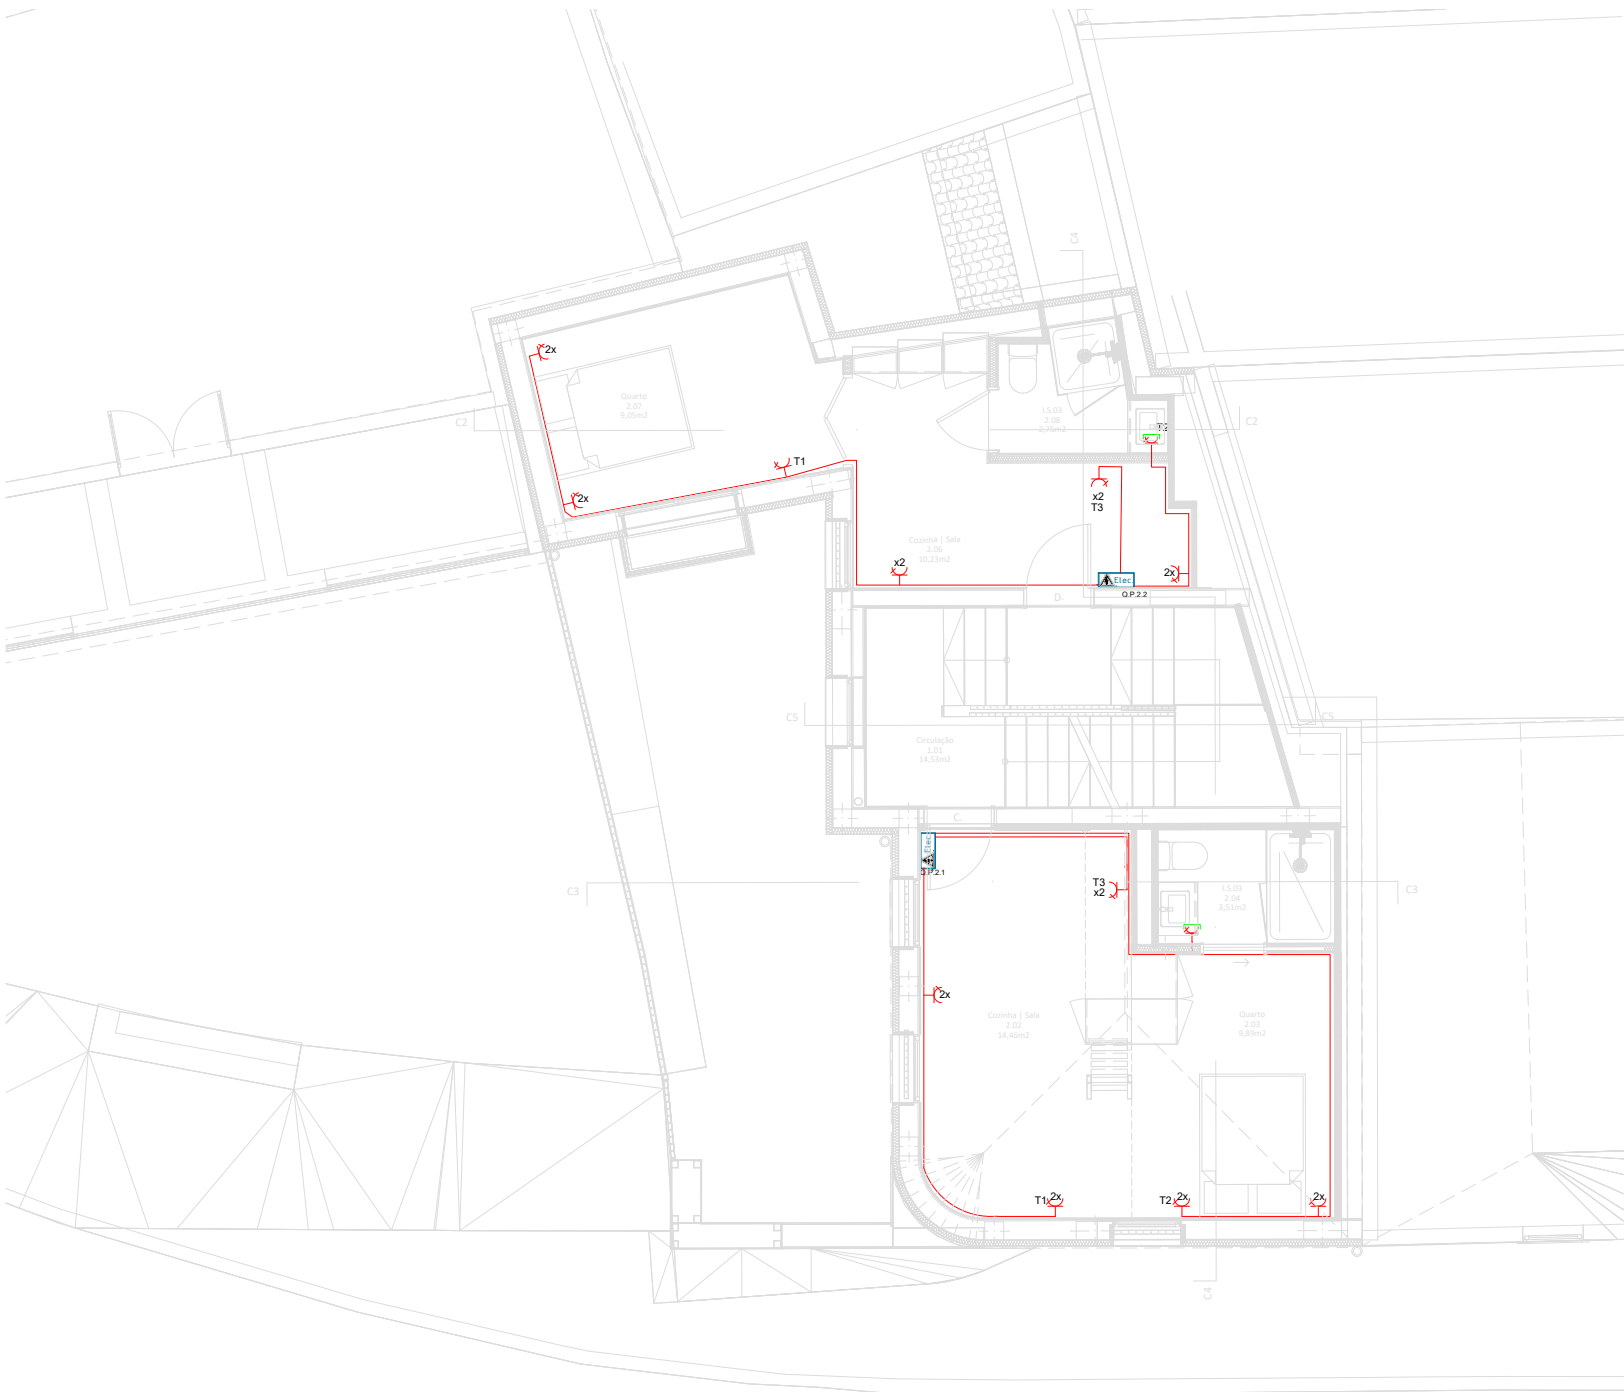

00	Entrega do Projeto de Execução	30.06.2026
Revisão	Descrição	Data

TUU

Requerente

BRUNO EXEMPLO

Projeto
MBERAL

000 0-00 2 , COIMBRA
Rua Eng. Miguel Ângelo

Especialidade
PROJETO DE ELETRICIDADE
PROJETO DE EXECUÇÃO

Designação

TOMADAS DE USO GERAL
PISO 3

JUNHO 2026
1:100

EL007

Observações

ESTE PROJETO DEVERÁ SER LIDO EM CONJUNTO COM AS PEÇAS ESCRITAS, ASSIM COMO, O PROJETO DE ARQUITETURA E AS RESTANTES ESPECIALIDADES.
QUAISQUER DISCREPÂNCIAS DEVERÃO SER COMUNICADAS AO PROJETISTA. TODAS AS MEDIDAS DESTES DESENHOS SÃO DE PROJETO E MERAMENTE INDICATIVAS, NECESSITAM SER RETIFICADAS EM OBRA.

Nome Ficheiro

TUU_MBERAL_PE_ELE_PD_V00.DWG

Código

24932024

Equipa


MANUEL SILVA | ENG ELETROTÉCNICO
EMANUEL SILVA | ENG ELETROTÉCNICO

Reprodução proibida, Dec. Lei 45/85 de 17 de DEZEMBRO e código do direito de autor e direitos conexos.

TUU.BUILDING DESIGN MANAGEMENT

arquitetura@tuu.pt

www.tuu.pt

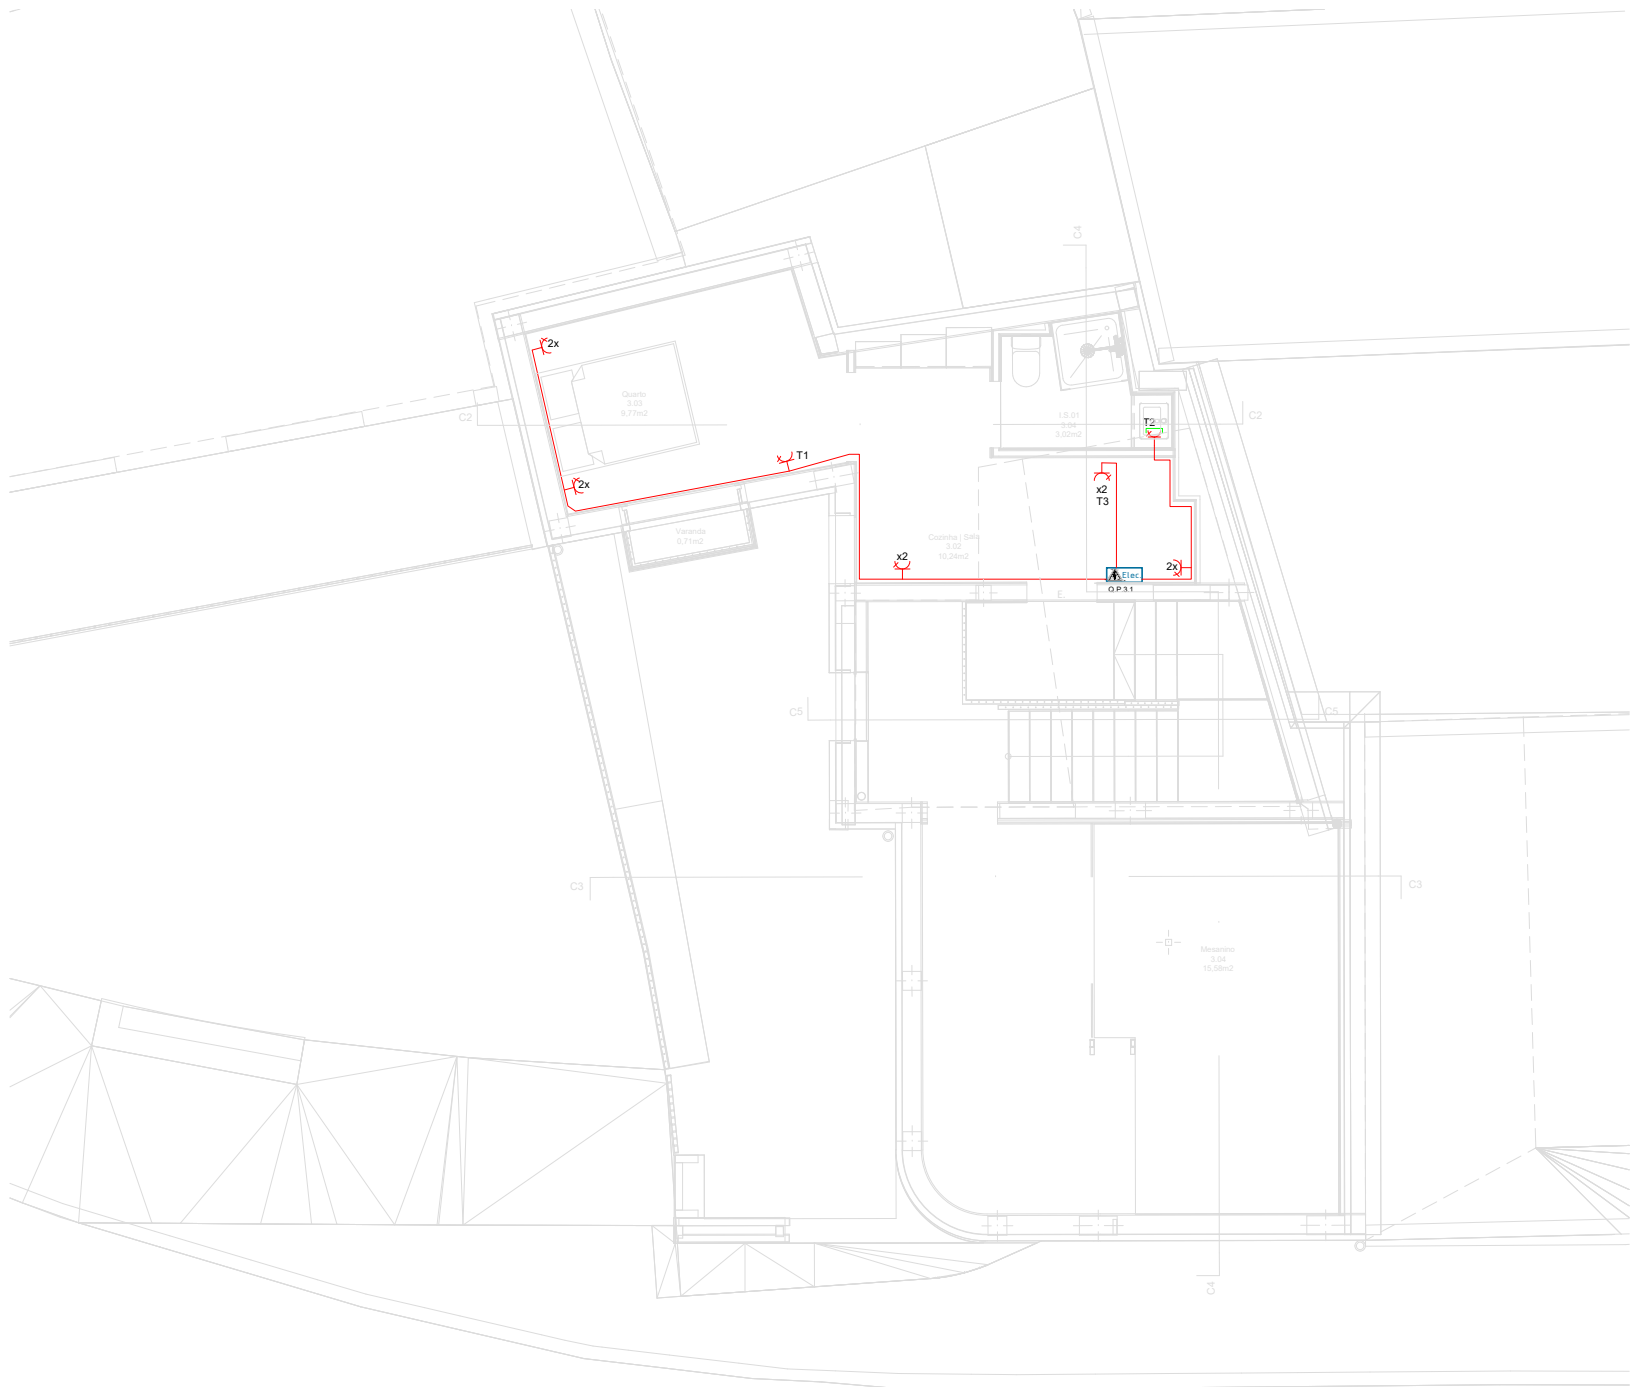

LEGENDA:

	QUADRO ELÉTRICO DO EDIFÍCIO
	TOMADA ELÉTRICA 2P+T, 16A, ENCASTRAR
	TOMADA ELÉTRICA 2P+T, 16A, ENCASTRAR, C/TAMPA IP44
	TOMADA ELÉTRICA 2P+T, 16A, ESTANQUE IP65, ENCASTRAR
	TOMADA ELÉTRICA 2P+T, 16A, ESTANQUE IP65, SALIENTE
	TOMADA DE CHÃO ELETRICIDADE (2 módulos) 1x 2P+T 16A
	ALIMENTAÇÃO ELÉTRICA ESPECÍFICA
	DOWNLIGHT LED COMPACTO DE ENCASTRAR, 2,5W 3000K IP43 Ø27mm
	APLIQUE DE PAREDE SALIENTE RETANGULAR, LUZ DESCENDENTE E ASCENDENTE
	Placa Superfície LED Quadrada 18W 225x225 mm; Ref. efectLED 407
	LUMINÁRIA LED DE ENCASTRAR BALIZADOR, Ø33mm, 2,5W, 3000K, IP65 IK10
	Plafon LED 20W PHILIPS CL200; Ref. efectLED 85955
	LUMINÁRIA LED DE ENCASTRAR, 5W, 3000K, IP65 IK10
	INTERRUPTOR SIMPLES DE ENCASTRAR (A=1,10m)
	COMUTADOR DE ESCADA DE ENCASTRAR (A=1,10m)
	DETETOR DE MOVIMENTO 360° DE ENCASTRAR
	DETETOR DE MOVIMENTO 180° SALIENTE
	BOTÃO DE PRESSÃO DE ENCASTRAR (A=1,10m)
	BLOCO DE ILUMINAÇÃO DE SEGURANÇA, >1h, 100lm, IP42/65

LEGENDA VIDEOPORTEIRO

	BOTONEIRA VP EXTERIOR
	TRINCO ELÉTRICO
	MONITOR VP INTERIOR
	ALIMENTADOR VP

00	Entrega do Projeto de Execução	30.06.2026
Revisão	Descrição	Data

TUU

Requerente

BRUN
O
EXEM
PLO

Projeto
MBERAL

0000
0-00
2
, COIMBRA

Especialidade
PROJETO DE ELETRICIDADE
PROJETO DE EXECUÇÃO

Designação

ILUMINAÇÃO
PISO 1

JUNHO 2026
1:100

EL008

Observações

ESTE PROJETO DEVERÁ SER LIDO EM CONJUNTO COM AS PEÇAS ESCRITAS, ASSIM COMO, O PROJETO DE ARQUITETURA E AS RESTANTES ESPECIALIDADES.

QUAISQUER DISCREPÂNCIAS DEVERÃO SER COMUNICADAS AO PROJETISTA. TODAS AS MEDIDAS DESTES DESENHOS SÃO DE PROJETO E MERAMENTE INDICATIVAS, NECESSITAM SER RETIFICADAS EM OBRA.

Nome Ficheiro
TUU_MBERAL_PE_ELE_PD_V00.DWG

Código
24932024

Equipa

AN	A	EX	EM	PL	O	
EMANUEL SILVA						ENG ELETROTÉCNICO
						ENG ELETROTÉCNICO

Reprodução proibida, Dec. Lei 45\85 de 17 de DEZEMBRO e código do direito de autor e direitos conexos.

TUU.BUILDING DESIGN MANAGEMENT

arquitetura@tuu.pt www.tuu.pt

LEGENDA:

	QUADRO ELÉTRICO DO EDIFÍCIO
	TOMADA ELÉTRICA 2P+T, 16A, ENCASTRAR
	TOMADA ELÉTRICA 2P+T, 16A, ENCASTRAR, C/TAMPA IP44
	TOMADA ELÉTRICA 2P+T, 16A, ESTANQUE IP65, ENCASTRAR
	TOMADA ELÉTRICA 2P+T, 16A, ESTANQUE IP65, SALIENTE
	TOMADA DE CHÃO ELÉTRICA (2 módulos) 1x 2P+T 16A
	ALIMENTAÇÃO ELÉTRICA ESPECÍFICA
	L1 DOWNLIGHT LED COMPACTO DE ENCASTRAR, 2,5W 3000K IP43 Ø27mm
	L7 APLIQUE DE PAREDE SALIENTE RETANGULAR, LUZ DESCENDENTE E ASCENDENTE
	L8 Placa Superfície LED Quadrada 18W 225x225 mm; Ref. efectLED 407
	L9 LUMINÁRIA LED DE ENCASTRAR BALIZADOR, Ø33mm, 2,5W, 3000K, IP65 IK10
	L14 Plafon LED 20W PHILIPS CL200; Ref. efectLED 85955
	L15 LUMINÁRIA LED DE ENCASTRAR, 5W, 3000K, IP65 IK10
	INTERRUPTOR SIMPLES DE ENCASTRAR (A=1,10m)
	COMUTADOR DE ESCADA DE ENCASTRAR (A=1,10m)
	DETETOR DE MOVIMENTO 360° DE ENCASTRAR
	DETETOR DE MOVIMENTO 180° SALIENTE
	BAP BOTÃO DE PRESSÃO DE ENCASTRAR (A=1,10m)
	BLOCO DE ILUMINAÇÃO DE SEGURANÇA, >1h, 100lm, IP42/65

LEGENDA VIDEOPORTEIRO

	BOTONEIRA VP EXTERIOR
	TRINCO ELÉTRICO
	MONITOR VP INTERIOR
	ALIMENTADOR VP

*AL - Alimentação do Bloco Autónomo feita a partir do circuito de iluminação local

00	Entrega do Projeto de Execução	30.06.2026
Revisão	Descrição	Data

TUU

Requerente

BRUNO
O EXEMPLO

Projeto
MBERAL

000 0-00 2 , COIMBRA
Rua
Ese
mg
03

Especialidade
PROJETO DE ELETRICIDADE
PROJETO DE EXECUÇÃO

Designação

ILUMINAÇÃO
PISO 2

JUNHO 2026
1:100

EL009

Observações

ESTE PROJETO DEVERÁ SER LIDO EM CONJUNTO COM AS PEÇAS
ESCRITAS, ASSIM COMO, O PROJETO DE ARQUITETURA E AS
REstantes ESPECIALIDADES.
QUAISQUER DISCREPÂNCIAS DEVERÃO SER COMUNICADAS AO
PROJETISTA. TODAS AS MEDIDAS DESTES DESENHOS SÃO DE
PROJETO E MERAMENTE INDICATIVAS, NECESSITAM SER
RETIFICADAS EM OBRA.

Nome Ficheiro

TUU_MBERAL_PE_ELE_PD_V00.DWG

Código

24932024

Equipa

ENG ELETROTÉCNICO
EMANUEL SILVA | ENG ELETROTÉCNICO

Reprodução proibida, Dec. Lei 45/85 de 17 de
DEZEMBRO e código do direito de autor e
direitos conexos.

TUU.BUILDING DESIGN MANAGEMENT

arquitetura@tuu.pt

www.tuu.pt



LEGENDA:

	QUADRO ELÉTRICO DO EDIFÍCIO
	TOMADA ELÉTRICA 2P+T, 16A, ENCASTRAR
	TOMADA ELÉTRICA 2P+T, 16A, ENCASTRAR, C/TAMPA IP44
	TOMADA ELÉTRICA 2P+T, 16A, ESTANQUE IP65, ENCASTRAR
	TOMADA ELÉTRICA 2P+T, 16A, ESTANQUE IP65, SALIENTE
	TOMADA DE CHÃO ELETRICIDADE (2 módulos) 1x 2P+T 16A
	ALIMENTAÇÃO ELÉTRICA ESPECÍFICA
	DOWNLIGHT LED COMPACTO DE ENCASTRAR, 2,5W 3000K IP43 Ø27mm
	APLIQUE DE PAREDE SALIENTE RETANGULAR, LUZ DESCENDENTE E ASCENDENTE
	Placa Superfície LED Quadrada 18W 225x225 mm; Ref. efectLED 407
	LUMINÁRIA LED DE ENCASTRAR BALIZADOR, Ø33mm, 2,5W, 3000K, IP65 IK10
	Plafon LED 20W PHILIPS CL200; Ref. efectLED 85955
	LUMINÁRIA LED DE ENCASTRAR, 5W, 3000K, IP65 IK10
	INTERRUPTOR SIMPLES DE ENCASTRAR (A=1,10m)
	COMUTADOR DE ESCADA DE ENCASTRAR (A=1,10m)
	DETETOR DE MOVIMENTO 360° DE ENCASTRAR
	DETETOR DE MOVIMENTO 180° SALIENTE
	BOTÃO DE PRESSÃO DE ENCASTRAR (A=1,10m)
	BLOCO DE ILUMINAÇÃO DE SEGURANÇA, >1h, 100lm, IP42/65

LEGENDA VIDEOPORTEIRO

	BOTONEIRA VP EXTERIOR
	TRINCO ELÉTRICO
	MONITOR VP INTERIOR
	ALIMENTADOR VP

*AL - Alimentação do Bloco Autónomo feita a partir do circuito de iluminação local

00	Entrega do Projeto de Execução	30.06.2026
Revisão	Descrição	Data

TUU

Requerente

BRUNO
O EXEMPLO

Projeto
MBERAL

000 0-00 2 , COIMBRA
Rua
Ese
mp
03

Especialidade
PROJETO DE ELETRICIDADE
PROJETO DE EXECUÇÃO

Designação

ILUMINAÇÃO
PISO 3

JUNHO 2026
1:100

EL010

Observações

ESTE PROJETO DEVERÁ SER LIDO EM CONJUNTO COM AS PEÇAS
ESCRITAS, ASSIM COMO, O PROJETO DE ARQUITETURA E AS
REMANESCENTES ESPECIALIDADES.
QUAISQUER DISCREPÂNCIAS DEVERÃO SER COMUNICADAS AO
PROJETISTA. TODAS AS MEDIDAS DESTES DESENHOS SÃO DE
PROJETO E MERAMENTE INDICATIVAS, NECESSITAM SER
RETIFICADAS EM OBRA.

Nome Ficheiro

TUU_MBERAL_PE_ELE_PD_V00.DWG

Código

24932024

Equipa

ENG ELETROTÉCNICO
EMANUEL SILVA | ENG ELETROTÉCNICO

Reprodução proibida, Dec. Lei 45/85 de 17 de
DEZEMBRO e código do direito de autor e
direitos conexos.

TUU.BUILDING DESIGN MANAGEMENT

arquitetura@tuu.pt

www.tuu.pt

LEGENDA:

	QUADRO ELÉTRICO DO EDIFÍCIO
	TOMADA ELÉTRICA 2P+T, 16A, ENCASTRAR
	TOMADA ELÉTRICA 2P+T, 16A, ENCASTRAR, C/TAMPA IP44
	TOMADA ELÉTRICA 2P+T, 16A, ESTANQUE IP65, ENCASTRAR
	TOMADA ELÉTRICA 2P+T, 16A, ESTANQUE IP65, SALIENTE
	TOMADA DE CHÃO ELETRICIDADE (2 módulos) 1x 2P+T 16A
	ALIMENTAÇÃO ELÉTRICA ESPECÍFICA
	DOWNLIGHT LED COMPACTO DE ENCASTRAR, 2,5W 3000K IP43 Ø27mm
	APLIQUE DE PAREDE SALIENTE RETANGULAR, LUZ DESCENDENTE E ASCENDENTE
	Placa Superfície LED Quadrada 18W 225x225 mm; Ref. efectLED 407
	LUMINÁRIA LED DE ENCASTRAR BALIZADOR, Ø33mm, 2,5W, 3000K, IP65 IK10
	Plafon LED 20W PHILIPS CL200; Ref. efectLED 85955
	LUMINÁRIA LED DE ENCASTRAR, 5W, 3000K, IP65 IK10
	INTERRUPTOR SIMPLES DE ENCASTRAR (A=1,10m)
	COMUTADOR DE ESCADA DE ENCASTRAR (A=1,10m)
	DETETOR DE MOVIMENTO 360° DE ENCASTRAR
	DETETOR DE MOVIMENTO 180° SALIENTE
	BOTÃO DE PRESSÃO DE ENCASTRAR (A=1,10m)
	BLOCO DE ILUMINAÇÃO DE SEGURANÇA, >1h, 100lm, IP42/65

LEGENDA VIDEOPORTEIRO

	BOTONEIRA VP EXTERIOR
	TRINCO ELÉTRICO
	MONITOR VP INTERIOR
	ALIMENTADOR VP

*AL - Alimentação do Bloco Autónomo feita a partir do circuito de iluminação local

00	Entrega do Projeto de Execução	30.06.2026
Revisão	Descrição	Data

TUU

Requerente

BRUN
O EXEM
P.L.O

Projeto
MBERAL

000 0-00 2 , COIMBRA
Rua
Ese
mg
03

Especialidade
PROJETO DE ELETRICIDADE
PROJETO DE EXECUÇÃO

Designação

REDE DE TERRAS
PISO 1

JUNHO 2026
1:100

EL011

Observações

ESTE PROJETO DEVERÁ SER LIDO EM CONJUNTO COM AS PEÇAS
ESCRITAS, ASSIM COMO, O PROJETO DE ARQUITETURA E AS
REMANESCENTES ESPECIALIDADES.
QUAISQUER DISCREPÂNCIAS DEVERÃO SER COMUNICADAS AO
PROJETISTA. TODAS AS MEDIDAS DESTES DESENHOS SÃO DE
PROJETO E MERAMENTE INDICATIVAS, NECESSITAM SER
RETIFICADAS EM OBRA.

Nome Ficheiro

TUU_MBERAL_PE_ELE_PD_V00.DWG

Código

24932024

Equipa

ENG ELETROTÉCNICO
EMANUEL SILVA | ENG ELETROTÉCNICO

Reprodução proibida, Dec. Lei 45/85 de 17 de
DEZEMBRO e código do direito de autor e
direitos conexos.

TUU.BUILDING DESIGN MANAGEMENT

arquitetura@tuu.pt

www.tuu.pt

LEGENDA:

	QUADRO ELÉTRICO DO EDIFÍCIO
	TOMADA ELÉTRICA 2P+T, 16A, ENCASTRAR
	TOMADA ELÉTRICA 2P+T, 16A, ENCASTRAR, C/TAMPA IP44
	TOMADA ELÉTRICA 2P+T, 16A, ESTANQUE IP65, ENCASTRAR
	TOMADA ELÉTRICA 2P+T, 16A, ESTANQUE IP65, SALIENTE
	TOMADA DE CHÃO ELETRICIDADE (2 módulos) 1x 2P+T 16A
	ALIMENTAÇÃO ELÉTRICA ESPECÍFICA
	DOWLIGHT LED COMPACTO DE ENCASTRAR, 2,5W 3000K IP43 Ø27mm
	APLIQUE DE PAREDE SALIENTE RETANGULAR, LUZ DESCENDENTE E ASCENDENTE
	Placa Superfície LED Quadrada 18W 225x225 mm; Ref. efectoLED 407
	LUMINÁRIA LED DE ENCASTRAR BALIZADOR, Ø33mm, 2,5W, 3000K, IP65 IK10
	Plafon LED 20W PHILIPS CL200; Ref. efectoLED 85955
	LUMINÁRIA LED DE ENCASTRAR, 5W, 3000K, IP65 IK10
	INTERRUPTOR SIMPLES DE ENCASTRAR (A=1,10m)
	COMUTADOR DE ESCADA DE ENCASTRAR (A=1,10m)
	DETETOR DE MOVIMENTO 360° DE ENCASTRAR
	DETETOR DE MOVIMENTO 180° SALIENTE
	BOTÃO DE PRESSÃO DE ENCASTRAR (A=1,10m)
	BLOCO DE ILUMINAÇÃO DE SEGURANÇA, >1h, 100lm, IP42/65

LEGENDA VIDEOPORTEIRO

	BOTONEIRA VP EXTERIOR
	TRINCO ELÉTRICO
	MONITOR VP INTERIOR
	ALIMENTADOR VP



00	Entrega do Projeto de Execução	30.06.2026
Revisão	Descrição	Data

TUW

Requerente

BRUN
C
EXEM
DProjeto
MBERAL

00000
00000
2
, COIMBRA

Especialidade
PROJETO DE ELETRICIDADE
PROJETO DE EXECUÇÃO

Designação

VIDEOPORTEIRO
PISO 1

JUNHO 2026
1:100

EL012

Observações
ESTE PROJETO DEVERÁ SER LIDO EM CONJUNTO COM AS PEÇAS ESCRITAS, ASSIM COMO, O PROJETO DE ARQUITETURA E AS RESTANTES ESPECIALIDADES.
QUAISQUER DISCREPÂNCIAS DEVERÃO SER COMUNICADAS AO PROJETISTA. TODAS AS MEDIDAS DESTES DESENHO SÃO DE PROJETO E MERAMENTE INDICATIVAS, NECESSITAM SER RETIFICADAS EM OBRA.

Nome Ficheiro
TUU_MBERAL_PE_ELE_PD_V00.DWG

Código
24932024

Equipa

AN	A	EX	EM	PL	O		ENG ELETROTÉCNICO
EMANUEL SILVA							ENG ELETROTÉCNICO

Reprodução proibida, Dec. Lei 45\85 de 17 de
DEZEMBRO e código do direito de autor e
direitos conexos.

TUU.BUILDING DESIGN MANAGEMENT

arquitetura@tuu.pt www.tuu.pt

LEGENDA:

	QUADRO ELÉTRICO DO EDIFÍCIO
	TOMADA ELÉTRICA 2P+T, 16A, ENCASTRAR
	TOMADA ELÉTRICA 2P+T, 16A, ENCASTRAR, C/TAMPA IP44
	TOMADA ELÉTRICA 2P+T, 16A, ESTANQUE IP65, ENCASTRAR
	TOMADA ELÉTRICA 2P+T, 16A, ESTANQUE IP65, SALIENTE
	TOMADA DE CHÃO ELÉTRICIDADE (2 módulos) 1x 2P+T 16A
	ALIMENTAÇÃO ELÉTRICA ESPECÍFICA
	L _{L1} DOWNLIGHT LED COMPACTO DE ENCASTRAR, 2,5W 3000K IP43 Ø27mm
	L _{L7} APLIQUE DE PAREDE SALIENTE RETANGULAR, LUZ DESCENDENTE E ASCENDENTE
	L _{L8} Placa Superfície LED Quadrada 18W 225x225 mm; Ref. efectoLED 407
	L _{L9} LUMINÁRIA LED DE ENCASTRAR BALIZADOR, Ø33mm, 2,5W, 3000K, IP65 IK10
	L _{L14} Plafon LED 20W PHILIPS CL200; Ref. efectoLED 85955
	L _{L15} LUMINÁRIA LED DE ENCASTRAR, 5W, 3000K, IP65 IK10
	INTERRUPTOR SIMPLES DE ENCASTRAR (A=1,10m)
	COMUTADOR DE ESCADA DE ENCASTRAR (A=1,10m)
	DETETOR DE MOVIMENTO 360° DE ENCASTRAR
	DETETOR DE MOVIMENTO 180° SALIENTE
	BOTÃO DE PRESSÃO DE ENCASTRAR (A=1,10m)
	BLOCO DE ILUMINAÇÃO DE SEGURANÇA, >1h, 100lm, IP42/65

LEGENDA VIDEOPORTEIRO

 Botoneira VP	BOTONEIRA VP EXTERIOR
	TRINCO ELÉTRICO
 VP	MONITOR VP INTERIOR
	ALIMENTADOR VP

00	Entrega do Projeto de Execução	30.06.2026
Revisão	Descrição	Data

TUU

Requerente

BRUNO EXEMPLO

Projeto
MBERAL

Especialidade
PROJETO DE ELETRICIDADE
PROJETO DE EXECUÇÃO

Designação

VIDEOPORTEIRO
PISO 2

JUNHO 2026
1:100

EL013

Observações

ESTE PROJETO DEVERÁ SER LIDO EM CONJUNTO COM AS PEÇAS ESCRITAS, ASSIM COMO, O PROJETO DE ARQUITETURA E AS RESTANTES ESPECIALIDADES. QUAISQUER DISCREPÂNCIAS DEVERÃO SER COMUNICADAS AO PROJETISTA. TODAS AS MEDIDAS DESTES DESENHO SÃO DE PROJETO E MERAMENTE INDICATIVAS, NECESSITAM SER RETIFICADAS EM OBRA.

Nome Ficheiro

TUU_MBERAL_PE_ELE_PD_V00.DWG

Código

24932024

Equipa

MANUEL SILVA | ENG ELETROTÉCNICO
EMANUEL SILVA | ENG ELETROTÉCNICO

Reprodução proibida, Dec. Lei 45/85 de 17 de DEZEMBRO e código do direito de autor e direitos conexos.

TUU.BUILDING DESIGN MANAGEMENT

arquitetura@tuu.pt

www.tuu.pt

LEGENDA:

	QUADRO ELÉTRICO DO EDIFÍCIO
	TOMADA ELÉTRICA 2P+T, 16A, ENCASTRAR
	TOMADA ELÉTRICA 2P+T, 16A, ENCASTRAR, C/TAMPA IP44
	TOMADA ELÉTRICA 2P+T, 16A, ESTANQUE IP65, ENCASTRAR
	TOMADA ELÉTRICA 2P+T, 16A, ESTANQUE IP65, SALIENTE
	TOMADA DE CHÃO ELETRICIDADE (2 módulos) 1x 2P+T 16A
	ALIMENTAÇÃO ELÉTRICA ESPECÍFICA
	DOWNLIGHT LED COMPACTO DE ENCASTRAR, 2,5W 3000K IP43 Ø27mm
	APLIQUE DE PAREDE SALIENTE RETANGULAR, LUZ DESCENDENTE E ASCENDENTE
	Placa Superfície LED Quadrada 18W 225x225 mm; Ref. efectLED 407
	LUMINÁRIA LED DE ENCASTRAR BALIZADOR, Ø33mm, 2,5W, 3000K, IP65 IK10
	Plafon LED 20W PHILIPS CL200; Ref. efectLED 85955
	LUMINÁRIA LED DE ENCASTRAR, 5W, 3000K, IP65 IK10
	INTERRUPTOR SIMPLES DE ENCASTRAR (A=1,10m)
	COMUTADOR DE ESCADA DE ENCASTRAR (A=1,10m)
	DETETOR DE MOVIMENTO 360° DE ENCASTRAR
	DETETOR DE MOVIMENTO 180° SALIENTE
	BOTÃO DE PRESSÃO DE ENCASTRAR (A=1,10m)
	BLOCO DE ILUMINAÇÃO DE SEGURANÇA, >1h, 100lm, IP42/65

LEGENDA VIDEOPORTEIRO

	BOTONEIRA VP EXTERIOR
	TRINCO ELÉTRICO
	MONITOR VP INTERIOR
	ALIMENTADOR VP



00	Entrega do Projeto de Execução	30.06.2026
Revisão	Descrição	Data

TUU

Requerente

BRUNO EXEMPLO

Projeto
MBERAL

Rua Eng. João de Deus, 100
3000-000, COIMBRA

Especialidade
PROJETO DE ELETRICIDADE
PROJETO DE EXECUÇÃO

Designação

VIDEOPORTEIRO
PISO 3

JUNHO 2026
1:100

EL014

Observações

ESTE PROJETO DEVERÁ SER LIDO EM CONJUNTO COM AS PEÇAS ESCRITAS, ASSIM COMO, O PROJETO DE ARQUITETURA E AS RESTANTES ESPECIALIDADES.
QUAISQUER DISCREPÂNCIAS DEVERÃO SER COMUNICADAS AO PROJETISTA. TODAS AS MEDIDAS DESTES DESENHO SÃO DE PROJETO E MERAMENTE INDICATIVAS, NECESSITAM SER RETIFICADAS EM OBRA.

Nome Ficheiro

TUU_MBERAL_PE_ELE_PD_V00.DWG

Código

24932024

Equipa

MANUEL SILVA | ENG ELETROTÉCNICO
EMANUEL SILVA | ENG ELETROTÉCNICO

Reprodução proibida, Dec. Lei 45/85 de 17 de DEZEMBRO e código do direito de autor e direitos conexos.

TUU.BUILDING DESIGN MANAGEMENT

arquitetura@tuu.pt

www.tuu.pt

LEGENDA:

	QUADRO ELÉTRICO DO EDIFÍCIO
	TOMADA ELÉTRICA 2P+T, 16A, ENCASTRAR
	TOMADA ELÉTRICA 2P+T, 16A, ENCASTRAR, C/TAMPA IP44
	TOMADA ELÉTRICA 2P+T, 16A, ESTANQUE IP65, ENCASTRAR
	TOMADA ELÉTRICA 2P+T, 16A, ESTANQUE IP65, SALIENTE
	TOMADA DE CHÃO ELETRICIDADE (2 módulos) 1x 2P+T 16A
	ALIMENTAÇÃO ELÉTRICA ESPECÍFICA
	DOWNLIGHT LED COMPACTO DE ENCASTRAR, 2,5W 3000K IP43 Ø27mm
	APLIQUE DE PAREDE SALIENTE RETANGULAR, LUZ DESCENDENTE E ASCENDENTE
	Placa Superfície LED Quadrada 18W 225x225 mm; Ref. efectLED 407
	LUMINÁRIA LED DE ENCASTRAR BALIZADOR, Ø33mm, 2,5W, 3000K, IP65 IK10
	Piafon LED 20W PHILIPS CL200; Ref. efectLED 85955
	LUMINÁRIA LED DE ENCASTRAR, 5W, 3000K, IP65 IK10
	INTERRUPTOR SIMPLES DE ENCASTRAR (A=1,10m)
	COMUTADOR DE ESCADA DE ENCASTRAR (A=1,10m)
	DETETOR DE MOVIMENTO 360° DE ENCASTRAR
	DETETOR DE MOVIMENTO 180° SALIENTE
	BOTÃO DE PRESSÃO DE ENCASTRAR (A=1,10m)
	BLOCO DE ILUMINAÇÃO DE SEGURANÇA, >1h, 100lm, IP42/65

LEGENDA VIDEOPORTEIRO

	BOTONEIRA VP EXTERIOR
	TRINCO ELÉTRICO
	MONITOR VP INTERIOR
	ALIMENTADOR VP



PODER DE CORTE DOS DISJUNTORES
NÃO INFERIOR A 50A (IEC-10883-1)

A CAIXA EXTERIOR DO QUADRO DE
CLASSE II DE ISOLAMENTO

Q.E.G.(N)

Classe II
IP42 IK04
Icc = 6kA

Da Portinhola
RV-K - 4x16mm²

3F+N, 230/400V
50Hz, In=50A

NºCirc.	Fase	Pot. (VA)	CANALIZAÇÃO	DESTINO
IL1	L1	---	3x H07V-K 15mm ²	Illumin. Circulações - I1.1, I1.2
IS1	L1	---	3x H07V-K 15mm ²	Illuminação Segurança
IL2	L1	---	3x H07V-K 15mm ²	Illumin. Circulações - I2.1, I2.2, I2.3
IS2	L1	---	3x H07V-K 15mm ²	Illuminação Segurança
IL3	L1	---	3x H07V-K 15mm ²	Illumin. Circulações - I3.1
IS3	L1	---	3x H07V-K 15mm ²	Illuminação Segurança
T3	L1	---	3x H07V-K 2,5mm ²	Vídeo Porteiro
T3	L1	---	3x H07V-K 2,5mm ²	ATI
				Reserva Não Equipada
				Reserva Não Equipada
ALE1	L2	---	3x H07V-K 10mm ²	Alimentação Q.P.1.1
ALE2	L2	---	3x H07V-K 10mm ²	Alimentação Q.P.1.2
ALE3	L3	---	3x H07V-K 10mm ²	Alimentação Q.P.2.1
ALE4	L3	---	3x H07V-K 10mm ²	Alimentação Q.P.2.2
ALE5	L1	---	3x H07V-K 10mm ²	Alimentação Q.P.3.1
				Reserva Não Equipada

Diagrama de distribuição elétrica para o apartamento 111, Classe II, IP42 IK04, Icc = 6kA.

Legenda:

- PODER DE CORTE DOS DISJUNTORES RACHAVERS 4x4 KALCIC 088-1
- A CAIXA EXTERIOR DO QUADRO DE CLASSE II DE ISOLAMENTO

Q.P.1.1

Classe II
IP42 IK04
Icc = 6kA

Do Q.E.G.
3x H07V-K 10mm²

1F+N, 230V
50Hz; In=32A

Diagrama de Distribuição:

O diagrama mostra a distribuição de energia para 10 circuitos (Nº Circ. 1 a 10). Cada circuito é protegido por um disjuntor de 25A 30kA na entrada e por disjuntores de 16A 10kA nas ramificações. Os circuitos são:

- Circuitos 1 a 4 (Canalização):** IL1 (3x H07V-K 1,5mm²), IL2 (3x H07V-K 1,5mm²), IL3 (Reserva Não Equipada), IL4 (Reserva Não Equipada).
- Circuitos 5 a 8 (Tomadas):** T1 (Tomadas Iso Geral - T1, 3x H07V-K 2,5mm²), T2 (Tomadas Iso Geral - T2, 3x H07V-K 2,5mm²), T3 (Tomadas Iso Geral Cozinha, 3x H07V-K 2,5mm²), T4 (Reserva Não Equipada).
- Circuitos 9 a 10 (Outros):** ALE1 (Forno, 3x H07V-K 4mm²), ALE2 (Placa de Indução, 3x H07V-K 4mm²), ALE3 (Tomada Exaustor, 3x H07V-K 2,5mm²), ALE4 (Tomadas Frigorífico, 3x H07V-K 2,5mm²), ALE5 (Tomada Máquina Lavar Roupa, 3x H07V-K 2,5mm²), ALE6 (Reserva Não Equipada), ALE7 (Termoacumulador Elétrico 180L, RV-K 3G52,5mm²), ALE8 (Unidade Exterior 1, RV-K 3G52,5mm²), ALE9 (Ventilador de Extração 1, 3x H07V-K 1,5mm²), ALE10 (Forno Doméstico 1, 3x H07V-K 1,5mm²).

Tabela de Dados:

Nº Circ.	Fase	Pot. (VA)	CANALIZAÇÃO	DESTINO
1	L2	---	IL1 3x H07V-K 1,5mm ²	Iluminação - IT1, IT2
2	L2	---	IL2 3x H07V-K 1,5mm ²	Iluminação - IZ1, IZ2
3	L2	---	IL3 ---	Reserva Não Equipada
4	L2	---	IL4 ---	Reserva Não Equipada
5	L2	---	T1 3x H07V-K 2,5mm ²	Tomadas Iso Geral - T1
6	L2	---	T2 3x H07V-K 2,5mm ²	Tomadas Iso Geral - T2
7	L2	---	T3 3x H07V-K 2,5mm ²	Tomadas Iso Geral Cozinha
8	L2	---	T4 ---	Reserva Não Equipada
9	L2	---	ALE1 3x H07V-K 4mm ²	Forno
10	L2	---	ALE2 3x H07V-K 4mm ²	Placa de Indução
11	L2	---	ALE3 3x H07V-K 2,5mm ²	Tomada Exaustor
12	L2	---	ALE4 3x H07V-K 2,5mm ²	Tomadas Frigorífico
13	L2	---	ALE5 3x H07V-K 2,5mm ²	Tomada Máquina Lavar Roupa
14	L2	---	ALE6 ---	Reserva Não Equipada
15	L2	---	ALE7 RV-K 3G52,5mm ²	Termoacumulador Elétrico 180L
16	L2	---	ALE8 RV-K 3G52,5mm ²	Unidade Exterior 1
17	L2	---	ALE9 3x H07V-K 1,5mm ²	Ventilador de Extração 1
18	L2	---	ALE10 3x H07V-K 1,5mm ²	Forno Doméstico 1

Q.P.1.2
 Classe II
 IP42 IK04
 Icc = 6kA

PODER DE CORTE DOS DISJUNTORES
 NÃO SUPERAR A VAL. ABAIXO (1)
 A CAIXA EXTERIOR DO QUADRO DE
 CLASSE II DE ISOLAMENTO

Do D.E.G.
 3x H07V-K 10mm²
 60A

1F+N, 230V
 50Hz, In=32A

25A 30mA
 25A 30mA
 25A 30mA
 25A 30mA
 25A 30mA
 25A 30mA

10A
 10A
 16A
 16A
 16A
 16A
 16A
 16A
 16A
 10A
 10A

NºCirc.	IL1	IL2	IL3	T1	T2	T3	T4	ALE1	ALE2	ALE3	ALE4	ALE5	ALE6	ALE7	ALE8	ALE9	ALE10
Fase	L2	L2	L2	L2	L2	L2	L2	L2	L2	L2	L2	L2	L2	L2	L2	L2	L2
Pot. (VA)	---	---	---	---	---	---	---	---	---	---	---	---	---	---	---	---	---
CANALIZAÇÃO	3x H07V-K 1,5mm ²	3x H07V-K 1,5mm ²		3x H07V-K 2,5mm ²	3x H07V-K 2,5mm ²	3x H07V-K 2,5mm ²		3x H07V-K 4mm ²	3x H07V-K 4mm ²	3x H07V-K 2,5mm ²	3x H07V-K 2,5mm ²	3x H07V-K 2,5mm ²		RV-K 3G52,5mm ²	RV-K 3G52,5mm ²	3x H07V-K 1,5mm ²	3x H07V-K 1,5mm ²
DESTINO	Iluminação - IT1, IT2	Iluminação - IZ1, IZ2	Reserva Não Equipada	Tomadas Uso Geral - T1	Tomadas Uso Geral - T2	Tomadas Uso Geral Cozinha	Reserva Não Equipada	Forno	Placa de Indução	Tomada Esvafor	Tomadas Fingerprint	Tomada Máquina Lavar-Roupa	Reserva Não Equipada	Termoacumulador Elétrico 2 80L	Unidade Exterior 2	Ventilador de Extração 2	Hotte Doméstico 2

00	Entrega do Projeto de Execução	30.06.2026
Revisão	Descrição	Data

TUW

Requerente

BRUN
O
EXEM
PLO

Projeto
MBERAL

0000
00-00
2, COIMBRA
Rua
Exe
mpl

Especialidade

PROJETO DE ELETRICIDADE
PROJETO DE EXECUÇÃO

Designação

ESQUEMAS DOS QUADROS ELÉTRICOS

JUNHO 2026

S/ESCALA

EL015

Observações

ESTE PROJETO DEVERÁ SER LIDO EM CONJUNTO COM AS PEÇAS ESCRITAS, ASSIM COMO, O PROJETO DE ARQUITETURA E AS RESTANTES ESPECIALIDADES.

QUAISQUER DISCREPÂNCIAS DEVERÃO SER COMUNICADAS AO
PROJETISTA. TODAS AS MEDIDAS DESTES DESENHOS SÃO DE
PROJETO E MERAMENTE INDICATIVAS, NECESSITAM SER
RETIFICADAS EM OBRA.

Nome Ficheiro

TUU_MBERAL PE_ELE_PD_V00.DWG

Código

24932024

Equipa

ANEXO | ENG ELETROTÉCNICO
EMANUEL SILVA | ENG ELETROTÉCNICO


Reprodução proibida, Dec. Lei 45\85 de 17 de DEZEMBRO e código do direito de autor e direitos conexos.

TUU.BUILDING DESIGN MANAGEMENT


arquitetura@tuu.pt

www.tuu.pt


Quadro Parcial 2.1

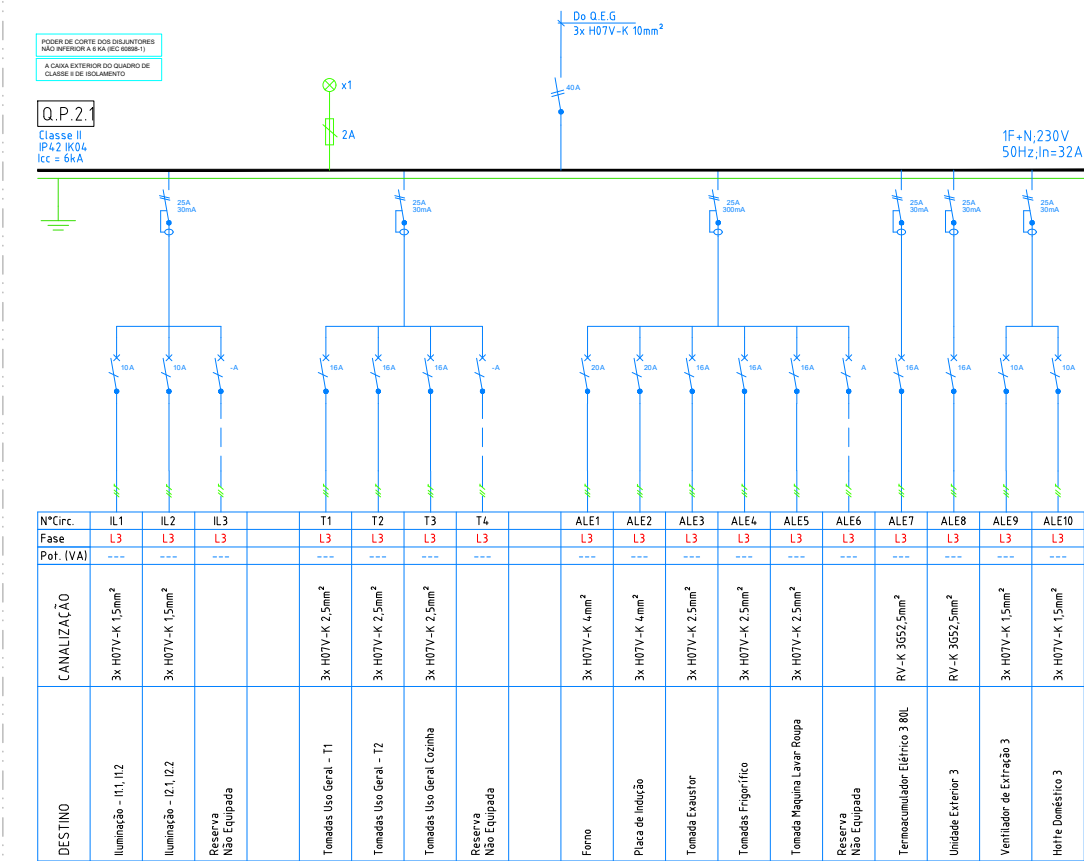

Quadro Parcial 2.2

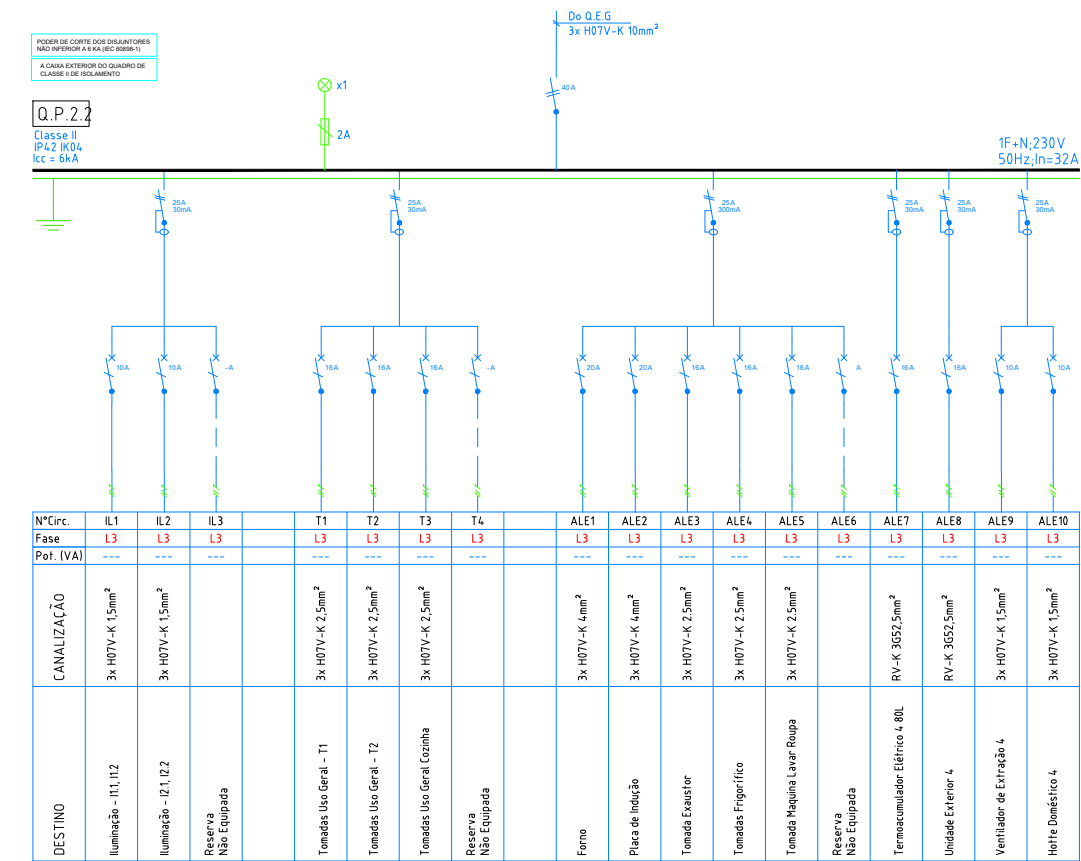

Quadro Parcial 3.1

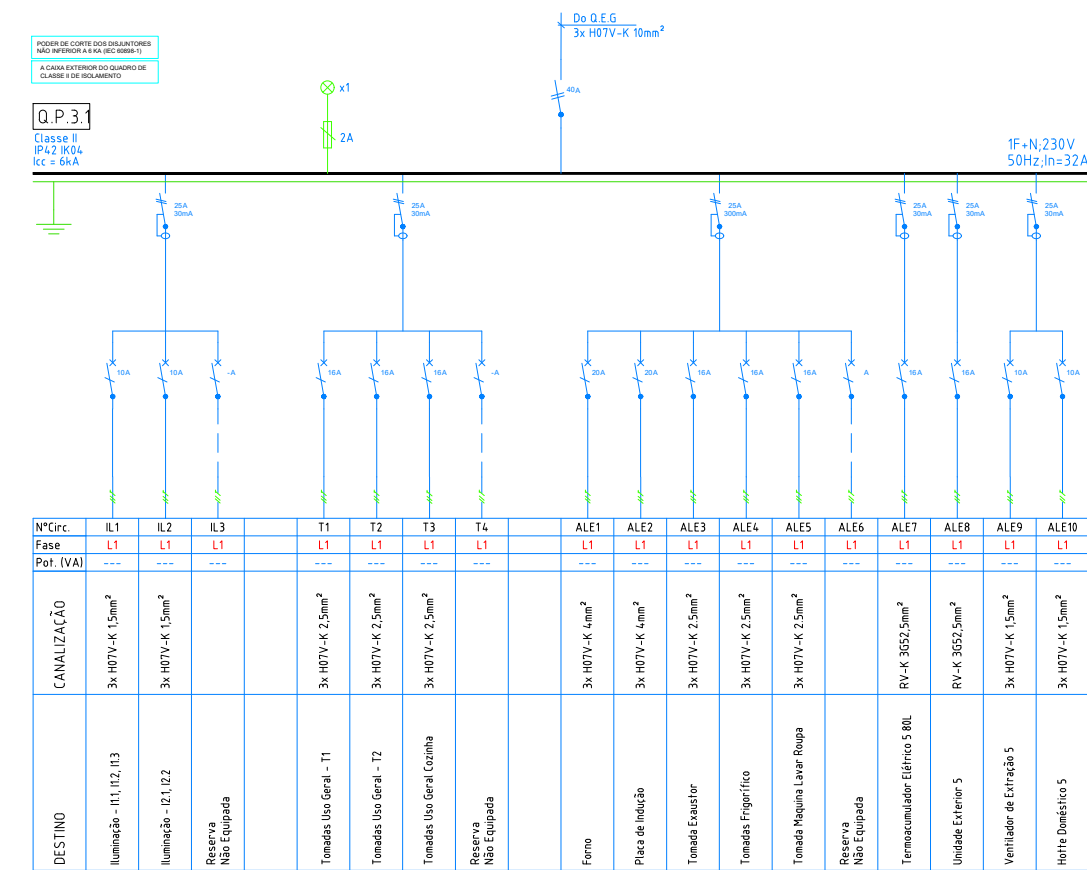

TUU

Requerente

BRUNO
O EXEMPLO

Projeto
MBERAL

000 0-00 2 , COIMBRA

Especialidade

PROJETO DE ELETRICIDADE
PROJETO DE EXECUÇÃO

Designação

ESQUEMAS DOS QUADROS
ELÉTRICOS

JUNHO 2026
S/ESCALA

EL016

Observações

ESTE PROJETO DEVERÁ SER LIDO EM CONJUNTO COM AS PEÇAS ESCRITAS, ASSIM COMO, O PROJETO DE ARQUITETURA E AS RESTANTES ESPECIALIDADES.
QUAISQUER DISCREPÂNCIAS DEVERÃO SER COMUNICADAS AO PROJETISTA. TODAS AS MEDIDAS DESTES DESENHOS SÃO DE PROJETO E MERAMENTE INDICATIVAS, NECESSITAM SER RETIFICADAS EM OBRA.

Nome Ficheiro

TUU_MBERAL_PE_ELE_PD_V00.DWG

Código

24932024

Equipa

AN & E T O | ENG ELETROTÉCNICO
EMANUEL SILVA | ENG ELETROTÉCNICO

Reprodução proibida, Dec. Lei 45/85 de 17 de
DEZEMBRO e código do direito de autor e
direitos conexos.

TUU.BUILDING DESIGN MANAGEMENT

arquitetura@tuu.pt

www.tuu.pt