

ÍNDICE

	TÍTULO	DATA	REV
001	PLANTA PISO 0 - DISTRIB. ENERGIA	01/26	-
002	PLANTA PISO -1 - DISTRIB. ENERGIA	01/26	-
003	PLANTA PISO 0 - CAMINHOS DE CABOS	01/26	-
004	PLANTA PISO -1 - CAMINHOS DE CABOS	01/26	-
005	PLANTA PISO 0 - ALIMENTAÇÕES ESPECÍFICAS	01/26	-
006	PLANTA PISO -1 - ALIMENTAÇÕES ESPECÍFICAS	01/26	-
007	PLANTA PISO 0 - TOMADAS	01/26	-
008	PLANTA PISO -1 - TOMADAS	01/26	-
009	PLANTA PISO 0 - TOMADAS ESTABILIZADAS (UPS)	01/26	-
010	PLANTA PISO -1 - TOMADAS ESTABILIZADAS (UPS)	01/26	-
011	PLANTA PISO 0 - ILUMINAÇÃO E BUS DALI	01/26	-
012	PLANTA PISO -1 - ILUMINAÇÃO E BUS DALI	01/26	-
013	PLANTA PISO 0 - EQUIPAMENTOS E BUS KNX	01/26	-
014	PLANTA PISO -1 - EQUIPAMENTOS E BUS KNX	01/26	-
015	PLANTA PISO 0 - ILUMINAÇÃO DE EMERGÊNCIA	01/26	-
016	PLANTA PISO -1 - ILUMINAÇÃO DE EMERGÊNCIA	01/26	-
017	PLANTA PISO 0 - SADI	01/26	-
018	PLANTA PISO -1 - SADI	01/26	-
019	PLANTA COBERTURA - FOTOVOLTAICO	01/26	-
020	PLANTA PISO 0 - FOTOVOLTAICO	01/26	-
021	ESQUEMAS FOTOVOLTAICOS	01/26	-
022	DIAGRAMA DA REDE ELÉTRICA	01/26	-
023	ESQUEMA DE PRINCIPIO SISTEMA AUDIOVISUAL	01/26	-
024	ESQUEMAS QUADROS ELÉTRICOS	01/26	-
025	ESQUEMAS QUADROS ELÉTRICOS	01/26	-
026	ESQUEMAS QUADROS ELÉTRICOS	01/26	-
027	DIAGRAMA DO SISTEMA KNX	01/26	-
028		01/26	-
029		01/26	-
030		01/26	-



Requerente
CÂMARA MUNICIPAL DE CANTANHEDE
Projeto
REQUALIFICAÇÃO E MODERNIZAÇÃO DA BIBLIOTECA MUNICIPAL DE CANTANHEDE

RUA EXEMPLO 11
0000-004 CANTANHEDE

Especialidade
PROJETO DA INSTALAÇÃO ELÉTRICA

PROJETO DE EXECUÇÃO

Designação
ÍNDICE

-

JANEIRO 2026
1:100

000

Observações
ESTE PROJETO DEVERÁ SER LIDO EM CONJUNTO COM AS PEÇAS ESCRITAS, ASSIM COMO, O PROJETO DE ARQUITETURA E AS RESTANTES ESPECIALIDADES.
QUAISQUER DISCREPÂNCIAS DEVERÃO SER COMUNICADAS AO PROJETISTA. TODAS AS MEDIDAS DESTES DESENHO SÃO DE PROJETO E MERAMENTE INDICATIVAS, NECESSITAM SER RETIFICADAS EM OBRA.


Nome Ficheiro
BIBLICA_PE_ELE_PD_V0.DWG

Código
39962025

Equipa
ANA EXEMPLO | **ENG ELETROTÉCNICO**
LUIS BALSAS | **ENG ELETROTÉCNICO**

Reprodução proibida, Dec. Lei 45/85 de 17 de Setembro e código do direito de autor e direitos conexos.

TUU.BUILDING DESIGN MANAGEMENT
arquitetura@tuu.pt www.tuu.pt

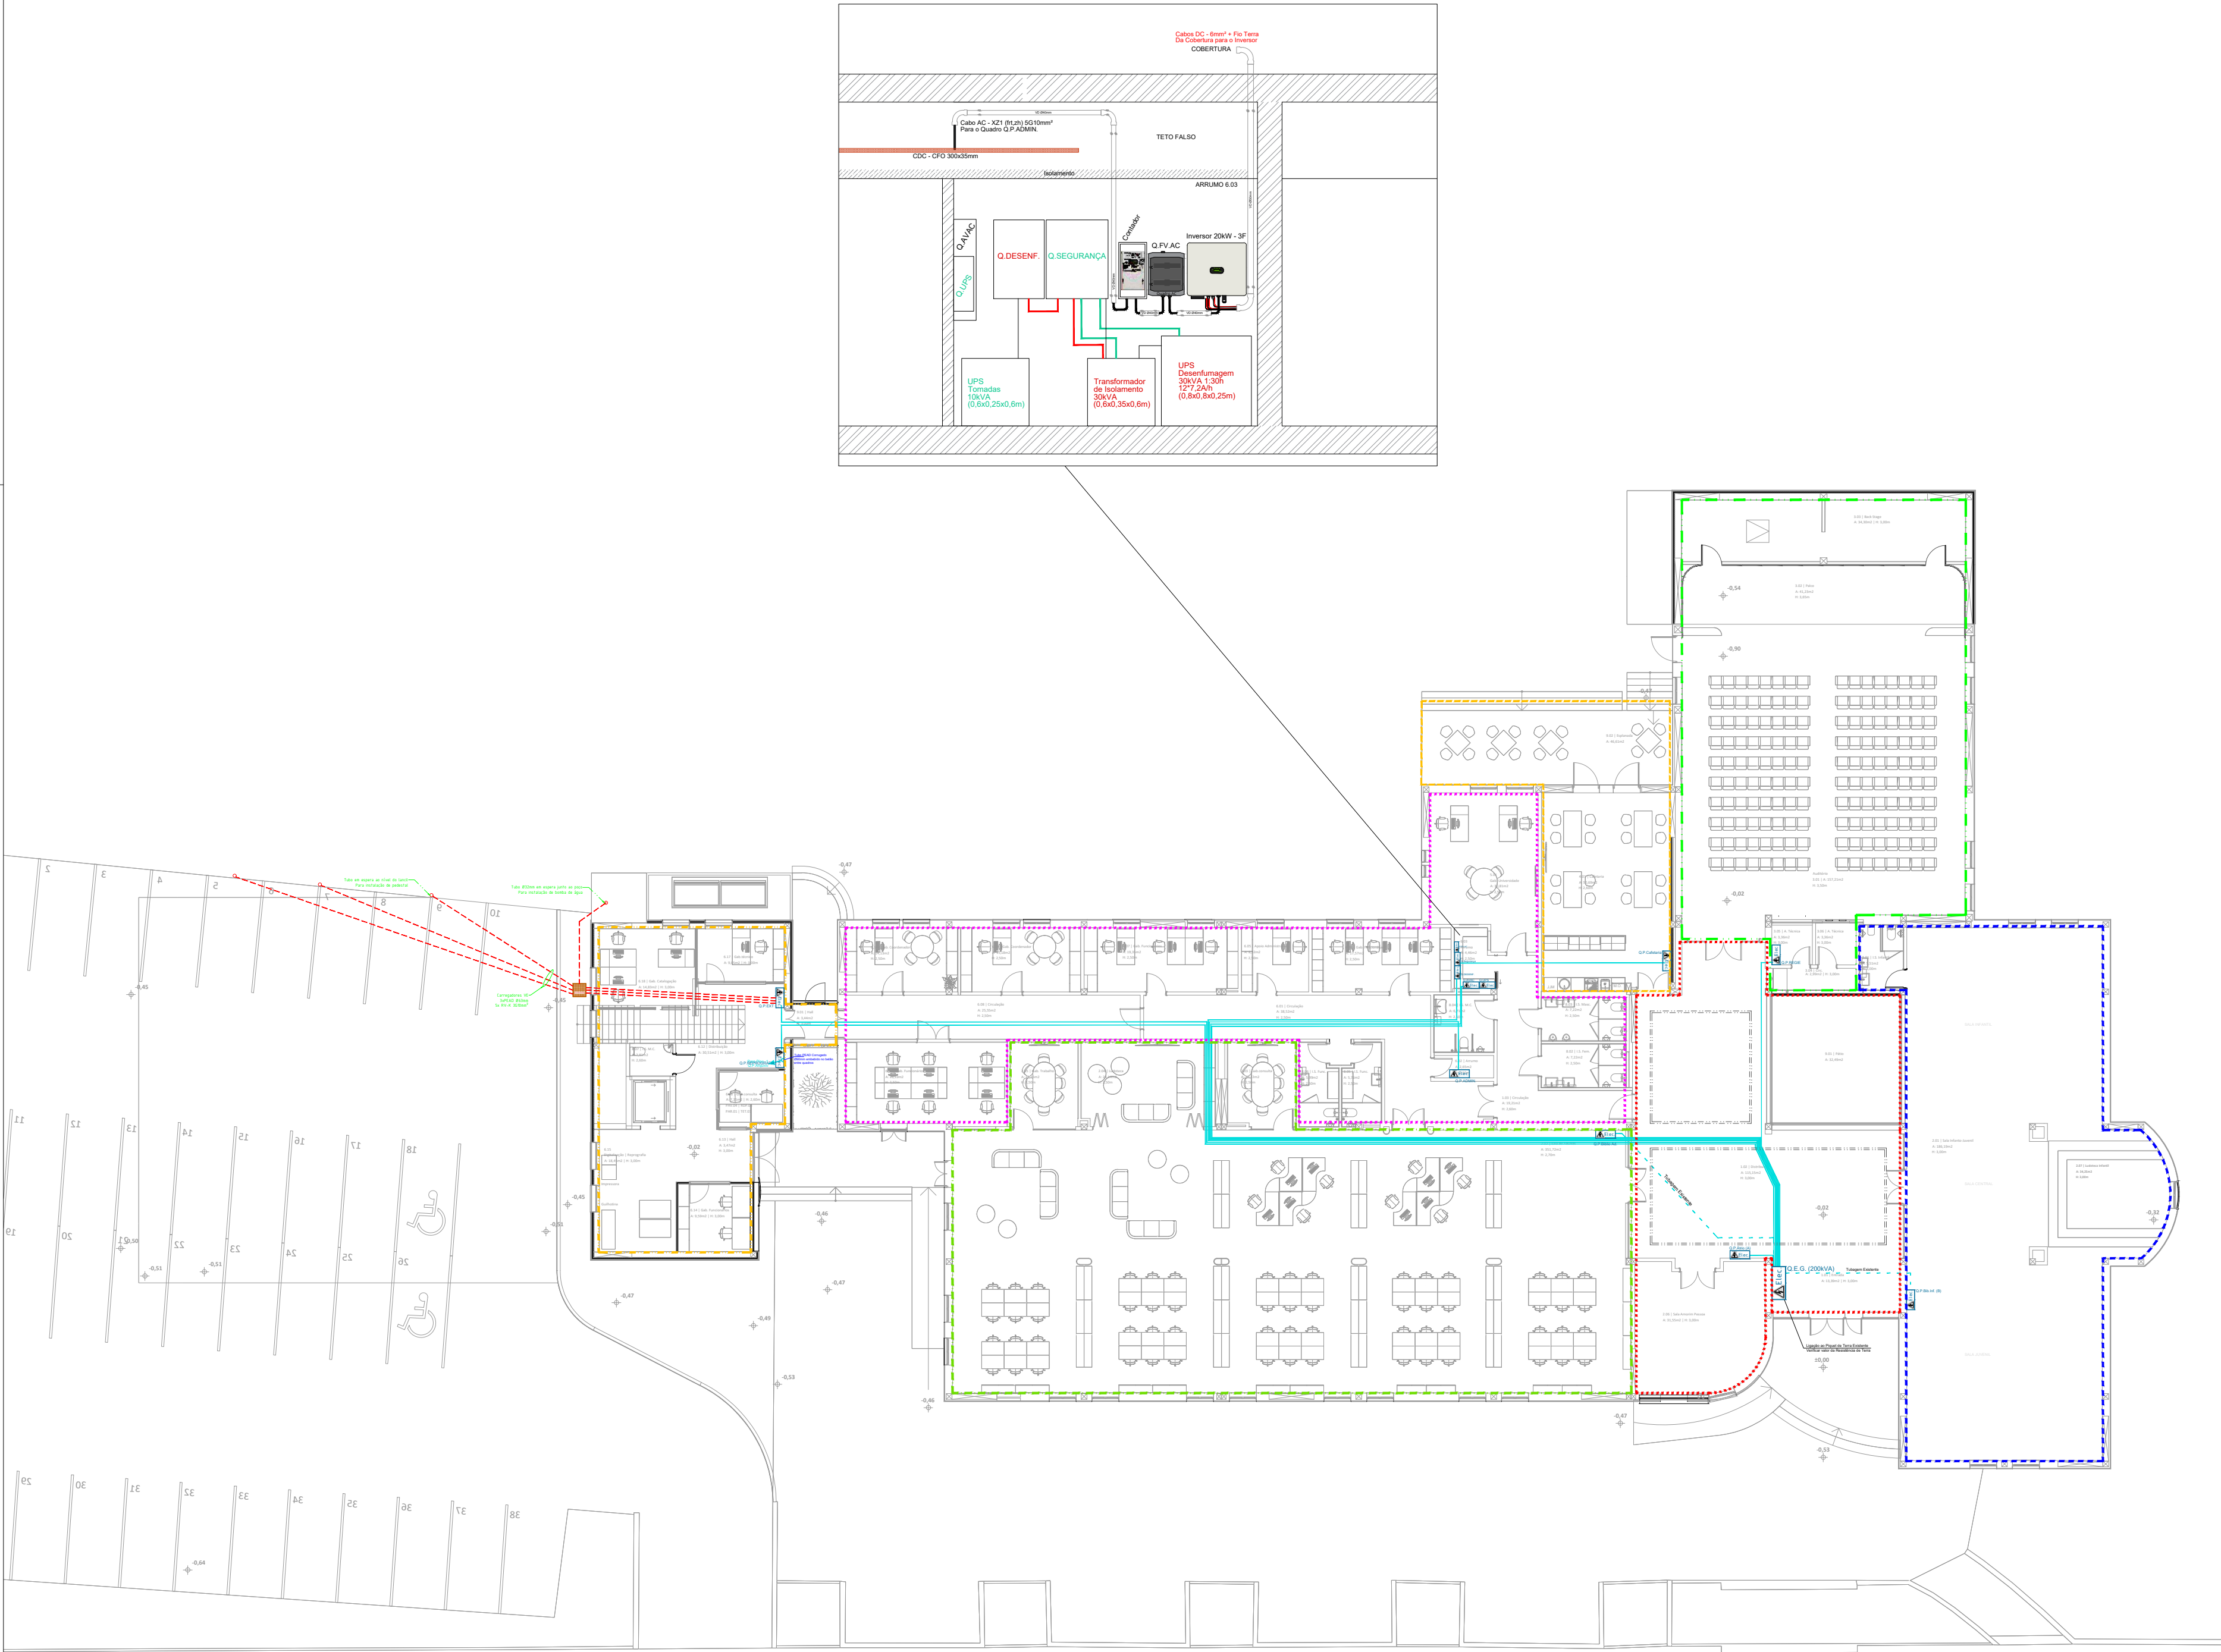

LEGENDA:		
	QUADRO ELÉTRICO DO EDIFÍCIO	
	TOMADA ELÉTRICA 2P+T, 16A, USOS GERAIS - ENCASTRAR	
	TOMADA ELÉTRICA 2P+T, 16A, ESTANQUE IP55 - ENCASTRAR	
	TOMADA ELÉTRICA 2P+T, 16A, ENCASTRAR, C/TAMPA IP44	
	TOMADA ELÉTRICA 2P+T, 16A, ESTANQUE IP55 - SALIENTE	
	CAIXA DE CHÃO 2 MÓDULOS (1xTOM 2P+T)	
	CAIXA DE CHÃO DE 12 MÓDULOS (3xTOM 2P+T + 2xTOM 2P+T (UPS) + 2xRL45 Cat6)	
	ALIMENTAÇÃO ELÉTRICA ESPECÍFICA DE EQUIPAMENTO	
	(Dimensões e altura, ver planta!)	
	BLOCO AUTÔNOMO PERMANENTE	
	BLOCO AUTÔNOMO NÃO PERMANENTE	
	LUMINÁRIA DE ENCASTRAR NO TETO, DO TIPO TROMMILUX, SÉRIE 4556 DALI, DIMENSÃO L1=1975mm, L5 1x1300 ou L5,2=1000mm, 4000K	
	LUMINÁRIA SUSPENSÃO DE TETO, DO TIPO TROMMILUX, SÉRIE 4556 DALI, DIMENSÃO 1975mm, 4000K	
	LUMINÁRIA SALIENTE DE PAREDE, DO TIPO TROMMILUX, SÉRIE 4028, DIMENSÃO 1220mm, NA VERTICAL, 4000K	
	LUMINÁRIA DO TIPO PANEL LED, DE ENCASTRAR NO TETO, TROMMILUX, SÉRIE 5550 DALI, 595x595mm, 30W 4000K (P30 R02)	
	LUMINÁRIA DE ENCASTRAR COM ABA DE REMATE, DO TIPO TROMMILUX, SÉRIE 5511 DALI, DIMENSÃO 965mm, 4000K	
	LUMINÁRIA SUSPENSÃO DE TETO LINEAR, TROMMILUX, DA SÉRIE 4052, 4000K	
	LUMINÁRIA DE ENCASTRAR NO TETO, DO TIPO DOWNLIGHT SEM ABA DE REMATE, TROMMILUX, SÉRIE 9075, Ø114mm, 4000K	
	LUMINÁRIA DE ENCASTRAR NO TETO, DO TIPO DOWNLIGHT COM ABA DE REMATE, TROMMILUX SÉRIE 5511, Ø265mm, 4000K	
	LUMINÁRIA SUSPENSÃO DE TETO, DO TIPO TROMMILUX, SÉRIE 4556, DIMENSÃO 2880mm, 4000K	
	LUMINÁRIA DE PAREDE SALIENTE, DO TIPO APLIQUE, TROMMILUX SÉRIE 2076, LIZ ASCENDETTE E DESCENDENTE, IP54, 42W, 4000K	
	LINHA DE LUZ CONTÍNUA, TROMMILUX, SÉRIE 4010, APLICAÇÃO EM SANCA, 4000K	
	DETECTOR DE MOVIMENTO 360º DE ENCASTRAR, HAGER EE805A, OU EQUIVALENTE	
	BORNE DUPLO DE CARREGAMENTO VEÍCULOS ELÉTRICOS	
01	Modificações diversas	21.01.2026
00	Entrega do Projeto de Execução	19.12.2025
Revisão	Descrição	Data

TUU

Requerente
CÂMARA MUNICIPAL DE CANTANHEDE
Projeto
REQUALIFICAÇÃO E MODERNIZAÇÃO DA BIBLIOTECA MUNICIPAL DE CANTANHEDE
RUA EXEMPLO 11
0000-004 CANTANHEDE

Especialidade
PROJETO DA INSTALAÇÃO ELÉTRICA

Designação
PLANTA DE DISTRIBUIÇÃO DE ENERGIA - PISO 0
Zonas de Afetação dos Quadros
JANEIRO 2026
1:100

EL001

Observações
ESTE PROJETO DEVERÁ SER LIDO EM CONJUNTO COM AS PEÇAS ESCRITAS, ASSIM COMO, O PROJETO DE ARQUITETURA E AS RESTANTES ESPECIALIDADES. QUAISQUER DISCREPÂNCIAS DEVERÃO SER COMUNICADAS AO PROJETISTA. TODAS AS MEDIDAS DESTE DESENHO SÃO DE PROJETO E MERAMENTE INDICATIVAS, NECESSITAM SER RETIFICADAS EM OBRA.

Nome Ficheiro
BIBLICA_PE_ELE_PD_V0.DWG

Código
39962025

Equipa
ANA EXEMPLO | ENG ELETROTÉCNICO
LUIS BALSAS | ENG ELETROTÉCNICO

Reprodução proibida, Dec. Lei 45185 de 17 de Setembro e código do direito de autor e direitos conexos.

TUU.BUILDING DESIGN MANAGEMENT
arquitetura@tuu.pt www.tuu.pt

01	Modificações diversas	21.01.2026
00	Entrega do Projeto de Execução	19.12.2025
Revisão	Descrição	Data

TUU

Requerente
CÂMARA MUNICIPAL DE CANTANHEDE
Projeto
REQUALIFICAÇÃO E MODERNIZAÇÃO DA BIBLIOTECA MUNICIPAL DE CANTANHEDE
RUA EXEMPLO 11
0000-004 CANTANHEDE

Especialidade
PROJETO DA INSTALAÇÃO ELÉTRICA

Projeto de Execução
Designação
PLANTA DE DISTRIBUIÇÃO DE ENERGIA - PISO -1
Zonas de afetação dos quadros
JANEIRO 2026
1:100

EL002

Observações
ESTE PROJETO DEVERÁ SER LIDO EM CONJUNTO COM AS PEÇAS ESCRITAS. ASSIM COMO, O PROJETO DE ARQUITETURA E AS RESTANTES ESPECIALIDADES.
QUAISQUER DISCREPÂNCIAS DEVERÃO SER COMUNICADAS AO PROJETISTA. TODAS AS MEDIDAS DESTES DESENHOS SÃO DE PROJETO E MERAMENTE INDICATIVAS, NECESSITAM SER RETIFICADAS EM OBRA.


Nome Ficheiro
BIBLICA_PE_ELE_PD_V0.DWG

Código
39962025

Equipa
ANA EXEMPLO | ENG ELETROTÉCNICO
LUIS BALSAS | ENG ELETROTÉCNICO

Reprodução proibida, Dec. Lei 45/85 de 17 de Setembro e código do direito de autor e direitos conexos.

TUU.BUILDING DESIGN MANAGEMENT
arquitetura@tuu.pt www.tuu.pt

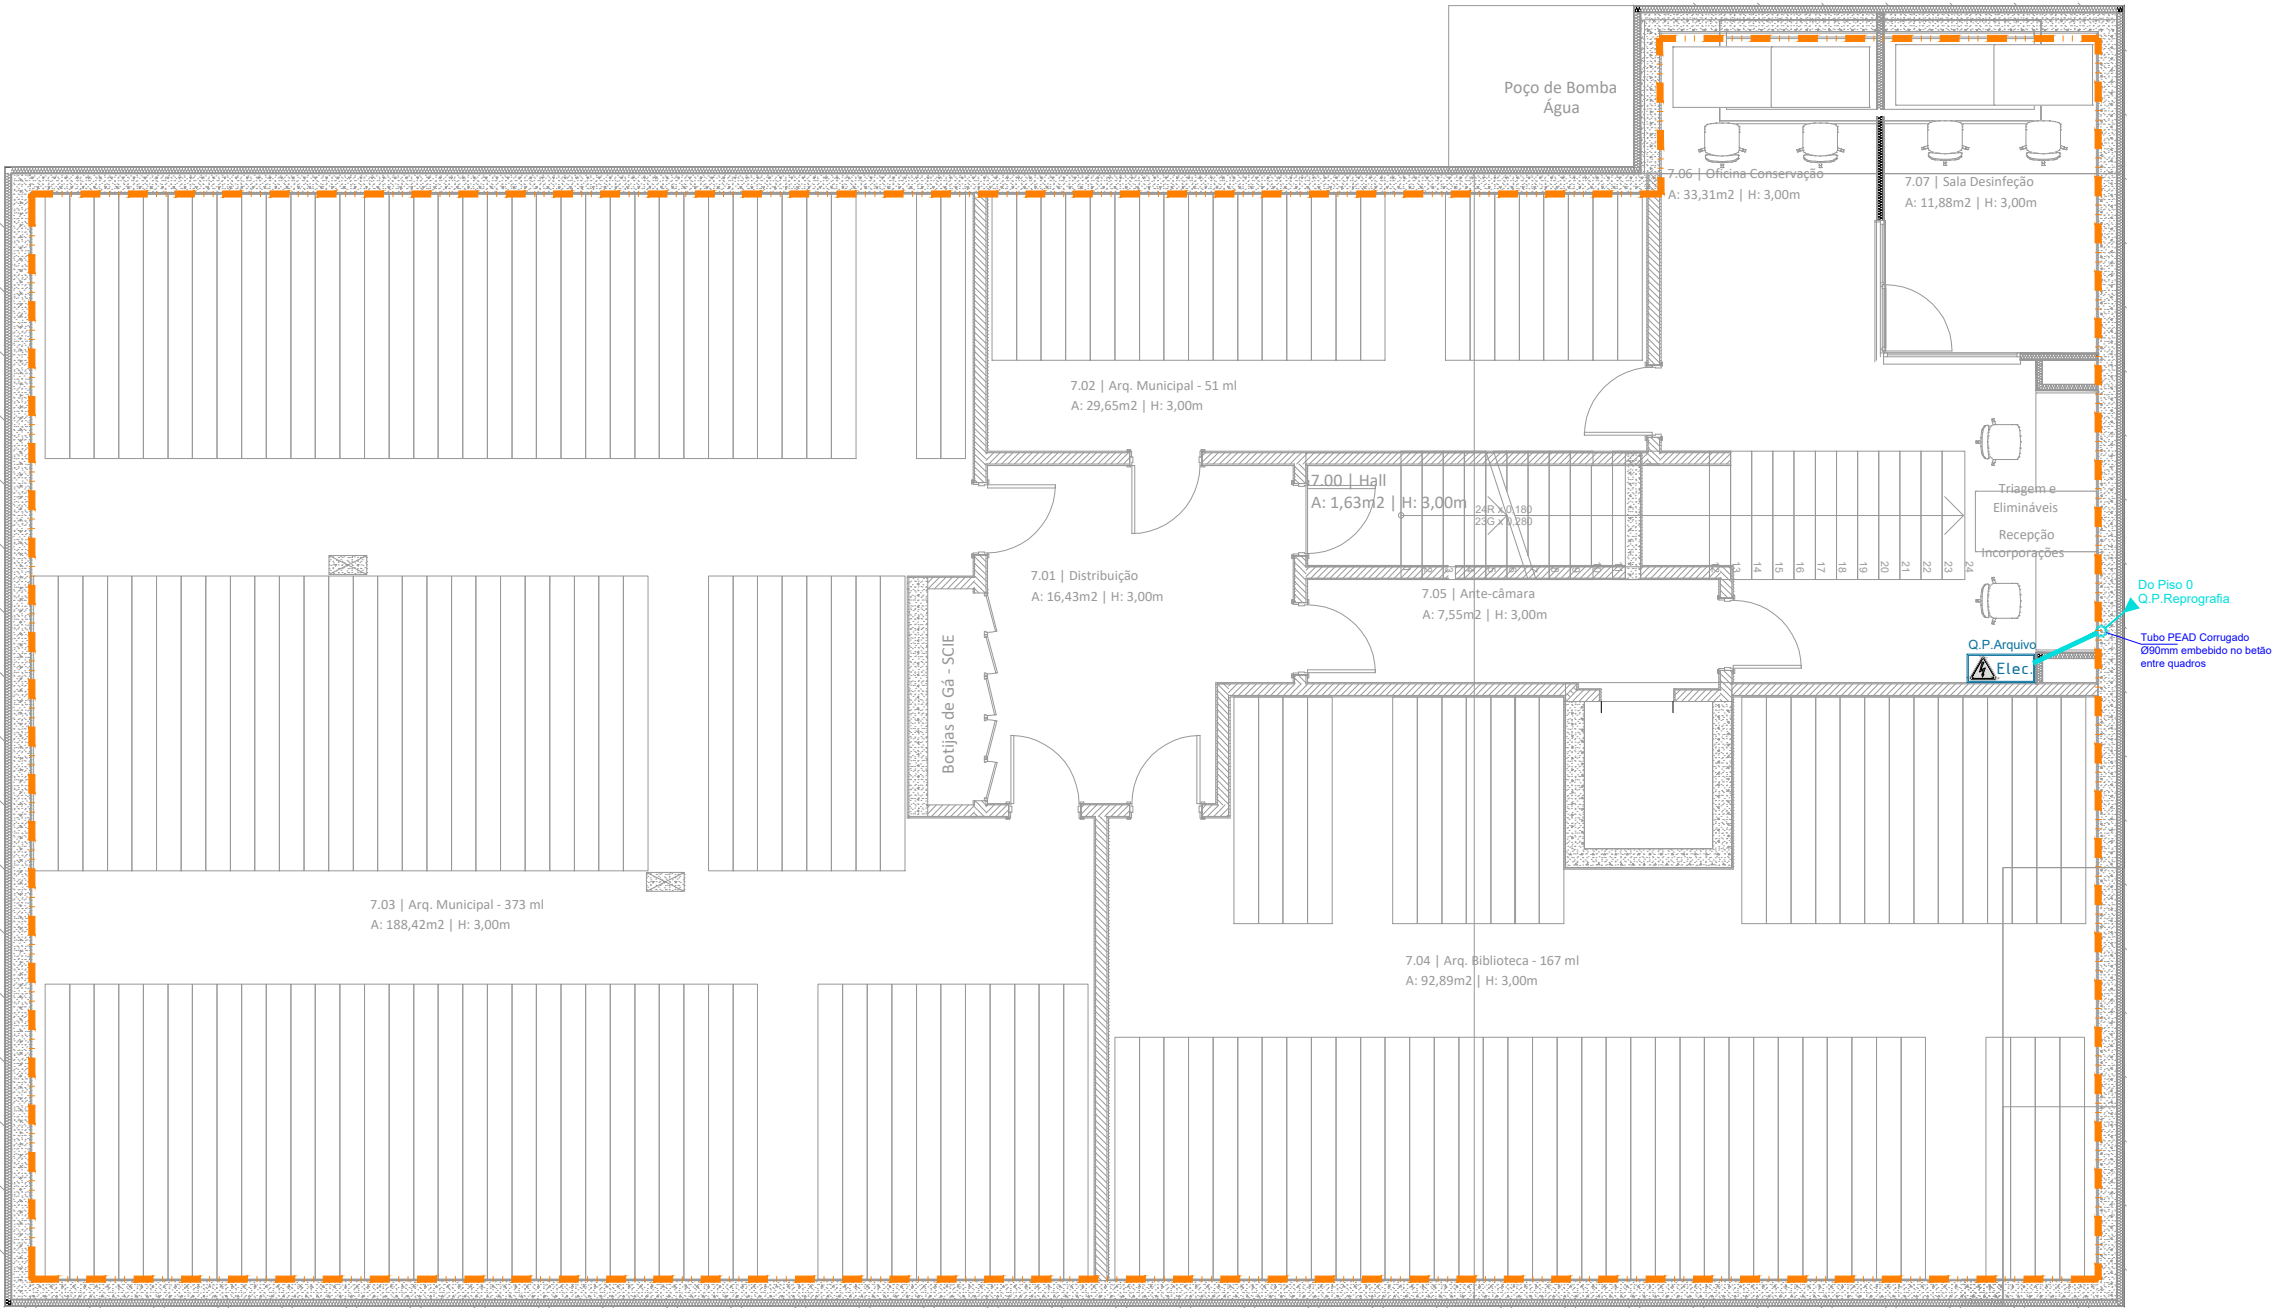

	QUADRO ELÉTRICO DO EDIFÍCIO	
	TOMADA ELÉTRICA 2P+1L, 16A, USOS GERAIS - ENCASTRAR	
	TOMADA ELÉTRICA 2P+1L, 16A, ESTANQUE IP55 - ENCASTRAR	
	TOMADA ELÉTRICA 2P+1L, 16A, ENCASTRAR, C/TAMPA IP44	
	TOMADA ELÉTRICA 2P+1L, 16A, ESTANQUE IP55 - SALENTE	
	CAIXA DE CHÃO 2 MÓDULOS (1xTOM 2P+1)	
	CAIXA DE CHÃO DE CHÃO 2 MÓDULOS (3xTOM 2P+1 + 2xTOM 2P+1 (UPS) + 2xRL45 CabE)	
	ALIMENTAÇÃO ELÉTRICA ESPECÍFICA DE EQUIPAMENTO	
	(Dimensões e altura, ver planta)	(Lx355mm)
	BLOCO AUTÔNOMO PERMANENTE	
	BLOCO AUTÔNOMO NÃO PERMANENTE	
	LUMINÁRIA DE ENCASTRAR NO TETO, DO TIPO TROMILUX, SÉRIE 405S DALI, DIMENSÃO L1=1975mm, L5, L1=1300 ou L5,2=1000mm, 4000K	
	LUMINÁRIA SUSPensa DE TETO, DO TIPO TROMILUX, SÉRIE 4556 DALI, DIMENSÃO 1975mm, 4000K	
	LUMINÁRIA SALENTE DE PAREDE, DO TIPO TROMILUX, SÉRIE 402S, DIMENSÃO 1220mm, 16 VERTICAL, 4000K	
	LUMINÁRIA DO TIPO PANEL LED, DE ENCASTRAR NO TETO, TROMILUX, SÉRIE 555S DALI, 95x95/95x90, 300 4000K IP30 IK02	
	LUMINÁRIA DE ENCASTRAR COM ABX DE REMATE, DO TIPO TROMILUX, SÉRIE 5511 DALI, DIMENSÃO 960mm, 4000K	
	LUMINÁRIA SUSPensa DE TETO LINEAR, TROMILUX, DA SÉRIE 4052, 4000K	
	LUMINÁRIA DE ENCASTRAR NO TETO, DO TIPO DOWNLIGHT SEM ABX DE REMATE, TROMILUX, SÉRIE 6075, 0114mm, 4000K	
	LUMINÁRIA DE ENCASTRAR NO TETO, DO TIPO DOWNLIGHT COM ABX DE REMATE, TROMILUX, SÉRIE 5511, 0265mm, 4000K	
	LUMINÁRIA SUSPensa DE TETO, DO TIPO TROMILUX, SÉRIE 4556, DIMENSÃO 386mm, 4000K	
	LUMINÁRIA DE PAREDE SALENTE, DO TIPO APLIQUE, TROMILUX SÉRIE 2076, LUZ ASCENDENTE E DESCENDENTE, IP04, 42W, 4000K	
	LINHA DE LUZ CONTÍNUA TROMILUX, SÉRIE 4195, APLICAÇÃO EM SANCA, 4000K	
	DETECTOR DE MOVIMENTO 360º DE ENCASTRAR, HAGER E60SA, OU EQUIVALENTE	
	BORNE DUPLO DE CARREGAMENTO VEÍCULOS ELÉCTRICOS	

01	Modificações diversas	21.01.20
00	Entrega do Projeto de Execução	19.12.20
Revisão	Descrição	Data

TUW

Especialidade
PROJETO DA INSTALAÇÃO ELÉTRICA

Designação
PLANTA DE CAMINHOS DE CABOS
CORRENTES FORTES (CFO)
PISO 0

JANEIRO 2026
1:100

EL003

ESTE PROJETO DEVERÁ SER LIDO EM CONJUNTO COM AS PEÇAS
ESCRITAS, ASSIM COMO, O PROJETO DE ARQUITETURA E AS
REMANESCENTES ESPECIALIDADES.
QUAISQUER DISCREPÂNCIAS DEVERÃO SER COMUNICADAS AO
PROJETISTA. TODAS AS MEDIDAS DESTES DESENHOS SÃO DE
REFERÊNCIA E MERAMENTE INDICATIVAS, NECESSITAM SER
RETIFICADAS EM OBRA.

Equipa
ANA EXEMPLO | ENG ELETROTÉCNICO
LUÍS BALSAS | ENG ELETROTÉCNICO

Reprodução proibida, Dec. Lei 45\85 de 17 de Setembro e código do direito de autor e direitos conexos.

TUU.BUILDING DESIGN MANAGEMENT

arquitetura@tuu.pt www.tuu.pt



01	Modificações diversas	21.01.2026
00	Entrega do Projeto de Execução	19.12.2025
Revisão	Descrição	Data

TUU

Requerente
CÂMARA MUNICIPAL DE CANTANHEDE
Projeto
REQUALIFICAÇÃO E MODERNIZAÇÃO DA BIBLIOTECA MUNICIPAL DE CANTANHEDE

RUA EXEMPLO 11
0000-004 **CANTANHEDE**

Especialidade
PROJETO DA INSTALAÇÃO ELÉTRICA

PROJETO DE EXECUÇÃO

Designação
PLANTA DE CAMINHOS DE CABOS CORRENTES FORTES (CFO) PISO -1

JANEIRO 2026
1:100

EL004

Observações
ESTE PROJETO DEVERÁ SER LIDO EM CONJUNTO COM AS PEÇAS ESCRITAS, ASSIM COMO, O PROJETO DE ARQUITETURA E AS RESTANTES ESPECIALIDADES.
QUAISQUER DISCREPÂNCIAS DEVERÃO SER COMUNICADAS AO PROJETISTA. TODAS AS MEDIDAS DESTES DESENHO SÃO DE PROJETO E MERAMENTE INDICATIVAS, NECESSITAM SER RETIFICADAS EM OBRA.


Nome Ficheiro
BIBLICA_PE_ELE_PD_V0.DWG

Código
39962025


Equipa
ANA EXEMPLO | **ENG ELETROTÉCNICO**
LUIS BALSAS | ENG ELETROTÉCNICO


Reprodução proibida, Dec. Lei 45/85 de 17 de Setembro e código do direito de autor e direitos conexos.

TUU.BUILDING DESIGN MANAGEMENT
arquitetura@tuu.pt www.tuu.pt

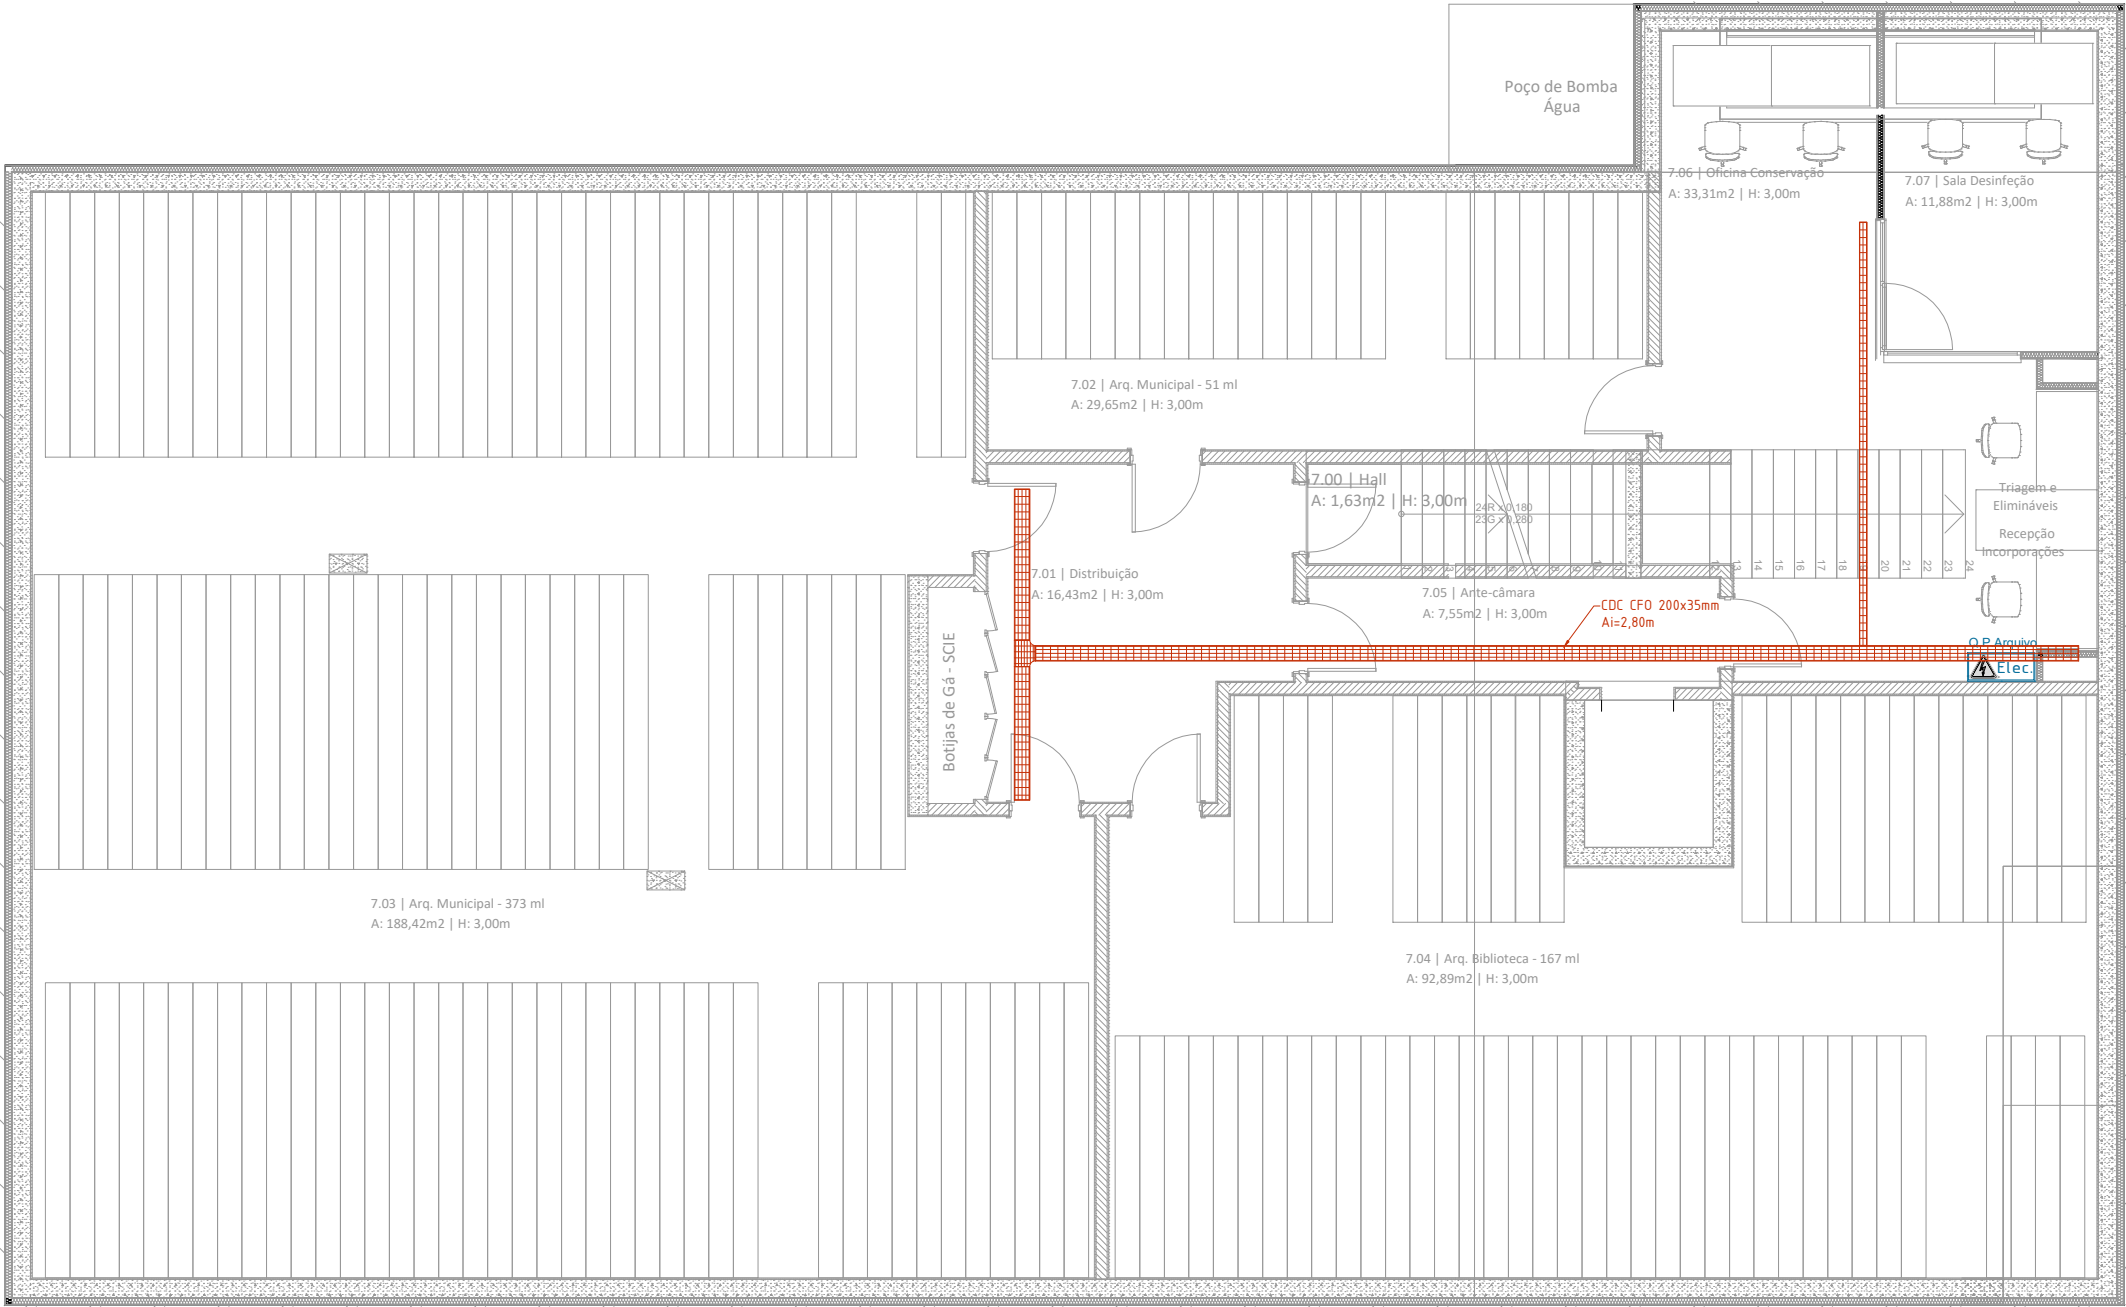

EXEMPLOS DE MODOS DE INSTALAÇÃO DE CAMINHOS DE CABOS

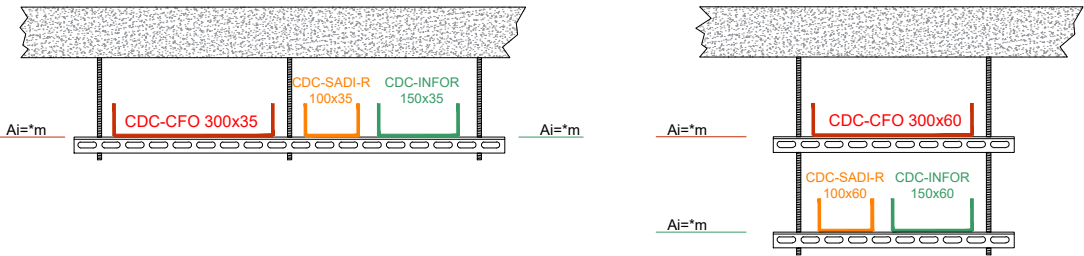

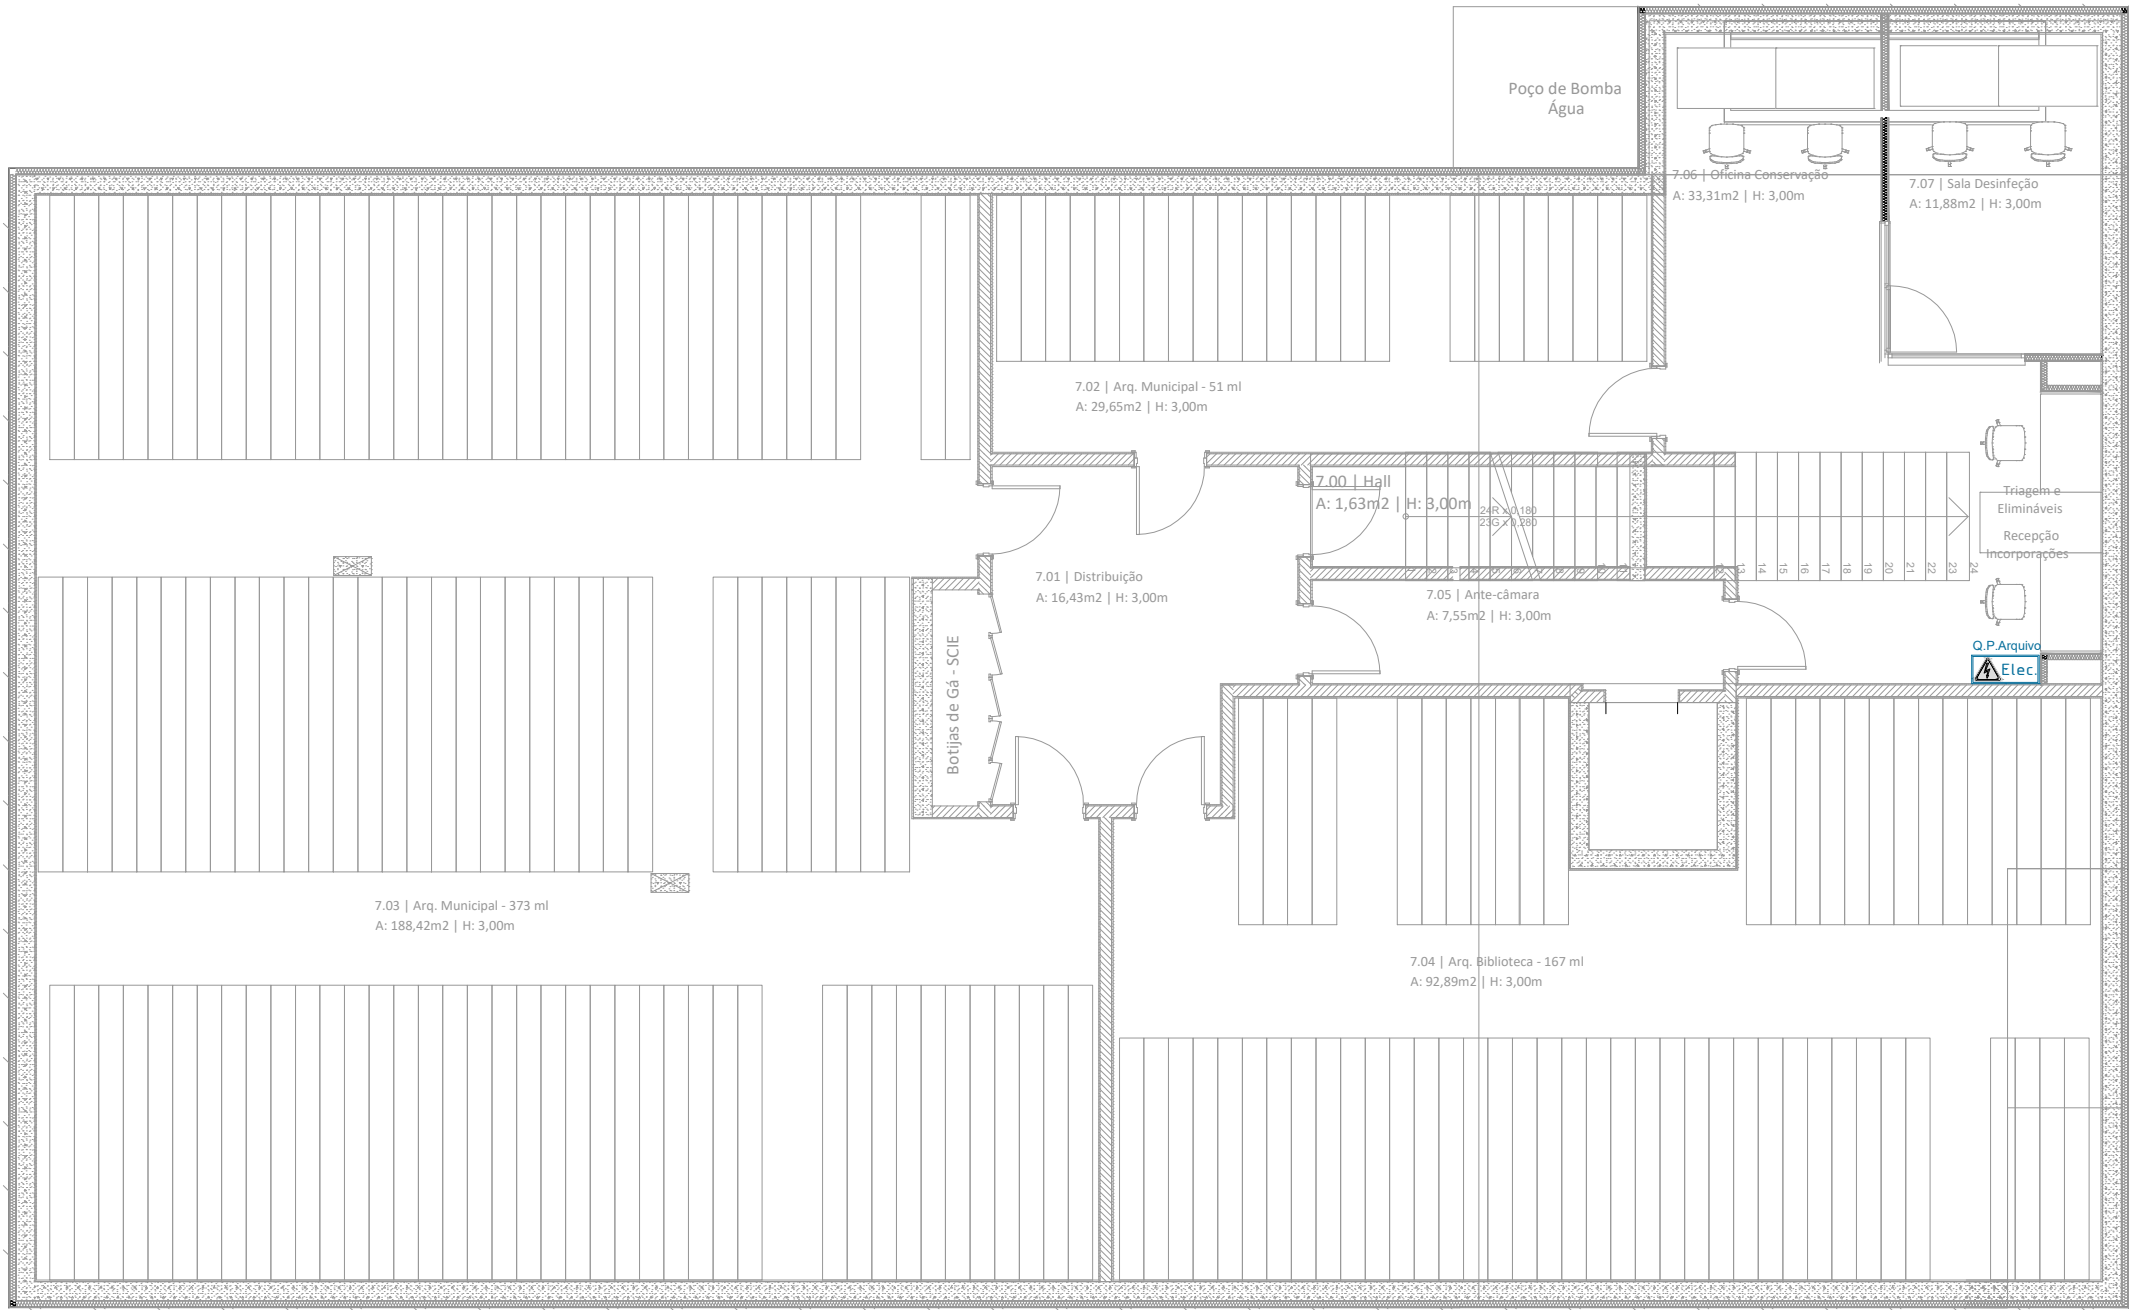

TUU

Requerente
CÂMARA MUNICIPAL DE CANTANHEDE
Projeto
REQUALIFICAÇÃO E MODERNIZAÇÃO DA BIBLIOTECA MUNICIPAL DE CANTANHEDE
RUA EXEMPLO 11
0000-004 CANTANHEDE

Especialidade
PROJETO DA INSTALAÇÃO ELÉTRICA

PROJETO DE EXECUÇÃO

Designação
PLANTA DE ALIMENTAÇÕES ESPECÍFICAS - PISO -1
-

JANEIRO 2026
1:100

EL006

Observações
ESTE PROJETO DEVERÁ SER LIDO EM CONJUNTO COM AS PEÇAS ESCRITAS, ASSIM COMO, O PROJETO DE ARQUITETURA E AS RESTANTES ESPECIALIDADES.
QUAISQUER DISCREPÂNCIAS DEVERÃO SER COMUNICADAS AO PROJETISTA. TODAS AS MEDIDAS DESTES DESENHOS SÃO DE PROJETO E MERAMENTE INDICATIVAS, NECESSITAM SER RETIFICADAS EM OBRA.

Nome Ficheiro
BIBLICA_PE_ELE_PD_V0.DWG

Código
39962025

Equipa
ANA EXEMPLO | ENG ELETROTÉCNICO
LUIS BALSAS | ENG ELETROTÉCNICO

Reprodução proibida, Dec. Lei 45/85 de 17 de Setembro e código do direito de autor e direitos conexos.

TUU.BUILDING DESIGN MANAGEMENT
arquitetura@tuu.pt www.tuu.pt

01	Modificações diversas	21.01.2026
00	Entrega do Projeto de Execução	19.12.2025
Revisão	Descrição	Data

TUU

Requerente
CÂMARA MUNICIPAL DE CANTANHEDE
Projeto
REQUALIFICAÇÃO E MODERNIZAÇÃO DA BIBLIOTECA MUNICIPAL DE CANTANHEDE

RUA EXEMPLO 11
0000-004 CANTANHEDE

Especialidade
PROJETO DA INSTALAÇÃO ELÉTRICA

PROJETO DE EXECUÇÃO

Designação
PLANTA DE TOMADAS DE ENERGIA - PISO -1
-

JANEIRO 2026
1:100

EL008

Observações
ESTE PROJETO DEVERÁ SER LIDO EM CONJUNTO COM AS PEÇAS ESCRITAS, ASSIM COMO, O PROJETO DE ARQUITETURA E AS RESTANTES ESPECIALIDADES.
QUAISQUER DISCREPÂNCIAS DEVERÃO SER COMUNICADAS AO PROJETISTA. TODAS AS MEDIDAS DESTES DESENHO SÃO DE PROJETO E MERAMENTE INDICATIVAS, NECESSITAM SER RETIFICADAS EM OBRA.


Nome Ficheiro
BIBLICA_PE_ELE_PD_V0.DWG

Código
39962025

Equipa
ANA EXEMPLO | ENG ELETROTÉCNICO
LUIS BALSAS | ENG ELETROTÉCNICO

Reprodução proibida, Dec. Lei 45/85 de 17 de Setembro e código do direito de autor e direitos conexos.

TUU.BUILDING DESIGN MANAGEMENT
arquitetura@tuu.pt www.tuu.pt

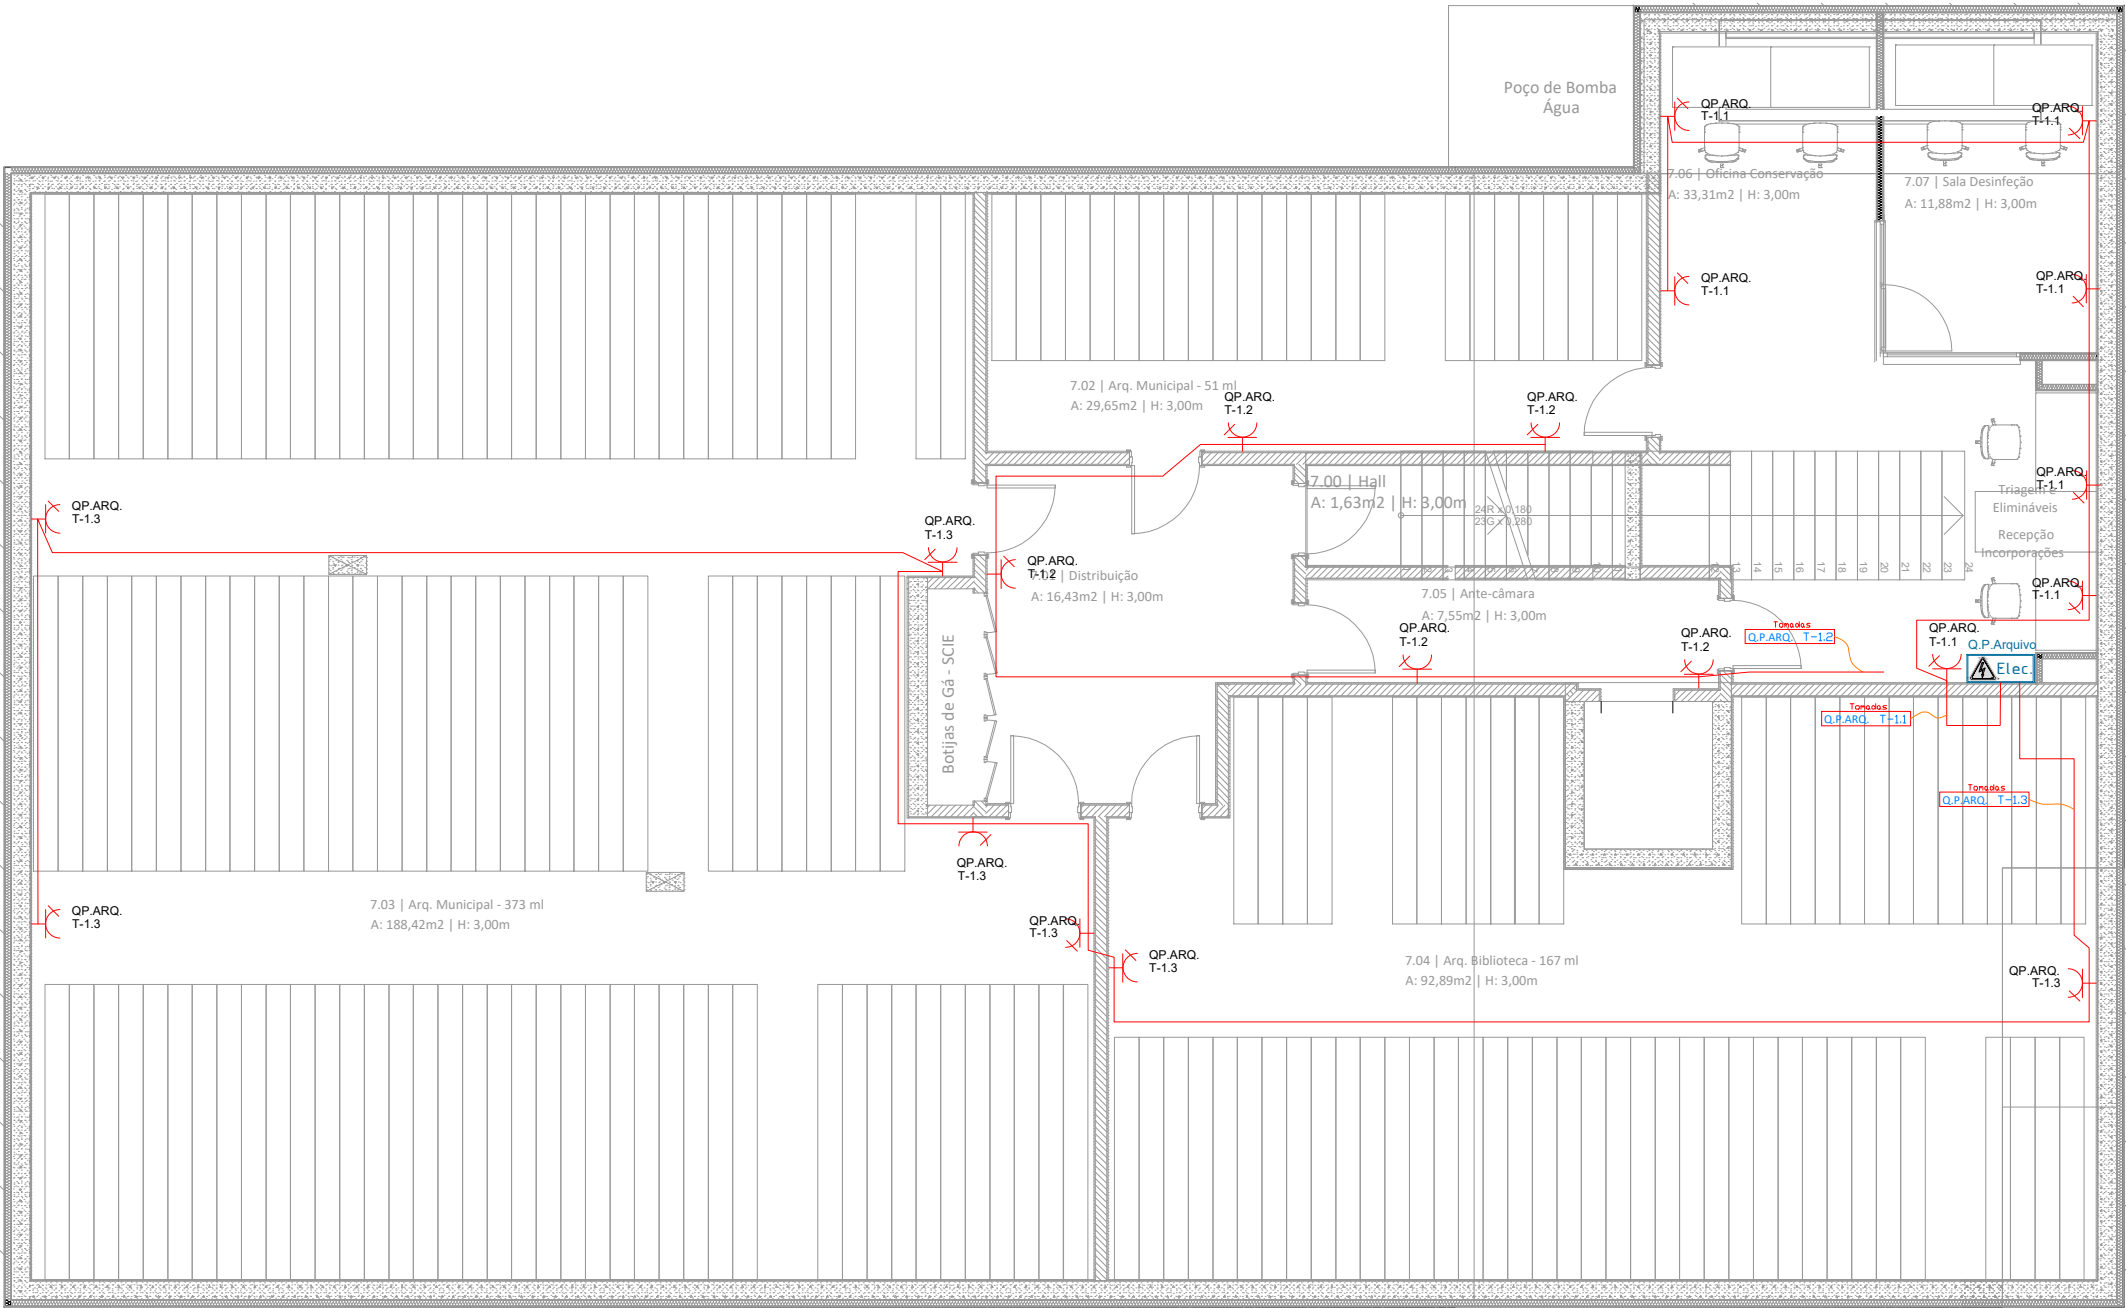

LEGENDA:

	QUADRO ELÉTRICO
	TOMADA ELÉTRICA 2P+T, 16A, USOS GERAIS - ENCASTRAR
	TOMADA ELÉTRICA TRIFÁSICA 3P+N+T, 16A, SALIENTE
	TOMADA ELÉTRICA 2P+T, 16A, ESTANQUE IP55 - ENCASTRAR
	TOMADA ELÉTRICA 2P+T, 16A, ENCASTRAR, C/TAMPA IP44
	TOMADA ELÉTRICA 2P+T, 16A, ESTANQUE IP55 - SALIENTE
	CAIXA DE CHÃO 2 MÓDULOS (1xTOM 2P+T)
	CAIXA DE CHÃO DE 12 MÓDULOS (3xTOM 2P+T + 2xTOM 2P+T (UPS) + 2xRJ45 Cat6)
	ALIMENTAÇÃO ELÉTRICA ESPECÍFICA DE EQUIPAMENTO
	TOMADA ELÉTRICA 2P+T, 16A, ESTABILIZADA UPS - ENCASTRAR

01	Modificações diversas	21.01.2026
00	Entrega do Projeto de Execução	19.12.2025
Revisão	Descrição	Data

TUU

Requerente
CÂMARA MUNICIPAL DE CANTANHEDE
Projeto
REQUALIFICAÇÃO E MODERNIZAÇÃO DA BIBLIOTECA MUNICIPAL DE CANTANHEDE

RUA EXEMPLO 11
0000-004 CANTANHEDE

Especialidade
PROJETO DA INSTALAÇÃO ELÉTRICA

PROJETO DE EXECUÇÃO

Designação
PLANTA DE TOMADAS ESTABILIZADAS (UPS) PISO -1

JANEIRO 2026
1:100

EL010

Observações
ESTE PROJETO DEVERÁ SER LIDO EM CONJUNTO COM AS PEÇAS ESCRITAS, ASSIM COMO, O PROJETO DE ARQUITETURA E AS RESTANTES ESPECIALIDADES.
QUAISQUER DISCREPÂNCIAS DEVERÃO SER COMUNICADAS AO PROJETISTA. TODAS AS MEDIDAS DESTES DESENHO SÃO DE PROJETO E MERAMENTE INDICATIVAS, NECESSITAM SER RETIFICADAS EM OBRA.


Nome Ficheiro
BIBLICA_PE_ELE_PD_V0.DWG

Código
39962025

Equipa
ANA EXEMPLO | ENG ELETROTÉCNICO
LUIS BALSAS | ENG ELETROTÉCNICO

Reprodução proibida, Dec. Lei 45/85 de 17 de Setembro e código do direito de autor e direitos conexos.

TUU.BUILDING DESIGN MANAGEMENT
arquitetura@tuu.pt www.tuu.pt

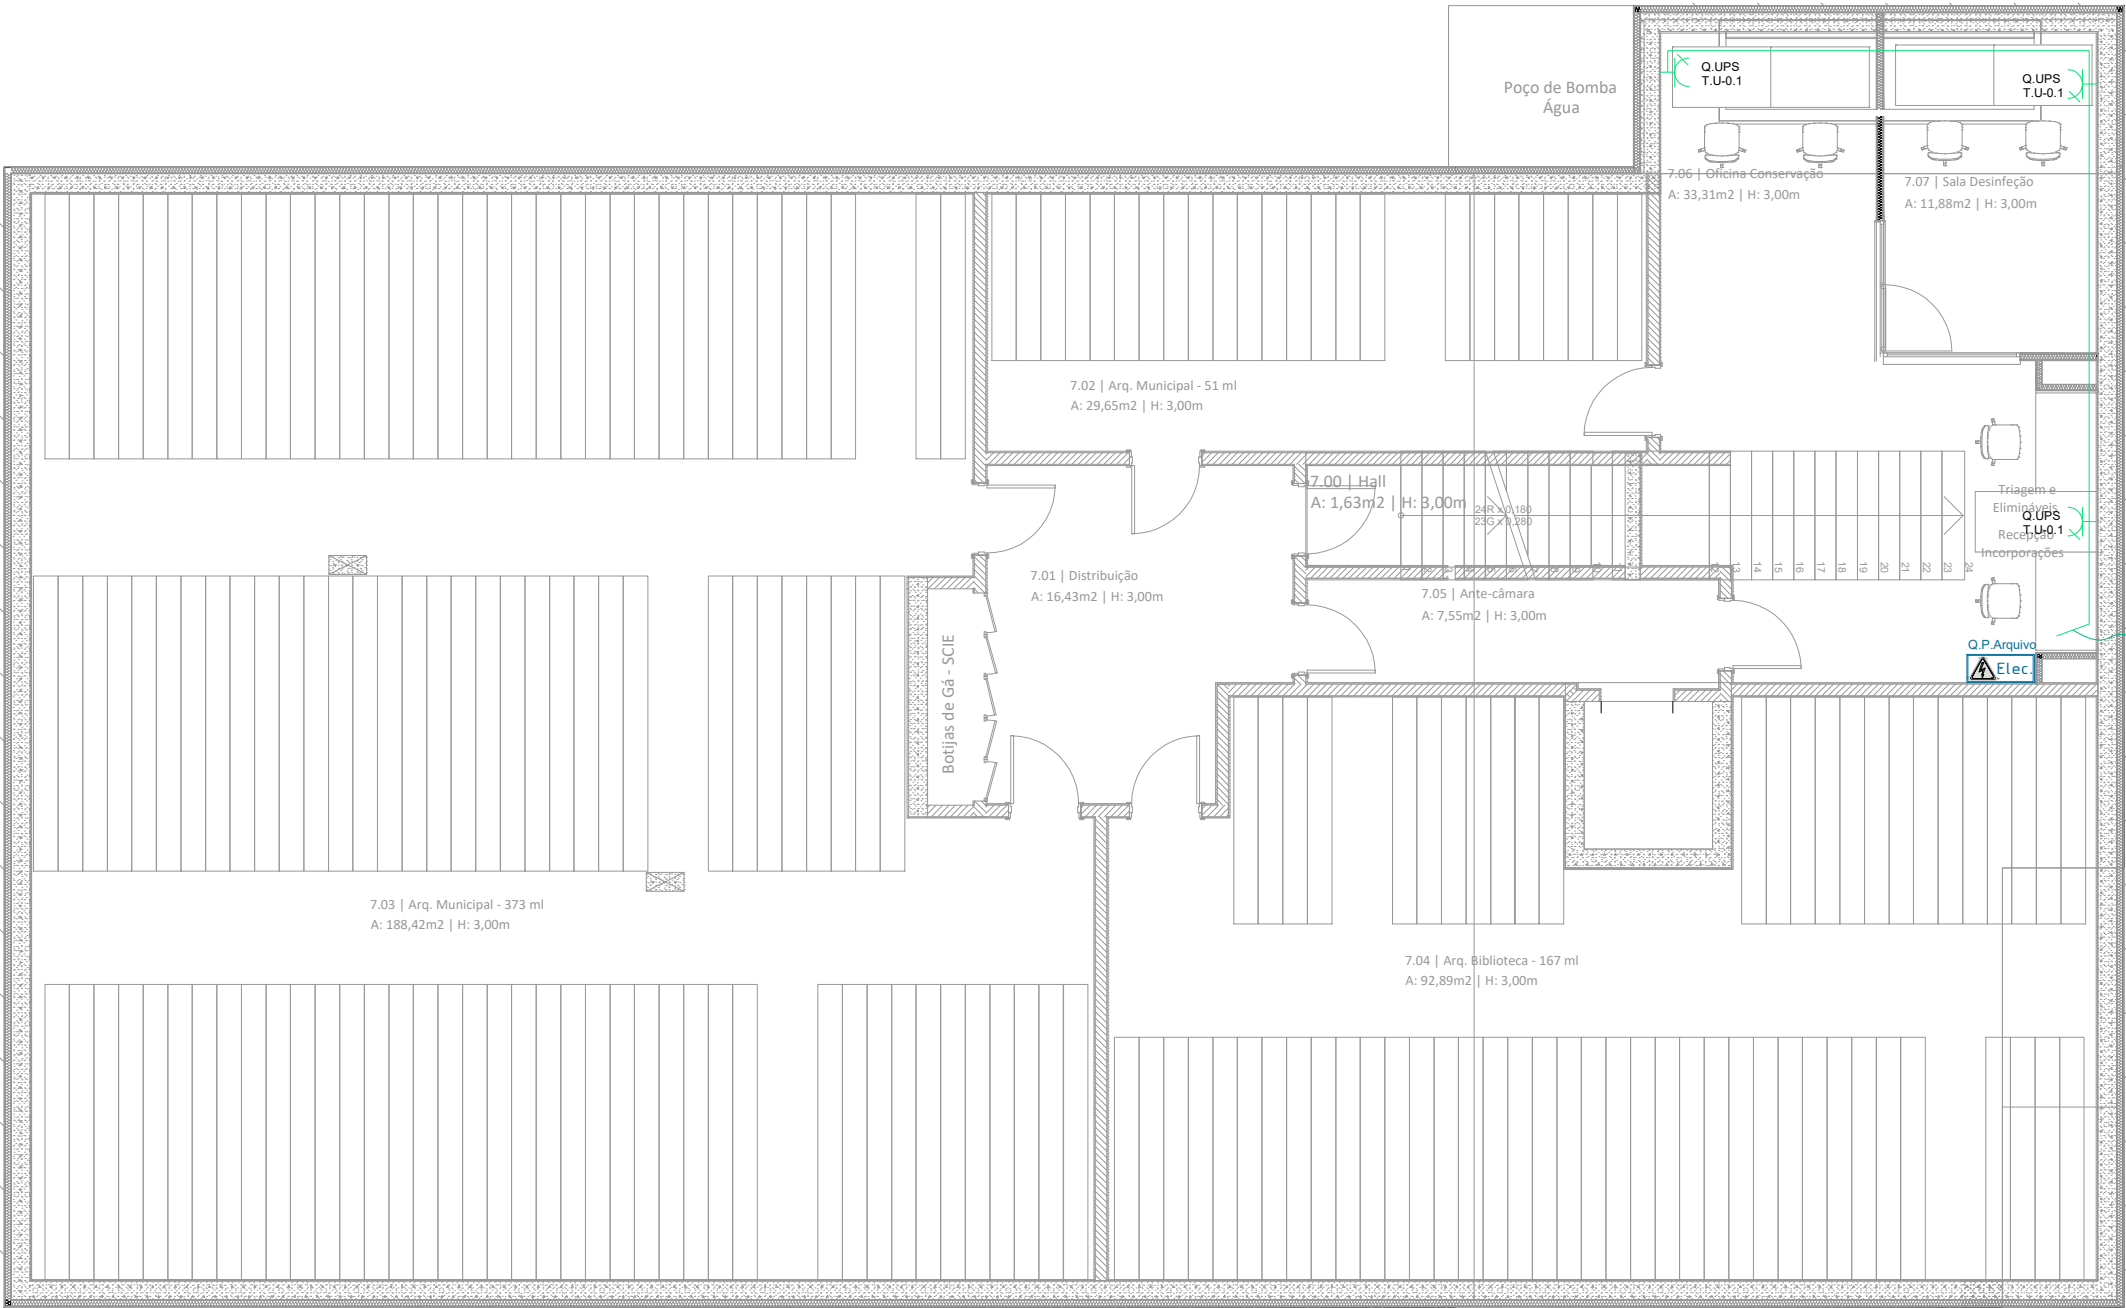

LEGENDA:

	QUADRO ELÉTRICO
	TOMADA ELÉTRICA 2P+T, 16A, USOS GERAIS - ENCASTRAR
	TOMADA ELÉTRICA TRIFÁSICA 3P+N+T, 16A, SALIENTE
	TOMADA ELÉTRICA 2P+T, 16A, ESTANQUE IP55 - ENCASTRAR
	TOMADA ELÉTRICA 2P+T, 16A, ENCASTRAR, C/TAMPA IP44
	TOMADA ELÉTRICA 2P+T, 16A, ESTANQUE IP55 - SALIENTE
	CAIXA DE CHÃO 2 MÓDULOS (1xTOM 2P+T)
	CAIXA DE CHÃO DE 12 MÓDULOS (3xTOM 2P+T + 2xTOM 2P+T (UPS) + 2xRJ45 Cat6)
	ALIMENTAÇÃO ELÉTRICA ESPECÍFICA DE EQUIPAMENTO
	TOMADA ELÉTRICA 2P+T, 16A, ESTABILIZADA UPS - ENCASTRAR



Os aparelhos de iluminação serão definidos pela arquitetura em conformidade com os mapas de iluminação apresentados, que devem ser verificados antes do início da empreitada.

Os aparelhos de iluminação serão comandados por sistema de domótica integrado (KNX/DALI) com os comandos de acordo com o indicado nas peças desenhadas.

Todos os traçados, alturas de montagem e localização de equipamentos, deverão ser confirmados sobre os desenhos do projeto de arquitetura ou nas reuniões de coordenação de obra com a presença do coordenador de todos os projetos.

Nos locais onde estejam indicadas esteiras de caminhos de cabos, as cablagens passarão no interior, transitando para tubo nos respetivos locais dos circuitos.

O índice de proteção de todos os materiais e equipamentos deverá ser adequado às condições locais de instalação, de acordo com a secção 512 das RTIEBT.

Todos os cabos serão colocados em tubagem do tipo ERM-F, ERPE ou VD.

Nas zonas de teto falso os cabos serão colocados em tubos em abraçadeiras ou em tubos apoiados e afixados nas esteiras de caminhos de cabos.

Cabo XZ1 (tr.zh) 3G1.5mm², alimentação elétrica das luminárias, enfado em tubo ou em caminhos de cabos.
Cabo de BUS DALI 2x1.5mm², enfado em tubo ou em caminhos de cabos.

LEGENDA:

	QUADRO ELÉTRICO DO EDIFÍCIO
	TOMADA ELÉTRICA 2P+T, 16A, USOS GERAIS - ENCASTRAR
	TOMADA ELÉTRICA 2P+T, 16A, ESTANQUE IP55 - ENCASTRAR
	TOMADA ELÉTRICA 2P+T, 16A, ENCASTRAR, C/TAMPA IP44
	TOMADA ELÉTRICA 2P+T, 16A, ESTANQUE IP55 - SALIENTE
	CAIXA DE CHÃO 2 MÓDULOS (1xTOM 2P+T)
	CAIXA DE CHÃO DE 12 MÓDULOS (3xTOM 2P+T + 2xTOM 2P+T (UPS) + 2xPLAS GAB)
	ALIMENTAÇÃO ELÉTRICA ESPECÍFICA DE EQUIPAMENTO
	BLOCO AUTÓNOMO PERMANENTE
	BLOCO AUTÓNOMO NÃO PERMANENTE
	LUMINÁRIA DE ENCASTRAR NO TETO, DO TIPO TROMILUX, SÉRIE 4526 DALI, DIMENSÃO L1=1975mm, L5.1=1300 ou L5.2=1000mm, 4000K
	LUMINÁRIA SUSPensa DE TETO, DO TIPO TROMILUX, SÉRIE 4556 DALI, DIMENSÃO 1975mm, 4000K
	LUMINÁRIA SALIENTE DE PAREDE, DO TIPO TROMILUX, SÉRIE 4028, DIMENSÃO 1200mm, NA VERTICAL, 4000K
	LUMINÁRIA DO TIPO PAINEL LED, DE ENCASTRAR NO TETO, TROMILUX, SÉRIE 5550 DALI, 595x595mm, 30W 4000K IP30 IK02
	LUMINÁRIA DE ENCASTRAR COM ABA DE REMATE, DO TIPO TROMILUX, SÉRIE 5511 DALI, DIMENSÃO 965mm, 4000K
	LUMINÁRIA SUSPensa DE TETO LINEAR, TROMILUX, DA SÉRIE 4052, 4000K
	LUMINÁRIA DE ENCASTRAR NO TETO, DO TIPO DOWNLIGHT SEM ABA DE REMATE, TROMILUX, SÉRIE 6075, Ø114mm, 4000K
	LUMINÁRIA DE ENCASTRAR NO TETO, DO TIPO DOWNLIGHT COM ABA DE REMATE, TROMILUX SÉRIE 5511, Ø265mm, 4000K
	LUMINÁRIA SUSPensa DE TETO, DO TIPO TROMILUX, SÉRIE 4556, DIMENSÃO 2880mm, 4000K
	LUMINÁRIA DE PAREDE SALIENTE, DO TIPO APLIQUE, TROMILUX SÉRIE 2076, LUZ ASCENDENTE E DESCENDENTE, IP54, 42W, 4000K
	LINHA DE LUZ CONTÍNUA, TROMILUX, SÉRIE 4010, APLICAÇÃO EM SANCA, 4000K
	DETECTOR DE MOVIMENTO 360° DE ENCASTRAR, HAGER EE805A, OU EQUIVALENTE
	BORNE DUPLO DE CARREGAMENTO VEÍCULOS ELÉTRICOS

01	Modificações diversas	21.01.2025
02	Edição do Projeto de Execução	19.12.2025
Revisão	Descrição	Data

TUU

Requerente
CÂMARA MUNICIPAL DE CANTANHEDE
Projeto
REQUALIFICAÇÃO E MODERNIZAÇÃO DA BIBLIOTECA MUNICIPAL DE CANTANHEDE
RUA EXEMPLO 11
0000-004 CANTANHEDE

Especialidade
PROJETO DA INSTALAÇÃO ELÉTRICA

PROJETO DE EXECUÇÃO

Designação
PLANTA DE ILUMINAÇÃO NORMAL PISO 0
BUS DALI
JANEIRO 2026
1:100

EL011

Observações
ESTE PROJETO DEVERÁ SER LIDO EM CONJUNTO COM AS PEÇAS ESCRITAS, ASSIM COMO, O PROJETO DE ARQUITETURA E AS RESTANTES ESPECIALIDADES.
QUAISQUER DISCREPÂNCIAS DEVERÃO SER COMUNICADAS AO PROJETISTA. TODAS AS MEDIDAS DESTE DESENHO SÃO DE PROJETO E MERAMENTE INDICATIVAS, NECESSITAM SER RETIFICADAS EM OBRA.

Nome Ficheiro
BIBLICA_PE_ELE_PD_V0.DWG

Código
39962025

Equipa
ANA EXEMPLO | ENG ELETROTÉCNICO
LUIS BALSAS | ENG ELETROTÉCNICO

Reprodução proibida, Dec. Lei 45185 de 17 de Setembro e código do direito de autor e direitos conexos.

TUU.BUILDING DESIGN MANAGEMENT
arquitetura@tuu.pt www.tuu.pt

01	Modificações diversas	21.01.2026
00	Entrega do Projeto de Execução	19.12.2025
Revisão	Descrição	Data

TUU

Requerente
CÂMARA MUNICIPAL DE CANTANHEDE
Projeto
REQUALIFICAÇÃO E MODERNIZAÇÃO DA BIBLIOTECA MUNICIPAL DE CANTANHEDE

RUA EXEMPLO 11
0000-004 CANTANHEDE

Especialidade
PROJETO DA INSTALAÇÃO ELÉTRICA

PROJETO DE EXECUÇÃO

Designação
PLANTA DE ILUMINAÇÃO NORMAL PISO -1

JANEIRO 2026
1:100

EL012

Observações
ESTE PROJETO DEVERÁ SER LIDO EM CONJUNTO COM AS PEÇAS ESCRITAS, ASSIM COMO, O PROJETO DE ARQUITETURA E AS RESTANTES ESPECIALIDADES.
QUAISQUER DISCREPÂNCIAS DEVERÃO SER COMUNICADAS AO PROJETISTA. TODAS AS MEDIDAS DESTES DESENHO SÃO DE PROJETO E MERAMENTE INDICATIVAS, NECESSITAM SER RETIFICADAS EM OBRA.

Nome Ficheiro
BIBLICA_PE_ELE_PD_V0.DWG


Código
39962025

Equipa
ANA EXEMPLO | ENG ELETROTÉCNICO
LUIS BALSAS | ENG ELETROTÉCNICO

Reprodução proibida, Dec. Lei 45/85 de 17 de Setembro e código do direito de autor e direitos conexos.

TUU.BUILDING DESIGN MANAGEMENT

arquitetura@tuu.pt www.tuu.pt

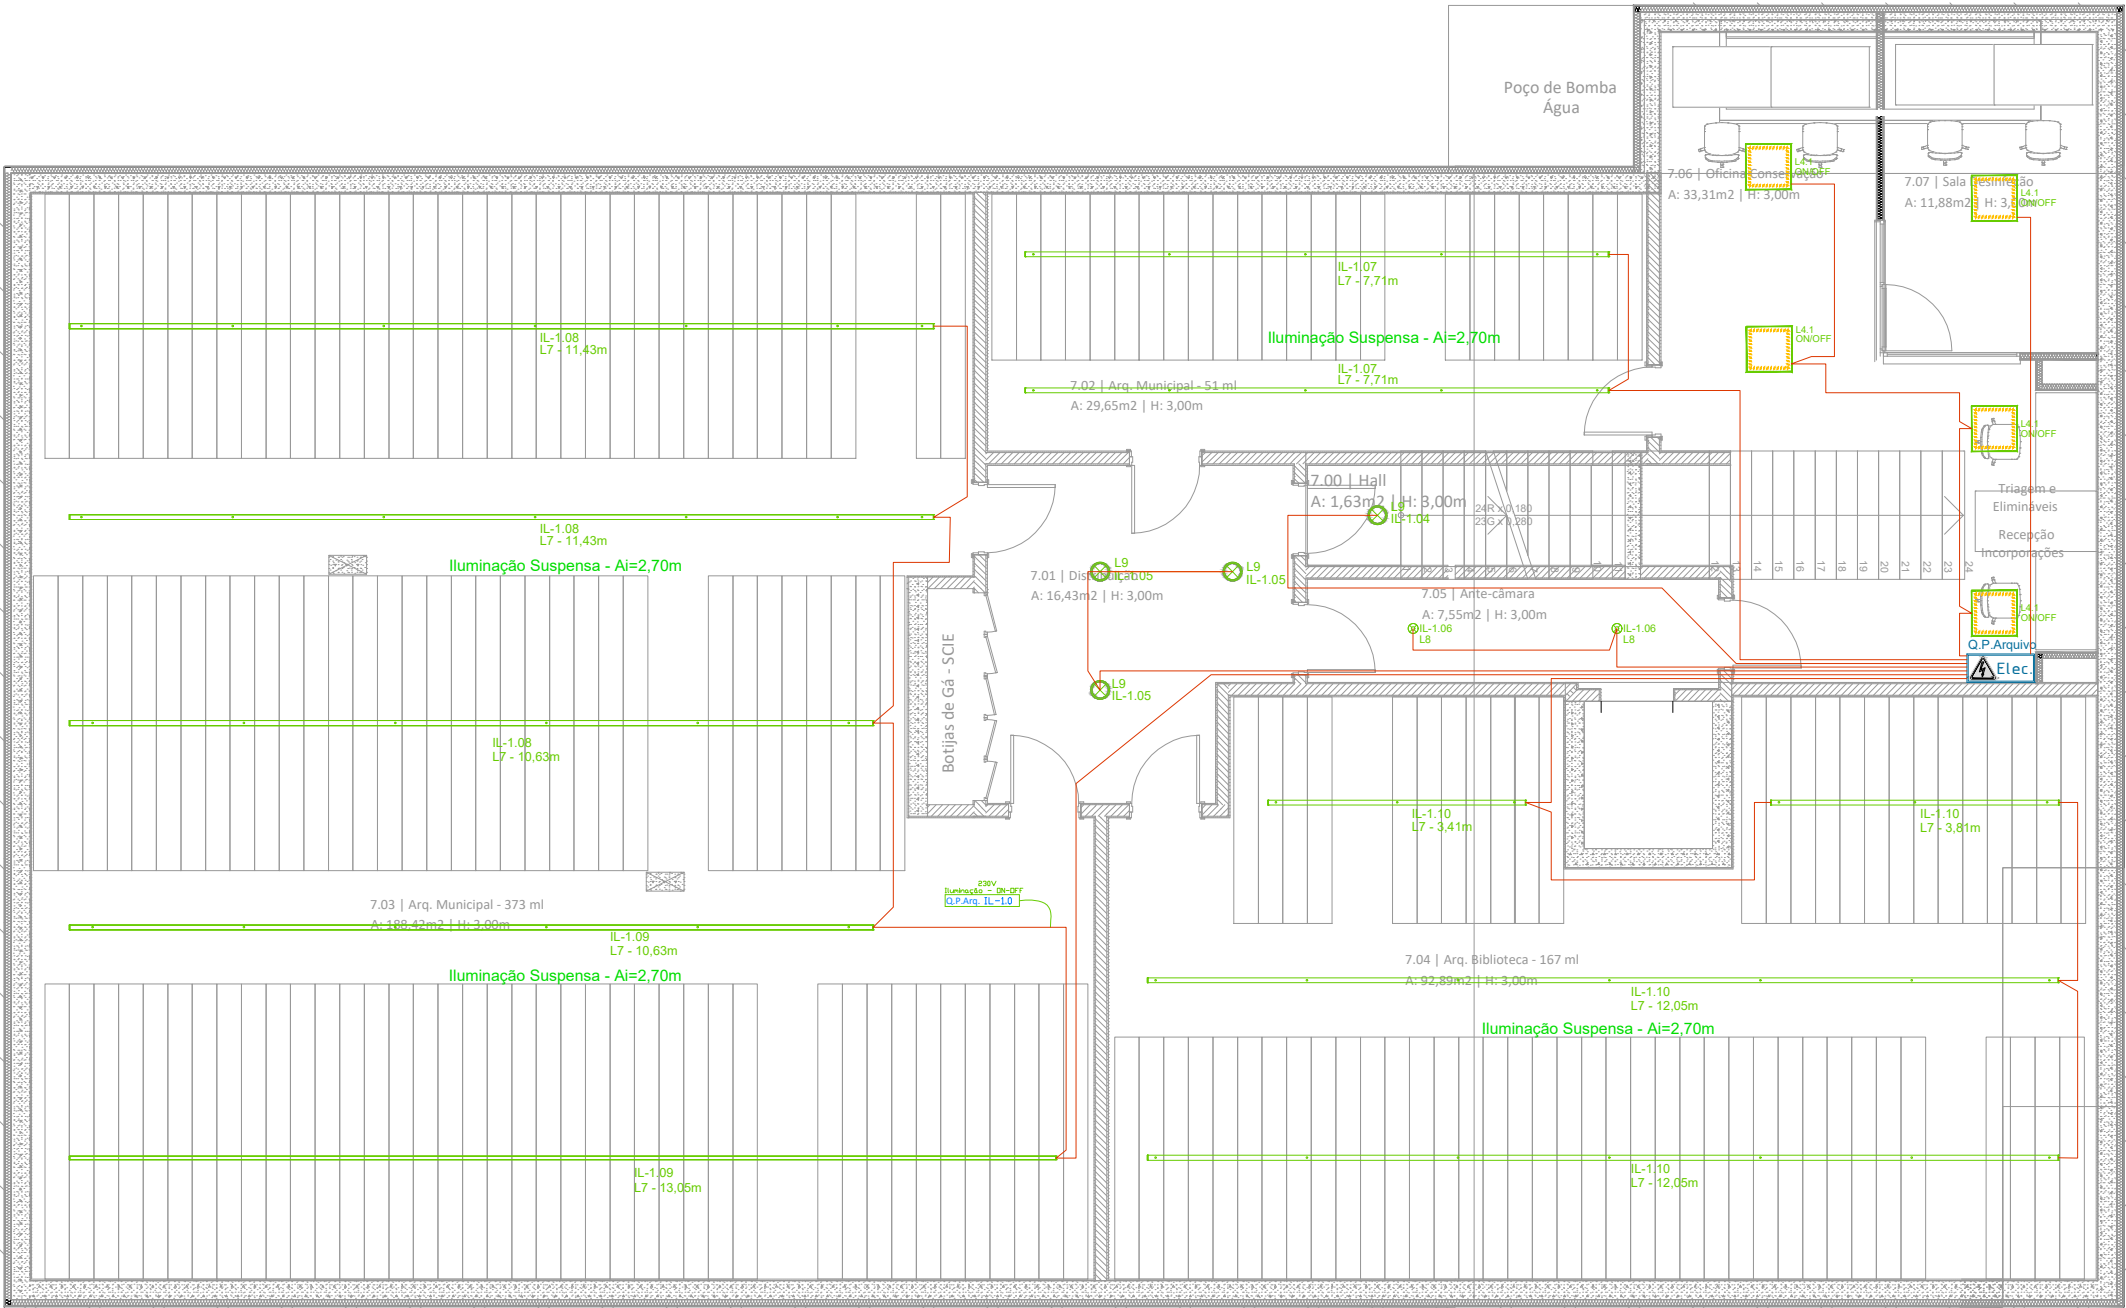

LEGENDA:

	QUADRO ELÉTRICO DO EDIFÍCIO
	TOMADA ELÉTRICA 2P+T, 16A, USOS GERAIS - ENCASTRAR
	TOMADA ELÉTRICA 2P+T, 16A, ESTANQUE IP55 - ENCASTRAR
	TOMADA ELÉTRICA 2P+T, 16A, ENCASTRAR, C/TAMPA IP44
	TOMADA ELÉTRICA 2P+T, 16A, ESTANQUE IP55 - SALIENTE
	CAIXA DE CHÃO 2 MÓDULOS (1xTOM 2P+T)
	CAIXA DE CHÃO DE 12 MÓDULOS (3xTOM 2P+T + 2xTOM 2P+T (UPS) + 2xRJ45 Cat6)
	ALIMENTAÇÃO ELÉTRICA ESPECÍFICA DE EQUIPAMENTO
	(Lx35mm)

	Cabo XZ1 (frt.zh) 3G1,5mm², alimentação elétrica das luminárias, enfiado em tubo ou em caminhos de cabos.
	Cabo de BUS DALI 2x1,5mm², enfiado em tubo ou em caminhos de cabos.

	BLOCO AUTÓNOMO PERMANENTE
	BLOCO AUTÓNOMO NÃO PERMANENTE
	LUMINÁRIA DE ENCASTRAR NO TETO, DO TIPO TROMILUX, SÉRIE 4526 DALI, DIMENSÃO L1=1975mm, L5.1=1300 ou L5.2=1000mm, 4000K
	LUMINÁRIA SUSPENSE DE TETO, DO TIPO TROMILUX, SÉRIE 4556 DALI, DIMENSÃO 1975mm, 4000K
	LUMINÁRIA SALIENTE DE PAREDE, DO TIPO TROMILUX, SÉRIE 4028, DIMENSÃO 1220mm, NA VERTICAL, 4000K
	LUMINÁRIA DO TIPO PAINEL LED, DE ENCASTRAR NO TETO, TROMILUX, SÉRIE 5550 DALI, 595x5950mm, 30W 4000K IP30 IK02
	LUMINÁRIA DE ENCASTRAR COM ABA DE REMATE, DO TIPO TROMILUX, SÉRIE 5511 DALI, DIMENSÃO 965mm, 4000K
	LUMINÁRIA SUSPENSE DE TETO LINEAR, TROMILUX, DA SÉRIE 4052, 4000K
	LUMINÁRIA DE ENCASTRAR NO TETO, DO TIPO DOWNLIGHT SEM ABA DE REMATE, TROMILUX, SÉRIE 6075, Ø114mm, 4000K
	LUMINÁRIA DE ENCASTRAR NO TETO, DO TIPO DOWNLIGHT COM ABA DE REMATE, TROMILUX SÉRIE 5511, Ø265mm, 4000K
	LUMINÁRIA SUSPENSE DE TETO, DO TIPO TROMILUX, SÉRIE 4556, DIMENSÃO 2880mm, 4000K
	LUMINÁRIA DE PAREDE SALIENTE, DO TIPO APLIQUE, TROMILUX SÉRIE 2076, LUZ ASCENDENTE E DESCENDENTE, IP54, 42W, 4000K
	LINHA DE LUZ CONTÍNUA, TROMILUX, SÉRIE 4010, APLICAÇÃO EM SANCA, 4000K
	DETECTOR DE MOVIMENTO 360° DE ENCASTRAR, HAGER EE805A, OU EQUIVALENTE
	BORNE DUPLO DE CARREGAMENTO VEÍCULOS ELÉTRICOS

Os aparelhos de iluminação serão definidos pela arquitetura em conformidade com os mapas de iluminação apresentados, que devem ser verificados antes do início da empreitada.

Os aparelhos de iluminação serão comandados por sistema de domótica integrado (KNX/DALI) com os comandos de acordo com o indicado nas peças desenhadas.

Todos os traçados, alturas de montagem e localização de equipamentos, deverão ser confirmados sobre os desenhos do projeto de arquitetura ou nas reuniões de coordenação de obra com a presença do coordenador de todos os projetos.

Nos locais onde estejam indicadas esteiras de caminhos de cabos, as cablagens passarão no interior, transitando para tubo nos respetivos locais dos circuitos.

O índice de proteção de todos os materiais e equipamentos deverá ser adequado às condições locais de instalação, de acordo com a secção 512 das RTIEBT.

Todos os cabos serão colocados em tubagem do tipo ERM-F, ERFE ou VD.

Nas zonas de teto falso os cabos serão colocados em tubos em abraçadeiras ou em tubos apoiados e afilçados nas esteiras de caminhos de cabos.



LEGENDA:		
	QUADRO ELÉTRICO DO EDIFÍCIO	
	TOMADA ELÉTRICA 2P+T, 16A, USOS GERAIS - ENCASTRAR	
	TOMADA ELÉTRICA 2P+T, 16A, ESTANQUE IP55 - ENCASTRAR	
	TOMADA ELÉTRICA 2P+T, 16A, ENCASTRAR, CTAMPA IP44	
	TOMADA ELÉTRICA 2P+T, 16A, ESTANQUE IP55 - SALIENTE	
	CAIXA DE CHÃO 2 MÓDULOS (1xTOM 2P+T)	
	CAIXA DE CHÃO DE 12 MÓDULOS (3xTOM 2P+T + 2xTOM 2P+T (UPS) + 2xRJ45 Cat6)	
	ALIMENTAÇÃO ELÉTRICA ESPECÍFICA DE EQUIPAMENTO	
	(Dimensões e altura, ver planta)	
	BLOCO AUTÔNOMO PERMANENTE	
	BLOCO AUTÔNOMO NÃO PERMANENTE	
	LUMINÁRIA DE ENCASTRAR NO TETO, DO TIPO TROMILUX, SÉRIE 4526 DALI, DIMENSÃO L=1975mm, L5=11300 ou L5=21000mm, 4000K	
	LUMINÁRIA SUSPENSÃO DE TETO, DO TIPO TROMILUX, SÉRIE 4556 DALI, DIMENSÃO 1975mm, 4000K	
	LUMINÁRIA SALIENTE DE PAREDE, DO TIPO TROMILUX, SÉRIE 4028, DIMENSÃO 1220mm, NA VERTICAL, 4000K	
	LUMINÁRIA DO TIPO PANEL LED, DE ENCASTRAR NO TETO, DO TIPO DOWNLIGHT SEM ABA DE REMATE, TROMILUX, SÉRIE 5550 DALI, 595x595mm, 30W 4000K (P30 R02)	
	LUMINÁRIA DE ENCASTRAR COM ABA DE REMATE, DO TIPO TROMILUX, SÉRIE 5511 DALI, DIMENSÃO 965mm, 4000K	
	LUMINÁRIA SUSPENSÃO DE TETO LINEAR, TROMILUX, DA, SÉRIE 4052, 4000K	
	LUMINÁRIA DE ENCASTRAR NO TETO, DO TIPO DOWNLIGHT SEM ABA DE REMATE, TROMILUX, SÉRIE 9075, Ø114mm, 4000K	
	LUMINÁRIA DE ENCASTRAR NO TETO, DO TIPO DOWNLIGHT COM ABA DE REMATE, TROMILUX, SÉRIE 5511, Ø265mm, 4000K	
	LUMINÁRIA SUSPENSÃO DE TETO, DO TIPO TROMILUX, SÉRIE 4556, DIMENSÃO 2800mm, 4000K	
	LUMINÁRIA DE PAREDE SALIENTE, DO TIPO APLIQUE, TROMILUX, SÉRIE 2076, LUZ ASCENDENTE E DESCENDENTE, IP54, 42W, 4000K	
	LINHA DE LUZ CONTÍNUA TROMILUX, SÉRIE 4010, APLICAÇÃO EM SANCA, 4000K	
	DETECTOR DE MOVIMENTO 360º DE ENCASTRAR, HAGER EE805A, OU EQUIVALENTE	
	BORNE DUPLO DE CARREGAMENTO VEÍCULOS ELÉTRICOS	
01	Modificações diversas	21.01.2026
00	Entrega do Projeto de Execução	19.12.2025
Revisão	Descrição	Data

TUU

Requerente
CÂMARA MUNICIPAL DE CANTANHEDE
Projeto
REQUALIFICAÇÃO E MODERNIZAÇÃO DA BIBLIOTECA MUNICIPAL DE CANTANHEDE
RUA EXEMPLO 11
0000-004 CANTANHEDE

Especialidade
PROJETO DA INSTALAÇÃO ELÉTRICA

Projeto de Execução
Designação
PLANTA DE EQUIPAMENTOS E BUS KNX - PISO 0

JANEIRO 2026
1:100

EL013

Observações
ESTE PROJETO DEVERÁ SER LIDO EM CONJUNTO COM AS PEÇAS ESCRITAS, ASSIM COMO, O PROJETO DE ARQUITETURA E AS RESTANTES ESPECIALIDADES. QUAISQUER DISCREPÂNCIAS DEVERÃO SER COMUNICADAS AO PROJETISTA. TODAS AS MEDIDAS DESTES DESENHOS SÃO DE PROJETO E MERAMENTE INDICATIVAS, NECESSITAM SER RETIFICADAS EM OBRA.

Nome Ficheiro
BIBLICA_PE_ELE_PD_V0.DWG


Código
39962025

Equipa
ANA EXEMPLO | ENG ELETROTÉCNICO
LUIS BALSAS | ENG ELETROTÉCNICO

Reprodução proibida, Dec. Lei 45185 de 17 de Setembro e código do direito de autor e direitos conexos.

TUU.BUILDING DESIGN MANAGEMENT
arquitetura@tuu.pt www.tuu.pt

CABO DE BUS KNX Y(ST)Y - 2x2x0,8mm²
Hager TG018 ou equivalente

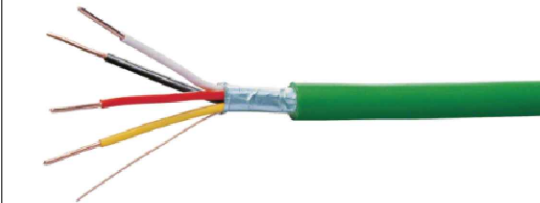

EQUIPAMENTOS PROPOSTOS:




TXD505
Det. mov. Corredor 360° encast. KNX



TXD503
Det. pres. Standard 360° encast. KNX



TXD501
Det. pres. Mini 360° encast. KNX

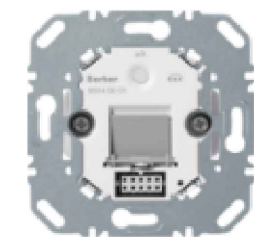

80040001
BAU (Easy)



80142321
BP KNX Q.x 2 teclas Easy p-etiq, alu




80141321
BP KNX Q.x 1 tecla Easy p-etiq, alu



TYFS672D
Gateway DALI/KNX Secure, 2 canais



TYA604C
Actuador bin./est. 4 canais 16A KNX-S

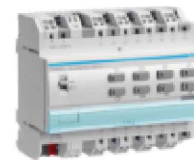



TYA608C
Actuador bin./est. 8 canais 16 KNX-S



TJAS471
domovea plus

LEGENDA KNX	
	BOTÃO DE PRESSÃO, KNX 1 TECLA / 2 FUNÇÕES
	BOTÃO DE PRESSÃO, KNX 2 TECLAS / 4 FUNÇÕES
	BOTÃO DE PRESSÃO, KNX 4 TECLAS / 8 FUNÇÕES
	DETECTOR DE PRESENÇA KNX 360º DE ENCASTRAR, HAGER TXD501 (Mini), OU EQUIVALENTE (até Ø10mm)
	DETECTOR DE PRESENÇA KNX 360º DE ENCASTRAR, HAGER TXD503, OU EQUIVALENTE (até Ø20mm)
	DETECTOR DE MOVIMENTO KNX 360º DE ENCASTRAR, HAGER TXD505 (Corredores), OU EQUIVALENTE (até 30m x 5m)
	Cabo de BUS KNX Y(ST)Y - 2x2x0,8mm², enfiado em tubo ou em caminhos de cabos.

CABO DE BUS KNX Y(ST)Y - 2x2x0,8mm²
Hager TG018 ou equivalente

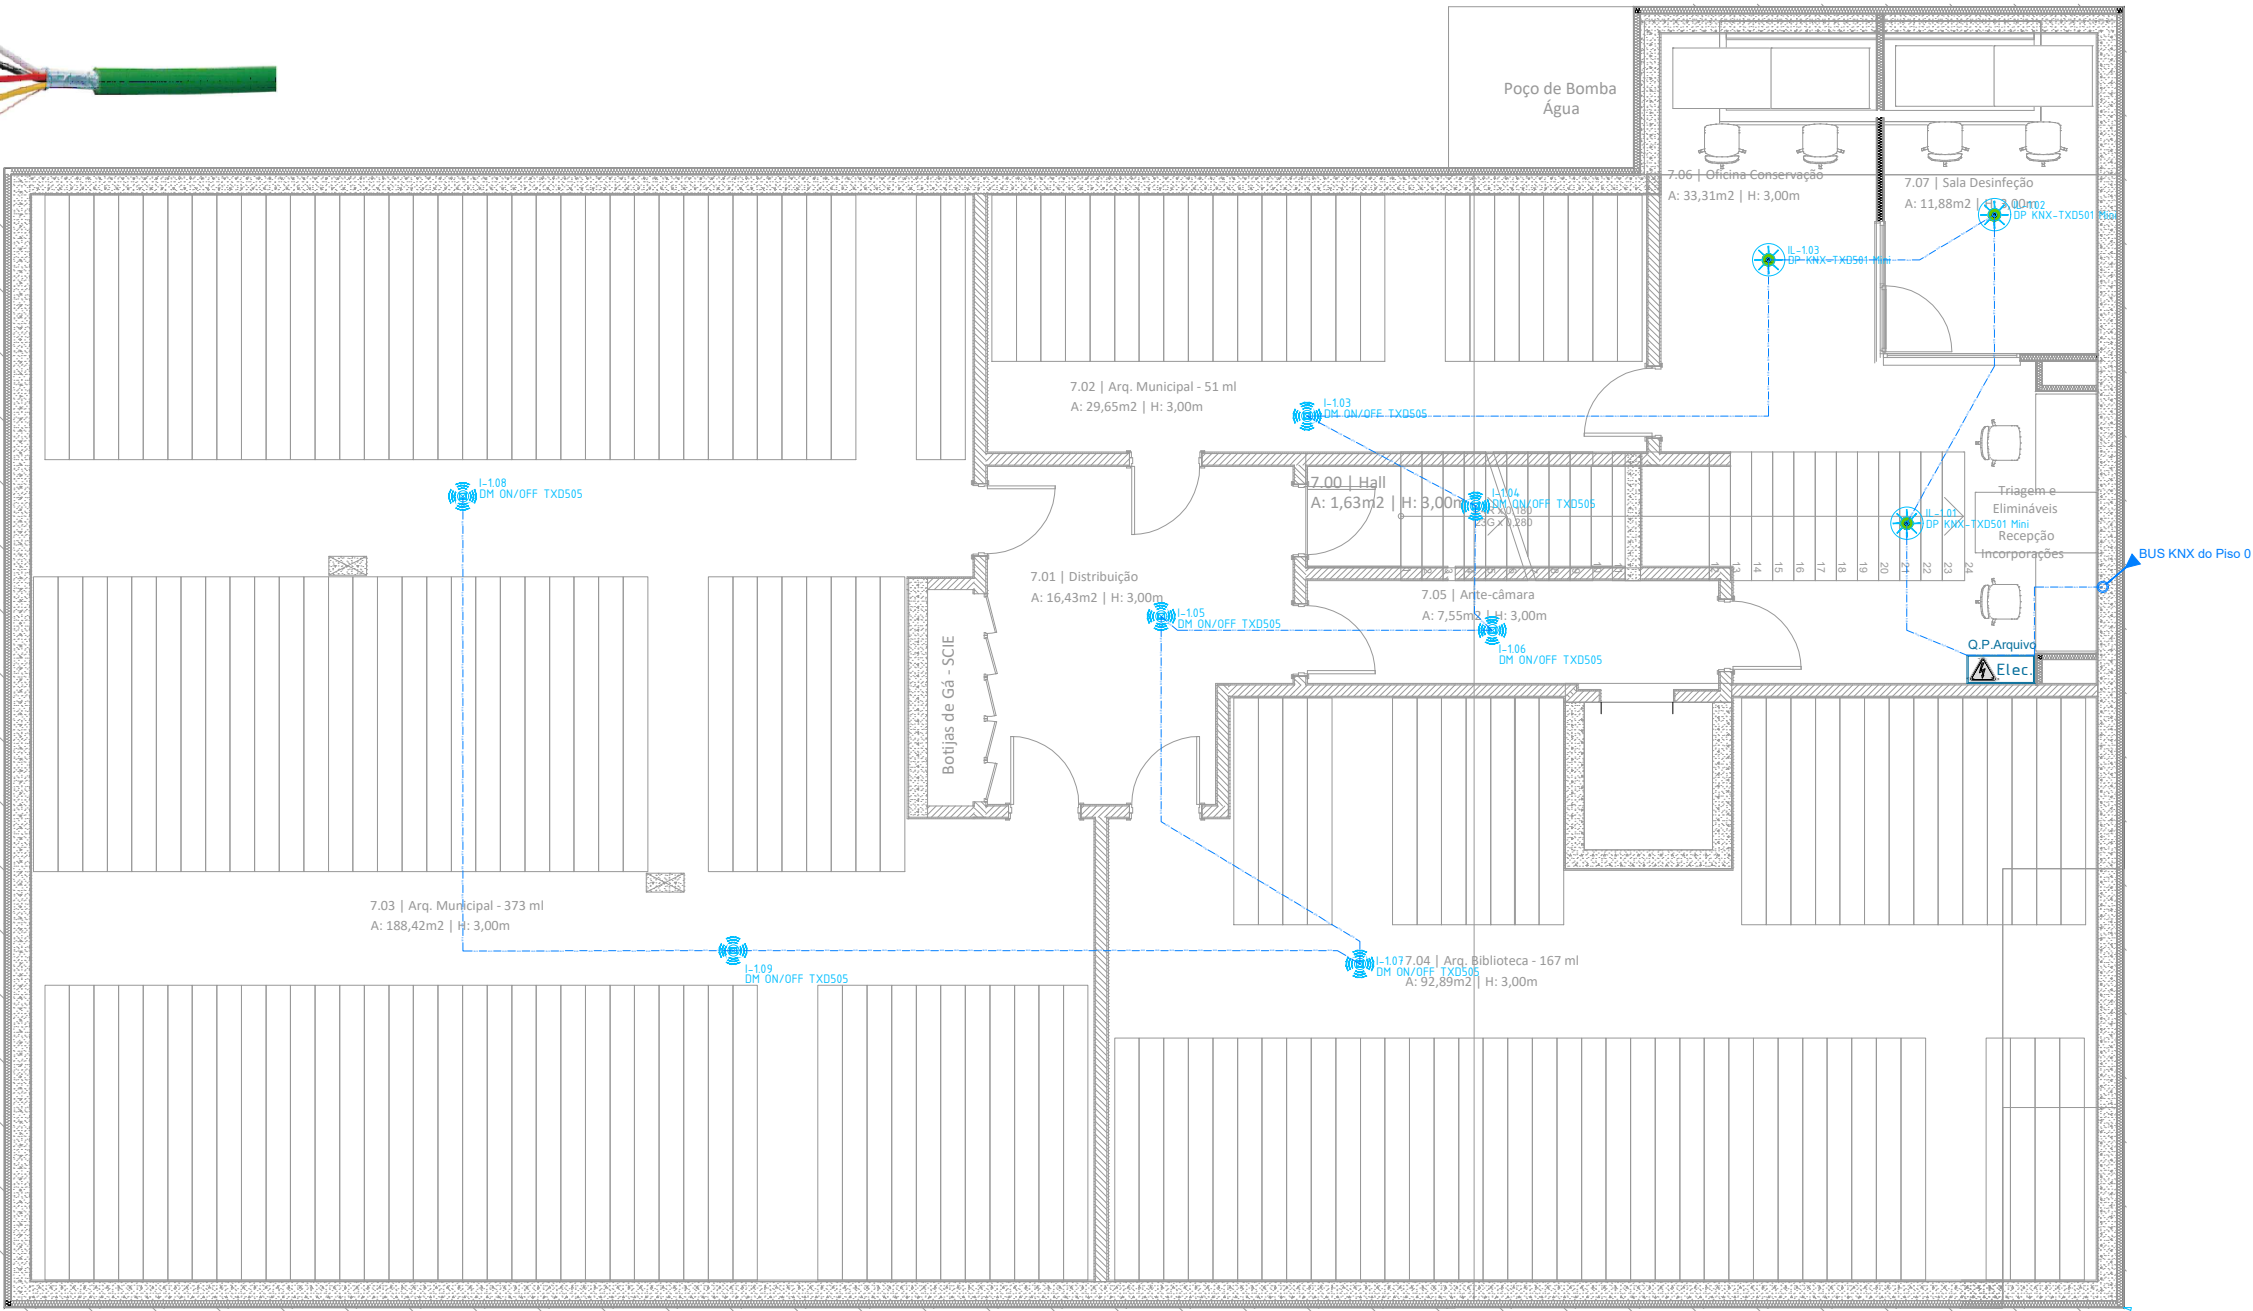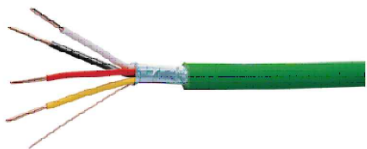

Revisão	Descrição	Data
01	Modificações diversas	21.01.2026
00	Entrega do Projeto de Execução	19.12.2025

TUU

Requerente
CÂMARA MUNICIPAL DE CANTANHEDE
Projeto
REQUALIFICAÇÃO E MODERNIZAÇÃO DA BIBLIOTECA MUNICIPAL DE CANTANHEDE

RUA EXEMPLO 11
0000-004 CANTANHEDE

Especialidade
PROJETO DA INSTALAÇÃO ELÉTRICA

PROJETO DE EXECUÇÃO

Designação
PLANTA DE EQUIPAMENTOS E BUS KNX - PISO -1

JANEIRO 2026
1:100

EL014

Observações
ESTE PROJETO DEVERÁ SER LIDO EM CONJUNTO COM AS PEÇAS ESCRITAS, ASSIM COMO, O PROJETO DE ARQUITETURA E AS RESTANTES ESPECIALIDADES.
QUAISQUER DISCREPÂNCIAS DEVERÃO SER COMUNICADAS AO PROJETISTA. TODAS AS MEDIDAS DESTES DESENHOS SÃO DE PROJETO E MERAMENTE INDICATIVAS, NECESSITAM SER RETIFICADAS EM OBRA.

Nome Ficheiro
BIBLICA_PE_ELE_PD_V0.DWG

Código
39962025

Equipa
ANA EXEMPLO | ENG ELETROTÉCNICO
LUIS BALSAS | ENG ELETROTÉCNICO

Reprodução proibida, Dec. Lei 45/85 de 17 de Setembro e código do direito de autor e direitos conexos.


TUU.BUILDING DESIGN MANAGEMENT

arquitetura@tuu.pt www.tuu.pt



TXD505

Det. mov. Corredor
360° encast. KNX

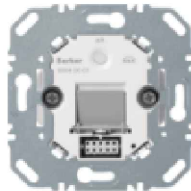

80040001
BAU (Easy)



TXD503

Det. pres. Standard
360° encast. KNX



80142321
BP KNX Q.x 2 teclas Easy p-etiq, alu




TXD501

Det. pres. Mini 360°
encast. KNX



80141321
BP KNX Q.x 1 tecla Easy p-etiq, alu

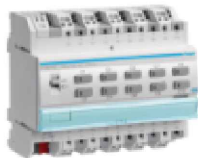

TYA610C


Actuador bin./est. 10
canais 16 KNX-S

LEGENDA KNX

	BOTÃO DE PRESSÃO, KNX 1 TECLA / 2 FUNÇÕES
	BOTÃO DE PRESSÃO, KNX 2 TECLAS / 4 FUNÇÕES
	BOTÃO DE PRESSÃO, KNX 4 TECLAS / 8 FUNÇÕES
	DETECTOR DE PRESENÇA KNX 360° DE ENCASTRAR, HAGER TXD501 (Mini), OU EQUIVALENTE (até Ø10m)
	DETECTOR DE PRESENÇA KNX 360° DE ENCASTRAR, HAGER TXD503, OU EQUIVALENTE (até Ø20m)
	DETECTOR DE MOVIMENTO KNX 360° DE ENCASTRAR, HAGER TXD505 (Corredores), OU EQUIVALENTE (até 30m x 5m)
	Cabo de BUS KNX Y(ST)Y - 2x2x0,8mm², enfiado em tubo ou em caminhos de cabos.



*AL - Alimentação do Bloco Autónomo feita a partir do circuito de iluminação local

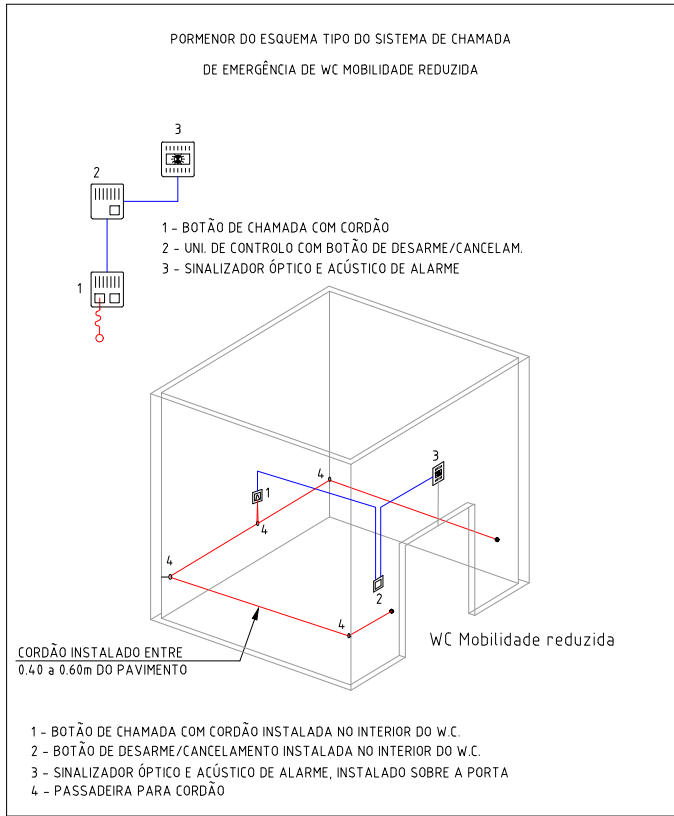

LEGENDA:

	QUADRO ELÉTRICO DO EDIFÍCIO
	TOMADA ELÉTRICA 2P+T, 16A, USOS GERAIS - ENCASTRAR
	TOMADA ELÉTRICA 2P+T, 16A, ESTANQUE IP55 - ENCASTRAR
	TOMADA ELÉTRICA 2P+T, 16A, ENCASTRAR, C/TAMPA IP44
	TOMADA ELÉTRICA 2P+T, 16A, ESTANQUE IP55 - SALIENTE
	CAIXA DE CHÃO 2 MÓDULOS (1xTOM 2P+T)
	CAIXA DE CHÃO DE 12 MÓDULOS (3xTOM 2P+T + 2xTOM 2P+T (UPS) + 2xRJ45 Cat6)
	ALIMENTAÇÃO ELÉTRICA ESPECÍFICA DE EQUIPAMENTO
	(Dimensões e altura, ver planta)
	BLOCO AUTÔNOMO PERMANENTE
	BLOCO AUTÔNOMO NÃO PERMANENTE
	LUMINÁRIA DE ENCASTRAR NO TETO, DO TIPO TROMILUX, SÉRIE 4526 DALI, DIMENSÃO L=1975mm, L5, L1=1300 ou L5, L2=1000mm, 4000K
	LUMINÁRIA SUSPensa DE TETO, DO TIPO TROMILUX, SÉRIE 4556 DALI, DIMENSÃO 1975mm, 4000K
	LUMINÁRIA SALIENTE DE PAREDE, DO TIPO TROMILUX, SÉRIE 4028, DIMENSÃO 1220mm, NA VERTICAL, 4000K
	LUMINÁRIA DO TIPO PANEL LED, DE ENCASTRAR NO TETO, TROMILUX, SÉRIE 5550 DALI, 595x595mm, 30W 4000K (P30 R02)
	LUMINÁRIA DE ENCASTRAR COM ABA DE REMATE, DO TIPO TROMILUX, SÉRIE 5511 DALI, DIMENSÃO 965mm, 4000K
	LUMINÁRIA SUSPensa DE TETO LINEAR, TROMILUX, DA SÉRIE 4052, 4000K
	LUMINÁRIA DE ENCASTRAR NO TETO, DO TIPO DOWNLIGHT SEM ABA DE REMATE, TROMILUX, SÉRIE 9075, Ø114mm, 4000K
	LUMINÁRIA DE ENCASTRAR NO TETO, DO TIPO DOWNLIGHT COM ABA DE REMATE, TROMILUX, SÉRIE 5511, Ø265mm, 4000K
	LUMINÁRIA SUSPensa DE TETO, DO TIPO TROMILUX, SÉRIE 4556, DIMENSÃO 2800mm, 4000K
	LUMINÁRIA DE PAREDE SALIENTE, DO TIPO APLIQUE, TROMILUX, SÉRIE 2076, LUX ASCENDENTE E DESCENDENTE, IP54, 42W, 4000K
	LINHA DE LUZ CONTÍNUA, TROMILUX, SÉRIE 4010, APLICAÇÃO EM SANCA, 4000K
	DETECTOR DE MOVIMENTO 360º DE ENCASTRAR, HAGER EE8054, OU EQUIVALENTE
	BORNE DUPLO DE CARREGAMENTO VEÍCULOS ELÉTRICOS

01	Identificações diversas	21.01.2025
00	Entrada do Projeto de Execução	19.12.2025
Revisão	Descrição	Data

TUU

Requerente
CÂMARA MUNICIPAL DE CANTANHEDE
Projeto
REQUALIFICAÇÃO E MODERNIZAÇÃO DA BIBLIOTECA MUNICIPAL DE CANTANHEDE

RUA EXEMPLO 11
0000-004 CANTANHEDE

Especialidade
PROJETO DA INSTALAÇÃO ELÉTRICA

PROJETO DE EXECUÇÃO

Designação
PLANTA DE ILUMINAÇÃO E CHAMADA DE EMERGÊNCIA PISO 0
JANEIRO 2026
1:100

EL015

Observações
ESTE PROJETO DEVERÁ SER LIDO EM CONJUNTO COM AS PEÇAS ESCRITAS, ASSIM COMO, O PROJETO DE ARQUITETURA E AS RESTANTES ESPECIALIDADES. QUAISQUER DISCREPÂNCIAS DEVERÃO SER COMUNICADAS AO PROJETISTA. TODAS AS MEDIDAS DESTES DESENHOS SÃO DE PROJETO E MERAMENTE INDICATIVAS, NECESSITAM SER RETIFICADAS EM OBRA.

Nome Ficheiro
BIBLICA_PE_ELE_PD_V0.DWG

Código
39962025

Equipa
ANA EXEMPLO | ENG ELETROTÉCNICO
LUIS BALSAS | ENG ELETROTÉCNICO

Reprodução proibida, Dec. Lei 45185 de 17 de Setembro e código do direito de autor e direitos conexos.

TUU.BUILDING DESIGN MANAGEMENT

arquitetura@tuu.pt

www.tuu.pt

01	Modificações diversas	21.01.2026
00	Entrega do Projeto de Execução	19.12.2025
Revisão	Descrição	Data

TUU

Requerente
CÂMARA MUNICIPAL DE CANTANHEDE
Projeto
REQUALIFICAÇÃO E MODERNIZAÇÃO DA BIBLIOTECA MUNICIPAL DE CANTANHEDE
RUA EXEMPLO 11
0000-004 CANTANHEDE

Especialidade
PROJETO DA INSTALAÇÃO ELÉTRICA

PROJETO DE EXECUÇÃO

Designação
PLANTA DE ILUMINAÇÃO DE EMERGÊNCIA
PISO -1
JANEIRO 2026
1:100

EL016

Observações
ESTE PROJETO DEVERÁ SER LIDO EM CONJUNTO COM AS PEÇAS ESCRITAS, ASSIM COMO, O PROJETO DE ARQUITETURA E AS RESTANTES ESPECIALIDADES.
QUAISQUER DISCREPÂNCIAS DEVERÃO SER COMUNICADAS AO PROJETISTA. TODAS AS MEDIDAS DESTES DESENHO SÃO DE PROJETO E MERAMENTE INDICATIVAS, NECESSITAM SER RETIFICADAS EM OBRA.

Nome Ficheiro
BIBLICA_PE_ELE_PD_V0.DWG


Código
39962025

Equipa
ANA EXEMPLO | **ENG ELETROTÉCNICO**
LUIS BALSAS | **ENG ELETROTÉCNICO**


Reprodução proibida, Dec. Lei 45/85 de 17 de Setembro e código do direito de autor e direitos conexos.

TUU.BUILDING DESIGN MANAGEMENT

arquitetura@tuu.pt www.tuu.pt

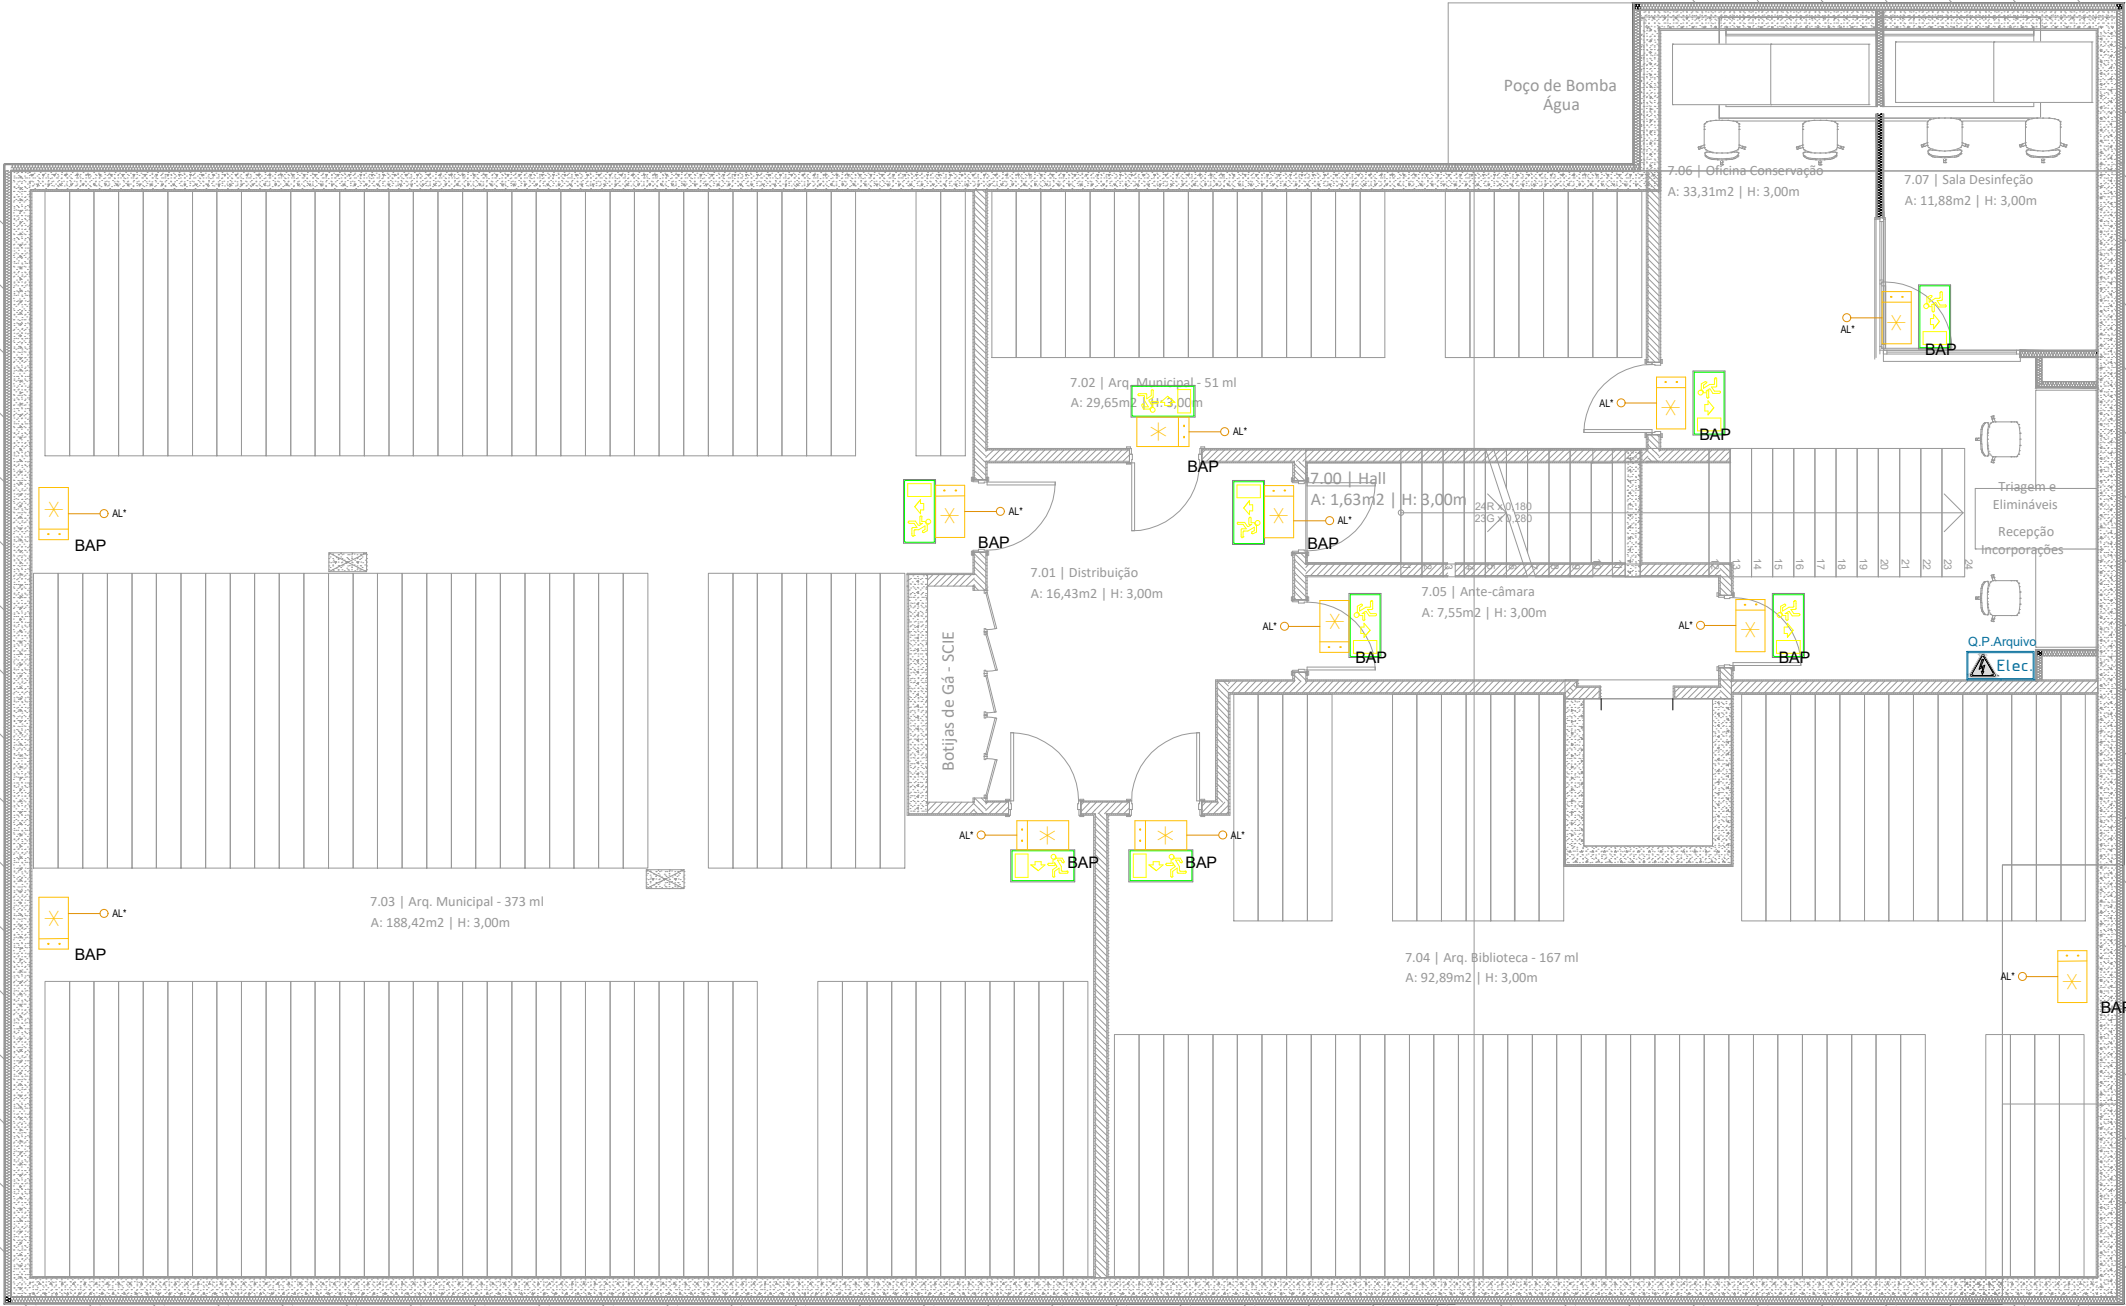

*AL - Alimentação do Bloco Autónomo feita a partir do circuito de iluminação local

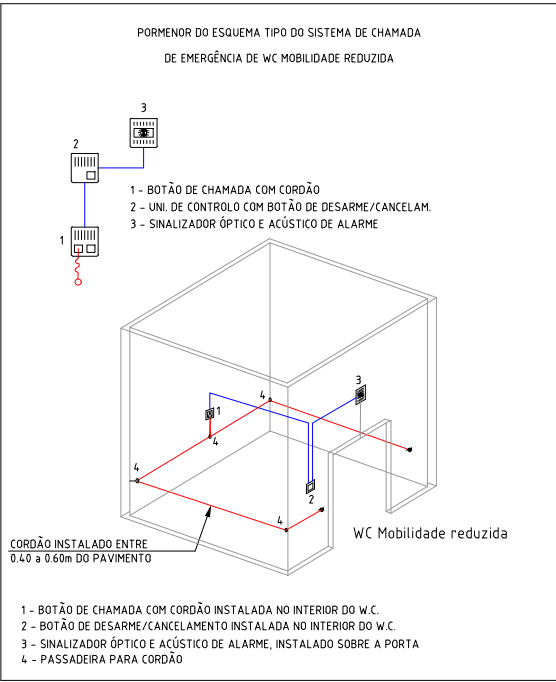

LEGENDA:	
	QUADRO ELÉTRICO DO EDIFÍCIO
	TOMADA ELÉTRICA 2P+T, 16A, USOS GERAIS - ENCASTRAR
	TOMADA ELÉTRICA 2P+T, 16A, ESTANQUE IP55 - ENCASTRAR
	TOMADA ELÉTRICA 2P+T, 16A, ENCASTRAR, C/TAMPA IP44
	TOMADA ELÉTRICA 2P+T, 16A, ESTANQUE IP55 - SALIENTE
	CAIXA DE CHÃO 2 MÓDULOS (1xTOM 2P+T)
	CAIXA DE CHÃO DE 12 MÓDULOS (3xTOM 2P+T + 2xTOM 2P+T (UPS) + 2xRJ45 Cat6)
	ALIMENTAÇÃO ELÉTRICA ESPECÍFICA DE EQUIPAMENTO
	BLOCO AUTÓNOMO PERMANENTE (Lx35mm)
	BLOCO AUTÓNOMO NÃO PERMANENTE



LEGENDA SADI:		
	CENTRAL DE DETEÇÃO DE INCÊNDIO CONVENCIONAL - Zonas EQUIPADA COM MÓDULO DE COMUNICAÇÃO	
	DETECTOR ÓTICO DE FUMO	
	DETECTOR ÓTICO DE FUMO NO TETO FALSO	
	DETECTOR TÉRMICO DE INCÊNDIO	
	BOTONEIRA MANUAL DE ALARME DE INCÊNDIO	
	SIRENE DE ALARME DE INCÊNDIO COM FLASH	
	INDICADOR DE AÇÃO LUMINOSO - ALARME DE INCÊNDIO	
	CABO JE-(S)JH BD FE 180 2x2x0,8mm², EM TUBO VDISISGRIS Ø20mm	
	MÓDULO DE COMANDO INFARCE (CDI - ELEVADORES)	
	BOTONEIRA DE CORTE GERAL DE ENERGIA (Edifício)	
	BOTONEIRA DE CORTE LOCAL DE ENERGIA (Local)	

Revisão	Descrição	Data
01	Modificações diversas	21.01.2026
00	Entrada do Projeto de Execução	19.12.2025

TUU

Requerente
CÂMARA MUNICIPAL DE CANTANHEDE
Projeto
REQUALIFICAÇÃO E MODERNIZAÇÃO DA BIBLIOTECA MUNICIPAL DE CANTANHEDE
RUA EXEMPLO 11
0000-004 CANTANHEDE

Especialidade
PROJETO DA INSTALAÇÃO ELÉTRICA

PROJETO DE EXECUÇÃO

Designação
PLANTA SISTEMA DE ALARME E DETEÇÃO DE INCÊNDIO PISO 0
JANEIRO 2026
1:100

EL017

Observações
ESTE PROJETO DEVERÁ SER LIDO EM CONJUNTO COM AS PEÇAS ESCRITAS, ASSIM COMO, O PROJETO DE ARQUITECTURA E AS RESTANTES ESPECIALIDADES.
QUAISQUER DISCREPÂNCIAS DEVERÃO SER COMUNICADAS AO PROJETISTA. TODAS AS MEDIDAS DESTES DESENHOS SÃO DE PROJETO E MERAMENTE INDICATIVAS, NECESSITAM SER RETIFICADAS EM OBRA.

Nome Ficheiro
BIBLICA_PE_ELE_PD_V0.DWG

Código
39962025

Equipa
ANA EXEMPLO | ENG ELETROTÉCNICO
LUIS BALSAS | ENG ELETROTÉCNICO

Reprodução proibida, Dec. Lei 45185 de 17 de Setembro e código do direito de autor e direitos conexos.

TUU.BUILDING DESIGN MANAGEMENT
arquitetura@tuu.pt www.tuu.pt

01	Modificações diversas	21.01.2026
00	Entrega do Projeto de Execução	19.12.2025
Revisão	Descrição	Data

TUU

Requerente
CÂMARA MUNICIPAL DE CANTANHEDE
Projeto
REQUALIFICAÇÃO E MODERNIZAÇÃO DA BIBLIOTECA MUNICIPAL DE CANTANHEDE
RUA EXEMPLO 11
0000-004 CANTANHEDE

Especialidade
PROJETO DA INSTALAÇÃO ELÉTRICA

PROJETO DE EXECUÇÃO

Designação
PLANTA SISTEMA DE ALARME E DETEÇÃO DE INCÊNDIO PISO -1
JANEIRO 2026
1:100

EL018

Observações
ESTE PROJETO DEVERÁ SER LIDO EM CONJUNTO COM AS PEÇAS ESCRITAS, ASSIM COMO, O PROJETO DE ARQUITETURA E AS RESTANTES ESPECIALIDADES.
QUAISQUER DISCREPÂNCIAS DEVERÃO SER COMUNICADAS AO PROJETISTA. TODAS AS MEDIDAS DESTES DESENHOS SÃO DE PROJETO E MERAMENTE INDICATIVAS, NECESSITAM SER RETIFICADAS EM OBRA.


Nome Ficheiro
BIBLICA_PE_ELE_PD_V0.DWG

Código
39962025

Equipa
ANA EXEMPLO | ENG ELETROTÉCNICO
LUIS BALSAS | ENG ELETROTÉCNICO


Reprodução proibida, Dec. Lei 45/85 de 17 de Setembro e código do direito de autor e direitos conexos.

TUU.BUILDING DESIGN MANAGEMENT
arquitetura@tuu.pt www.tuu.pt

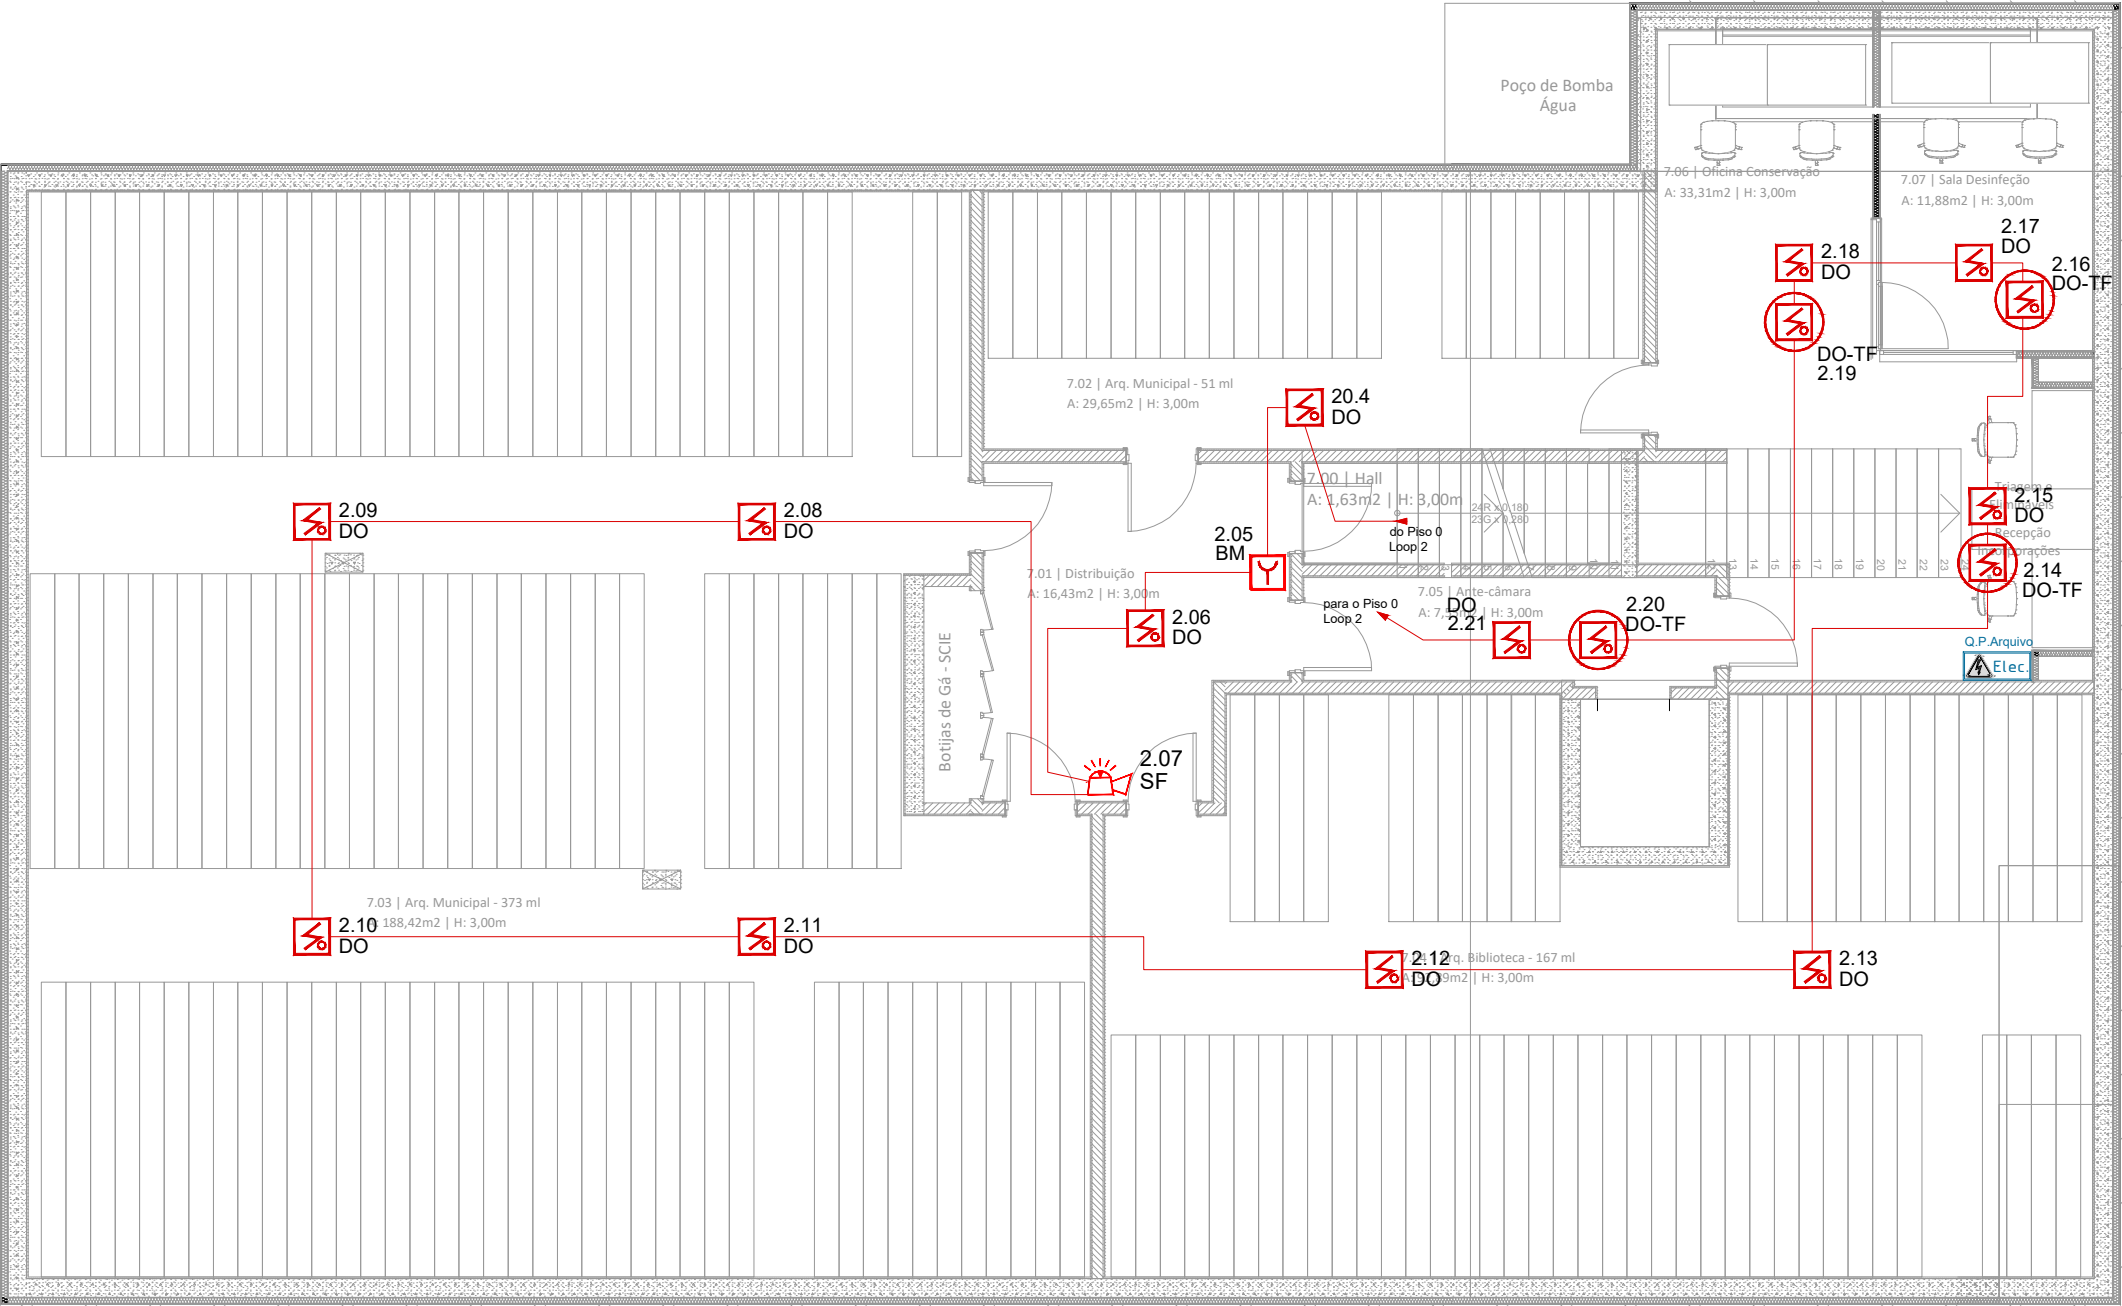

LEGENDA SADI:

	CENTRAL DE DETEÇÃO DE INCÊNDIO CONVENCIONAL *Zonas EQUIPADA COM MÓDULO DE COMUNICAÇÃO
	DETECTOR ÓTICO DE FUMO
	DETECTOR ÓTICO DE FUMO NO TETO FALSO
	DETECTOR TÉRMICO DE INCÊNDIO
	BOTONEIRA MANUAL DE ALARME DE INCÊNDIO
	SIRENE DE ALARME DE INCÊNDIO COM FLASH
	INDICADOR DE AÇÃO LUMINOSO - ALARME DE INCÊNDIO
	CABO JE-(St)H BD FE180 2x2x0,8mm², EM TUBO VD/ISOGRIS Ø20mm
	MÓDULO DE COMANDO INFARCE (CDI - ELEVADORES)
	BOTONEIRA DE CORTE GERAL DE ENERGIA (Edifício)
	BOTONEIRA DE CORTE LOCAL DE ENERGIA (Local)

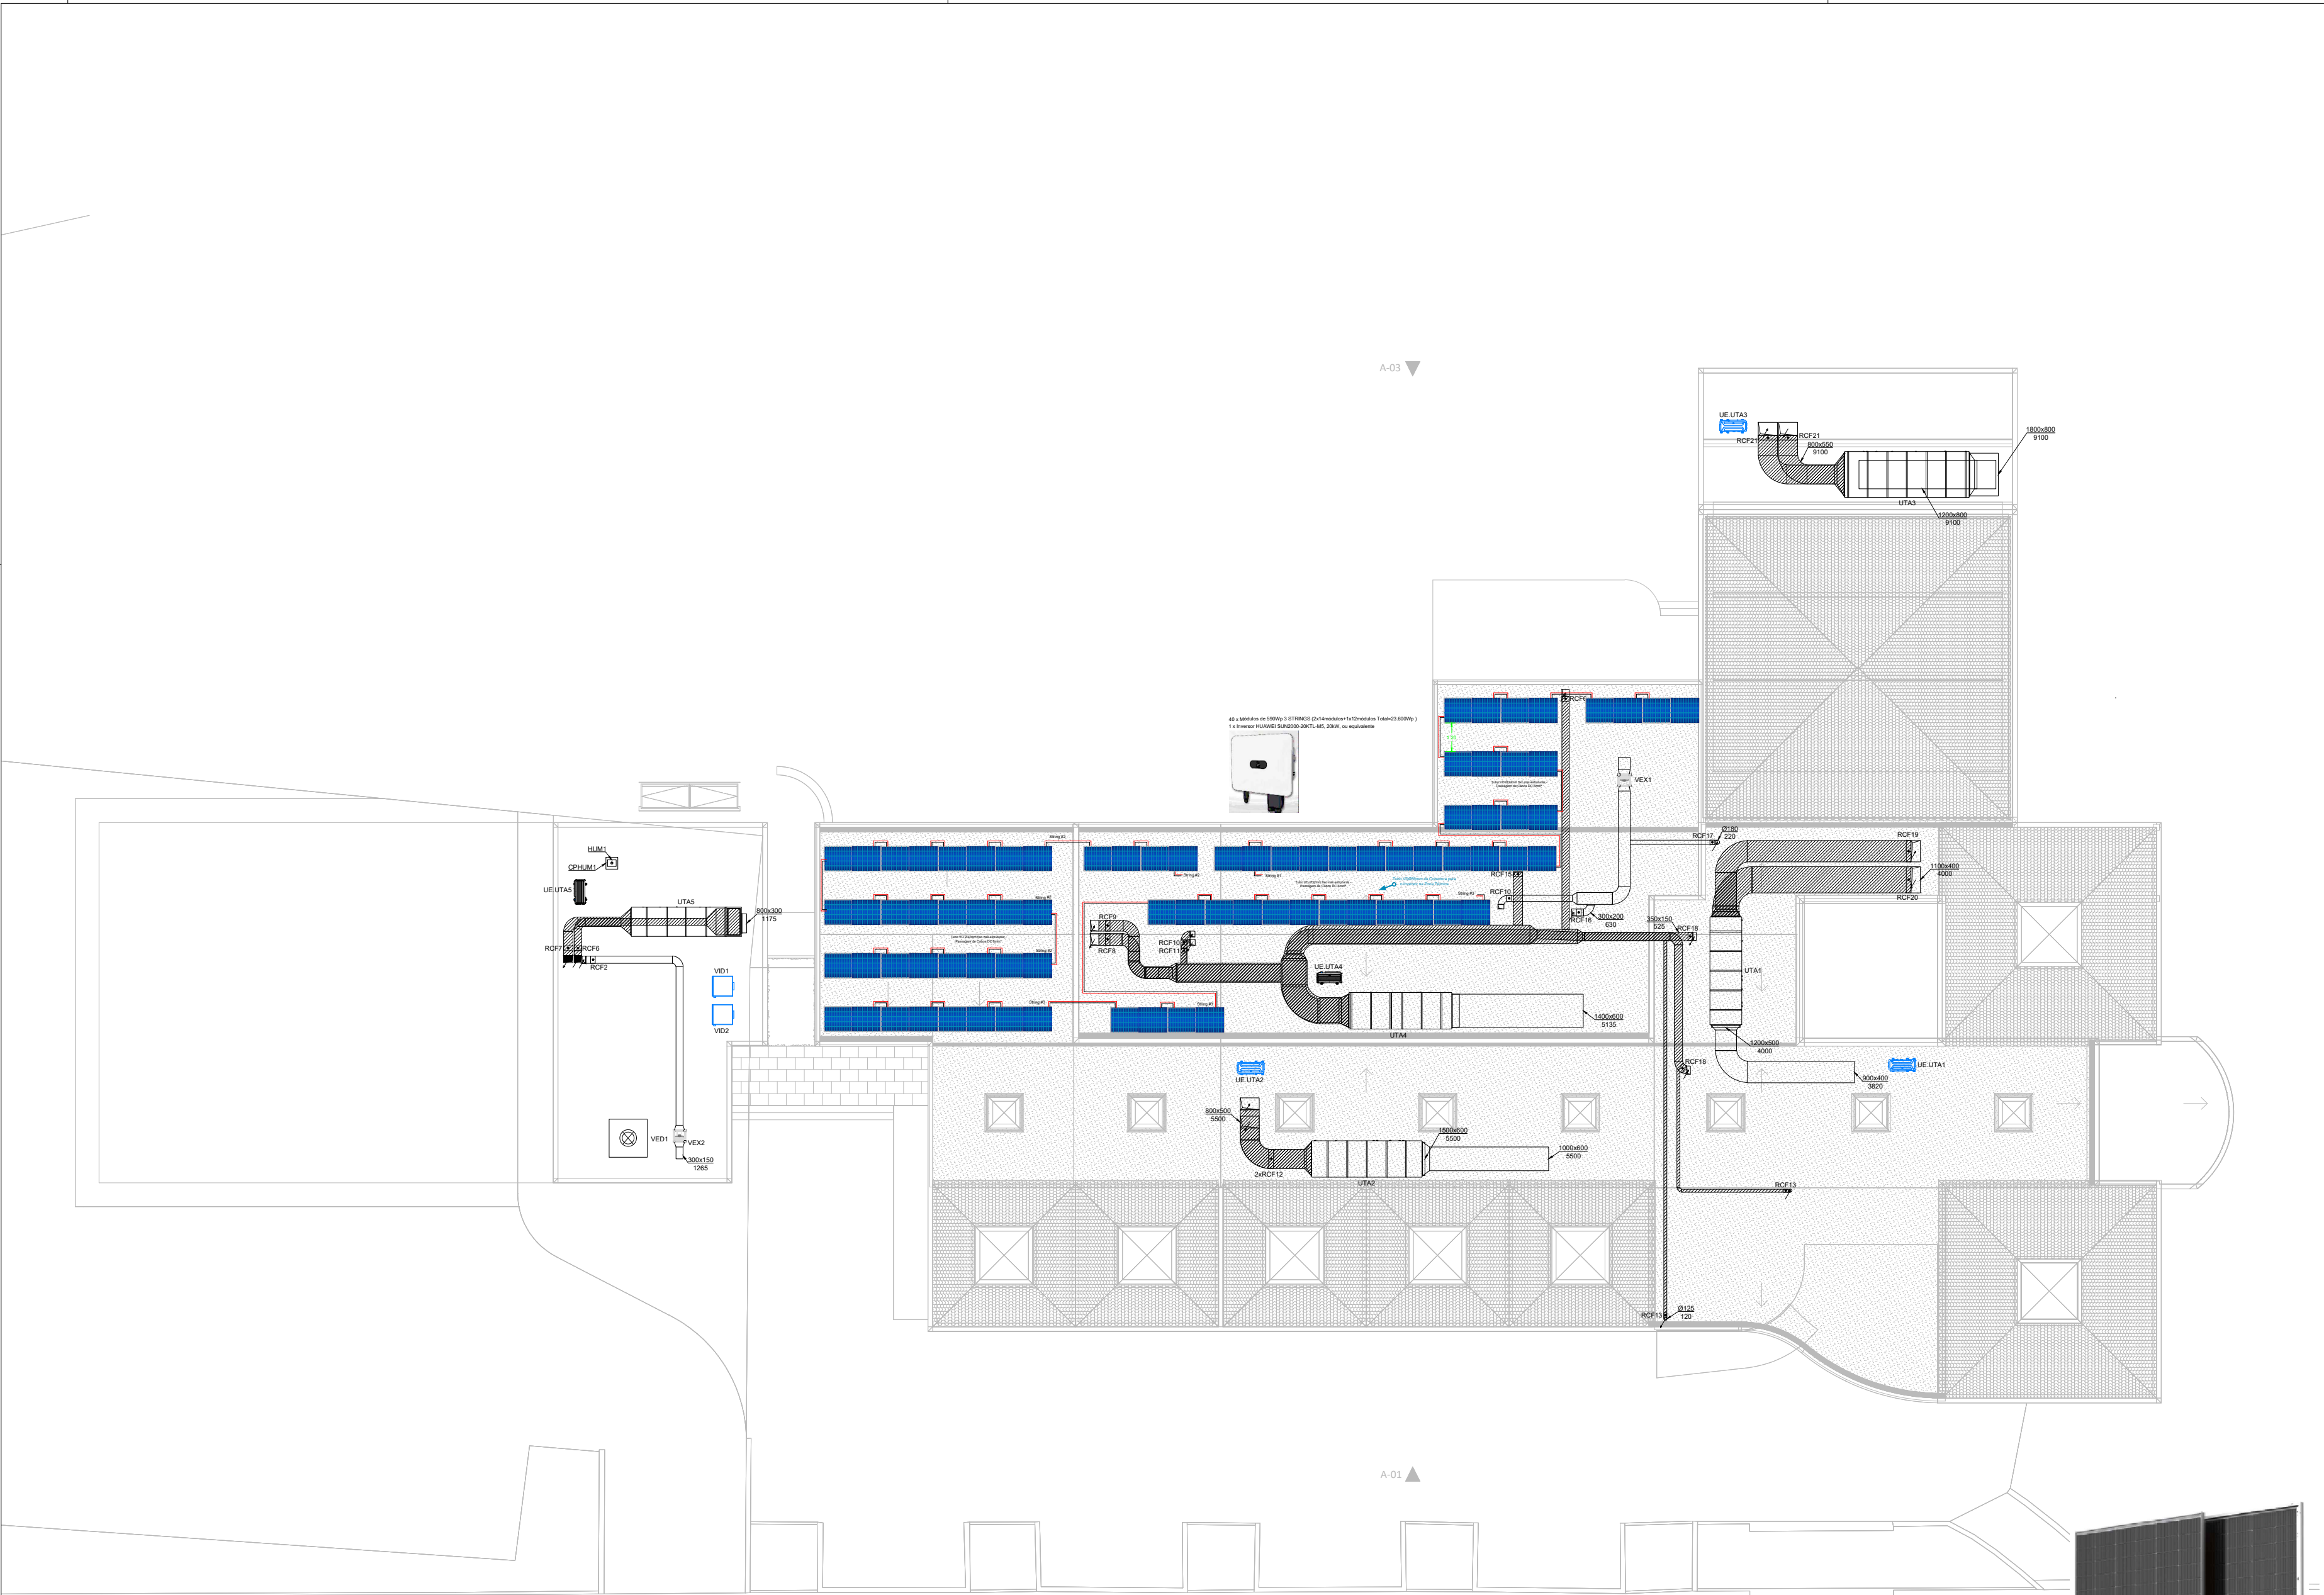

01	Modificações diversas	21.01.2026
00	Entrada do Projeto de Execução	19.12.2025
Revisão	Descrição	Data

TUU

Requerente
CÂMARA MUNICIPAL DE CANTANHEDE
Projeto
REQUALIFICAÇÃO E MODERNIZAÇÃO DA BIBLIOTECA MUNICIPAL DE CANTANHEDE
RUA EXEMPLO 11
0000-004 CANTANHEDE

Especialidade
PROJETO DA INSTALAÇÃO ELÉTRICA

Designação
PLANTA DA INSTALAÇÃO FOTOVOLTAICA COBERTURA
JANEIRO 2026
1:100

EL019

Observações
ESTE PROJETO DEVERÁ SER LIDO EM CONJUNTO COM AS PEÇAS ESCRITAS, ASSIM COMO, O PROJETO DE ARQUITETURA E AS RESTANTES ESPECIALIDADES.
QUAISQUER DISCREPÂNCIAS DEVERÃO SER COMUNICADAS AO PROJETISTA. TODAS AS MEDIDAS DESTES DESENHOS SÃO DE PROJETO E MERAMENTE INDICATIVAS, NECESSITAM SER RETIFICADAS EM OBRA.

Nome Ficheiro
BIBLICA_PE_ELE_PD_V0.DWG

Código
39962025

Equipa
ANA EXEMPLO | ENG ELETROTÉCNICO
LUIS BALSAS | ENG ELETROTÉCNICO

Reprodução proibida, Dec. Lei 45185 de 17 de Setembro e código do direito de autor e direitos conexos.


TUU.BUILDING DESIGN MANAGEMENT
arquitetura@tuu.pt www.tuu.pt



Inversor HUAWEI SUN2000-20KTL-M5, 20kW, ou equivalente



Estrutura de Fixação SUNFER 29H, ou equivalente

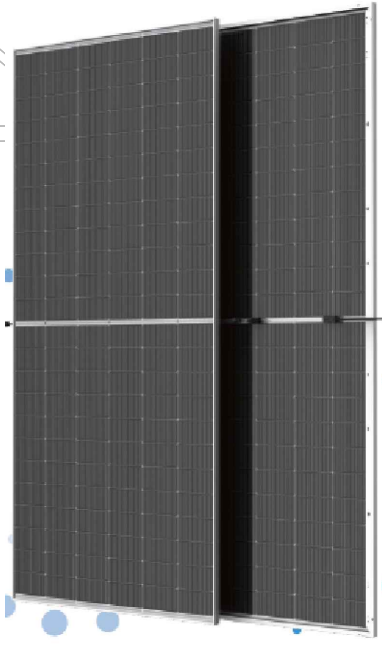

Módulos TrinaSolar TSM-NEG18C.20 de 590Wp



Revisão	Descrição	Data
01	Modificações diversas	21.01.2026
00	Entrega do Projeto de Execução	19.12.2025

TUU

Requerente
CÂMARA MUNICIPAL DE CANTANHEDE
Projeto
REQUALIFICAÇÃO E MODERNIZAÇÃO DA BIBLIOTECA MUNICIPAL DE CANTANHEDE
RUA EXEMPLO 11
0000-004 CANTANHEDE

Especialidade
PROJETO DA INSTALAÇÃO ELÉTRICA

PROJETO DE EXECUÇÃO

Designação
PLANTA DA INSTALAÇÃO FOTOVOLTAICA - PISO 0

JANEIRO 2026
1:100

EL020

Observações
ESTE PROJETO DEVERÁ SER LIDO EM CONJUNTO COM AS PEÇAS ESCRITAS, ASSIM COMO, O PROJETO DE ARQUITETURA E AS RESTANTES ESPECIALIDADES.
QUAISQUER DISCREPÂNCIAS DEVERÃO SER COMUNICADAS AO PROJETISTA. TODAS AS MEDIDAS DESTES DESENHOS SÃO DE PROJETO E MERAMENTE INDICATIVAS, NECESSITAM SER RETIFICADAS EM OBRA.

Nome Ficheiro
BIBLICA_PE_ELE_PD_V0.DWG

Código
39962025

Equipa
ANA EXEMPLO | ENG ELETROTÉCNICO
LUIS BALSAS | ENG ELETROTÉCNICO

Reprodução proibida, Dec. Lei 45185 de 17 de Setembro e código do direito de autor e direitos conexos.

TUU.BUILDING DESIGN MANAGEMENT
arquitetura@tuu.pt www.tuu.pt

01	Modificações diversas	21.01.2026
00	Entrega do Projeto de Execução	19.12.2025
Revisão	Descrição	Data

TUU

Requerente
CÂMARA MUNICIPAL DE CANTANHEDE
Projeto
REQUALIFICAÇÃO E MODERNIZAÇÃO DA BIBLIOTECA MUNICIPAL DE CANTANHEDE

RU A EKE MP LO 11
000 0-00 4 CANTANHEDE

Especialidade
PROJETO DA INSTALAÇÃO ELÉTRICA

PROJETO DE EXECUÇÃO

Designação
ESQUEMAS DA INSTALAÇÃO FOTOVOLTAICA

JANEIRO 2026
S/E

EL021

Observações

ESTE PROJETO DEVERÁ SER LIDO EM CONJUNTO COM AS PEÇAS ESCRITAS, ASSIM COMO, O PROJETO DE ARQUITETURA E AS RESTANTES ESPECIALIDADES. QUAISQUER DISCREPÂNCIAS DEVERÃO SER COMUNICADAS AO PROJETISTA. TODAS AS MEDIDAS DESTES DESENHO SÃO DE PROJETO E MERAMENTE INDICATIVAS, NECESSITAM SER RETIFICADAS EM OBRA.

Nome Ficheiro
BIBLICA_PE_ELE_PD_V0.DWG

Código
39962025


Equipa
LUIS BALSAS | ENG ELETROTÉCNICO

Reprodução proibida, Dec. Lei 45/85 de 17 de Setembro e código do direito de autor e direitos conexos.

TUU.BUILDING DESIGN MANAGEMENT

arquitetura@tuu.pt

www.tuu.pt

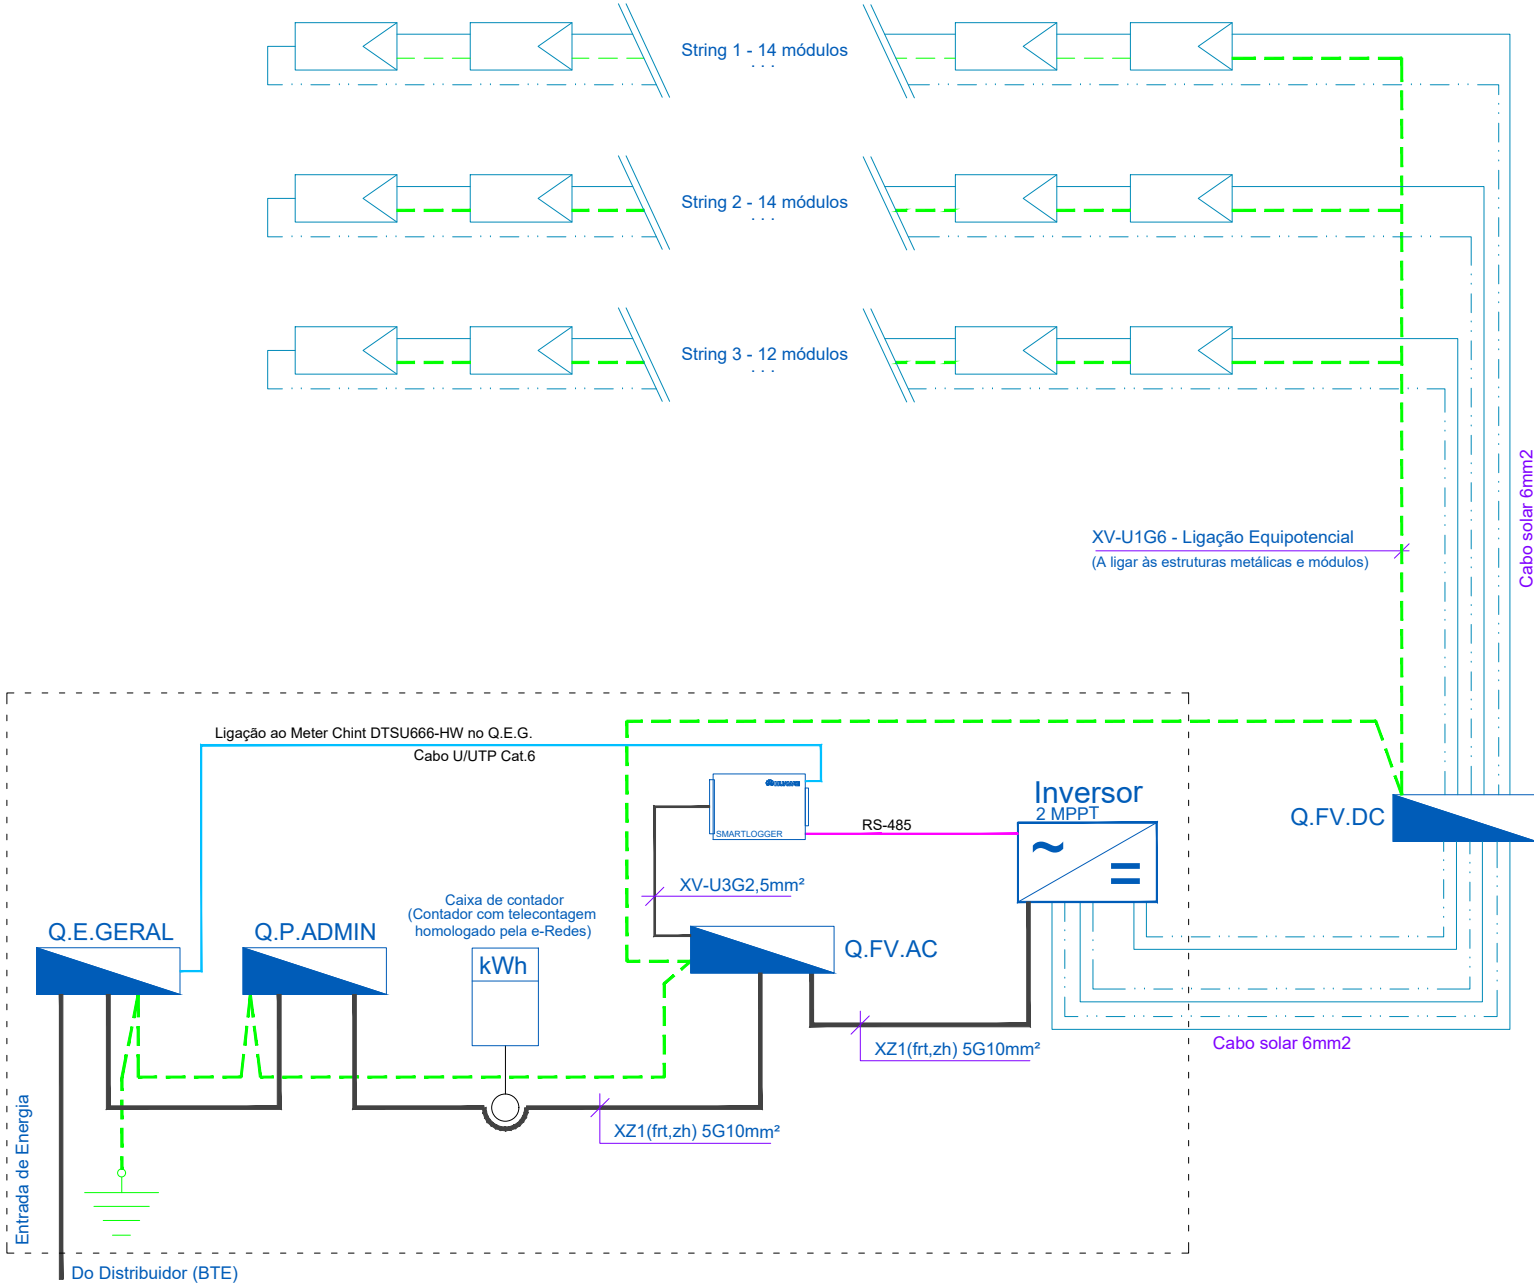

Q.FV.DC


CLASSE II DE ISOLAMENTO
DC (+/-), PE 1000V
IP 65, IK 08

CARACTERÍSTICAS	SÁIDA
XZ1 (ft,zh) R1G10	TERRA DE PROTEÇÃO
2xCabo Solar 4mm² (H1Z2Z2-K 6 mm²)	ENTRADA 1 MPPT_1
2xCabo Solar 4mm² (H1Z2Z2-K 6 mm²)	ENTRADA 2 MPPT_1
2xCabo Solar 4mm² (H1Z2Z2-K 6 mm²)	ENTRADA 3 MPPT_2

Q.FV.AC


CLASSE II DE ISOLAMENTO OU EQUIVALENTE
L1, L2, L3, N, PE - 50Hz 400/230V
In=100A, Icn=8kA, IEC 60947-2, IP 65, IK 08

CARACTERÍSTICAS	SÁIDA
XV-RSG6mm²	P/Q.E.Pec1 Dígitos 4x32A

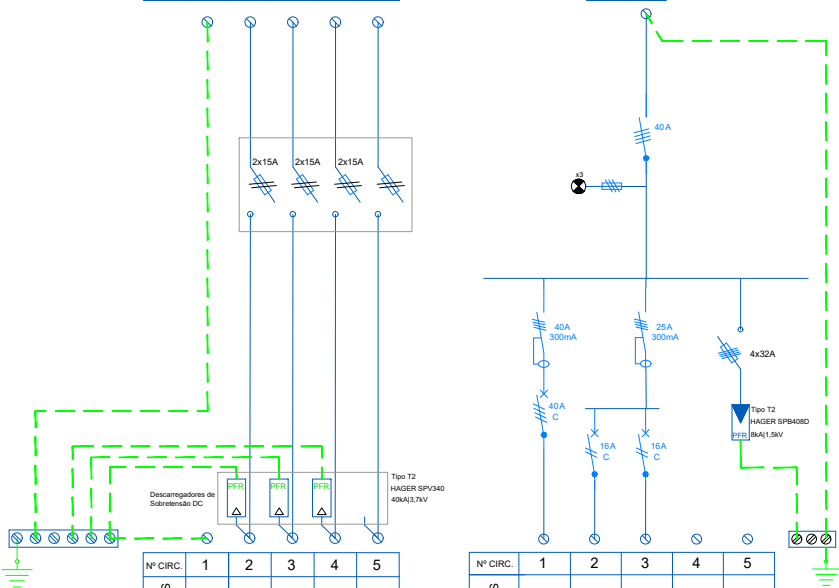

Nº CIRC.	1	2	3	4	5
CARACTERÍSTICAS	XZ1 (ft,zh) R1G10	2xCabo Solar 6mm² (H1Z2Z2-K 6 mm²)	2xCabo Solar 6mm² (H1Z2Z2-K 6 mm²)	2xCabo Solar 6mm² (H1Z2Z2-K 6 mm²)	
ENTRADA	LIGAÇÃO EQUIPOTENCIAL	DA STRING #1	DA STRING #2	DA STRING #3	

Nº CIRC.	1	2	3	4	5
CARACTERÍSTICAS	XV-U1G510mm²	XV-U1G32,5mm²	(RESERVA)	(RESERVA)	
ENTRADA	DO INVERSOR 1	SISTEMA DE MONITORIZAÇÃO	RESERVA	RESERVA	DESCARREGADORES DE SOBRETENSÃO

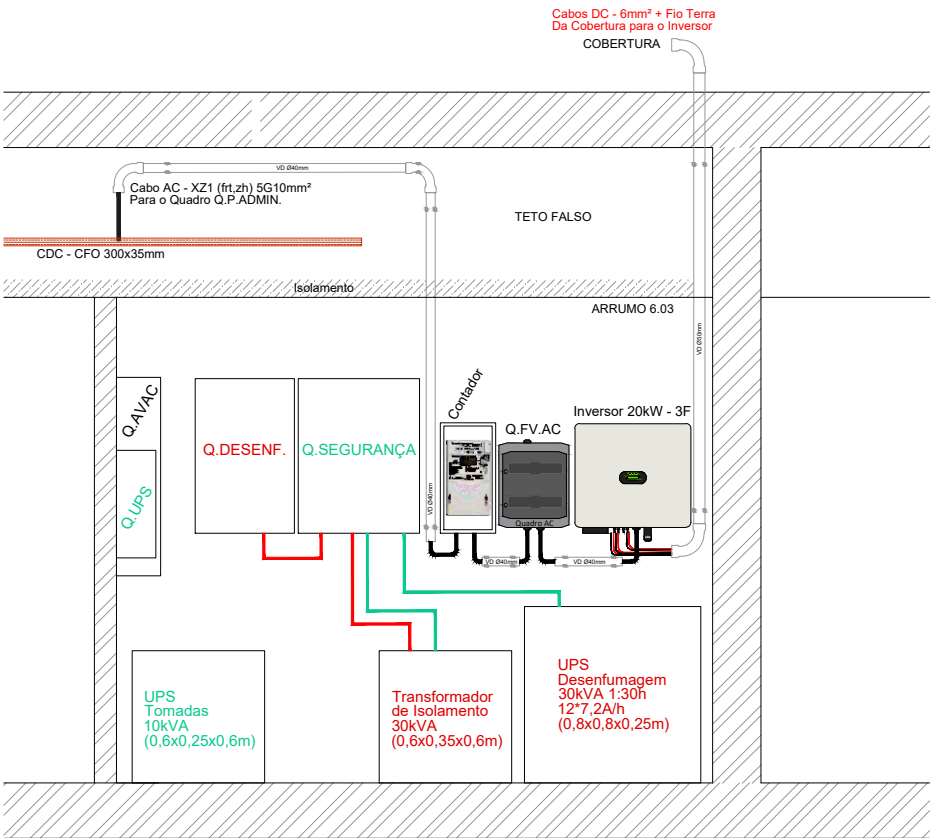

01	Modificações diversas	21.01.2026
00	Entrega do Projeto de Execução	19.12.2025
Revisão	Descrição	Data

TUU

Requerente
CÂMARA MUNICIPAL DE CANTANHEDE
Projeto
REQUALIFICAÇÃO E MODERNIZAÇÃO DA BIBLIOTECA MUNICIPAL DE CANTANHEDE

RUA EXEMPLO 11
000 000 4 CANTANHEDE

Especialidade
PROJETO DA INSTALAÇÃO ELÉTRICA

PROJETO DE EXECUÇÃO

Designação
DIAGRAMA DA REDE ELÉTRICA

JANEIRO 2026
S/E

EL022

Observações
ESTE PROJETO DEVERÁ SER LIDO EM CONJUNTO COM AS PEÇAS ESCRITAS, ASSIM COMO, O PROJETO DE ARQUITETURA E AS RESTANTES ESPECIALIDADES.
QUAISQUER DISCREPÂNCIAS DEVERÃO SER COMUNICADAS AO PROJETISTA. TODAS AS MEDIDAS DESTES DESENHOS SÃO DE PROJETO E MERAMENTE INDICATIVAS, NECESSITAM SER RETIFICADAS EM OBRA.

Nome Ficheiro
BIBLICA_PE_ELE_PD_V0.DWG

Código
39962025

Equipa
Zé A. B. | ENG ELETROTÉCNICO
LUIS BALSAS | ENG ELETROTÉCNICO

Reprodução proibida, Dec. Lei 45/85 de 17 de Setembro e código do direito de autor e direitos conexos.

TUU.BUILDING DESIGN MANAGEMENT

arquitetura@tuu.pt www.tuu.pt




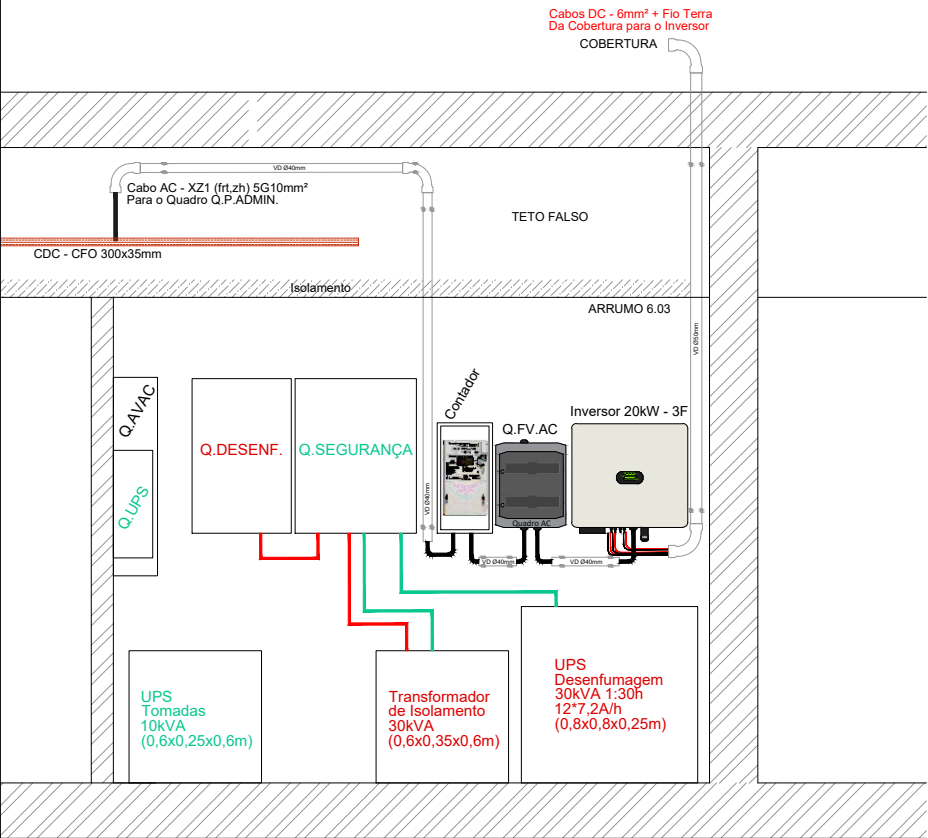


DIAGRAMA DA LIGAÇÃO DO QUADRO DE DESENFUMAGEM

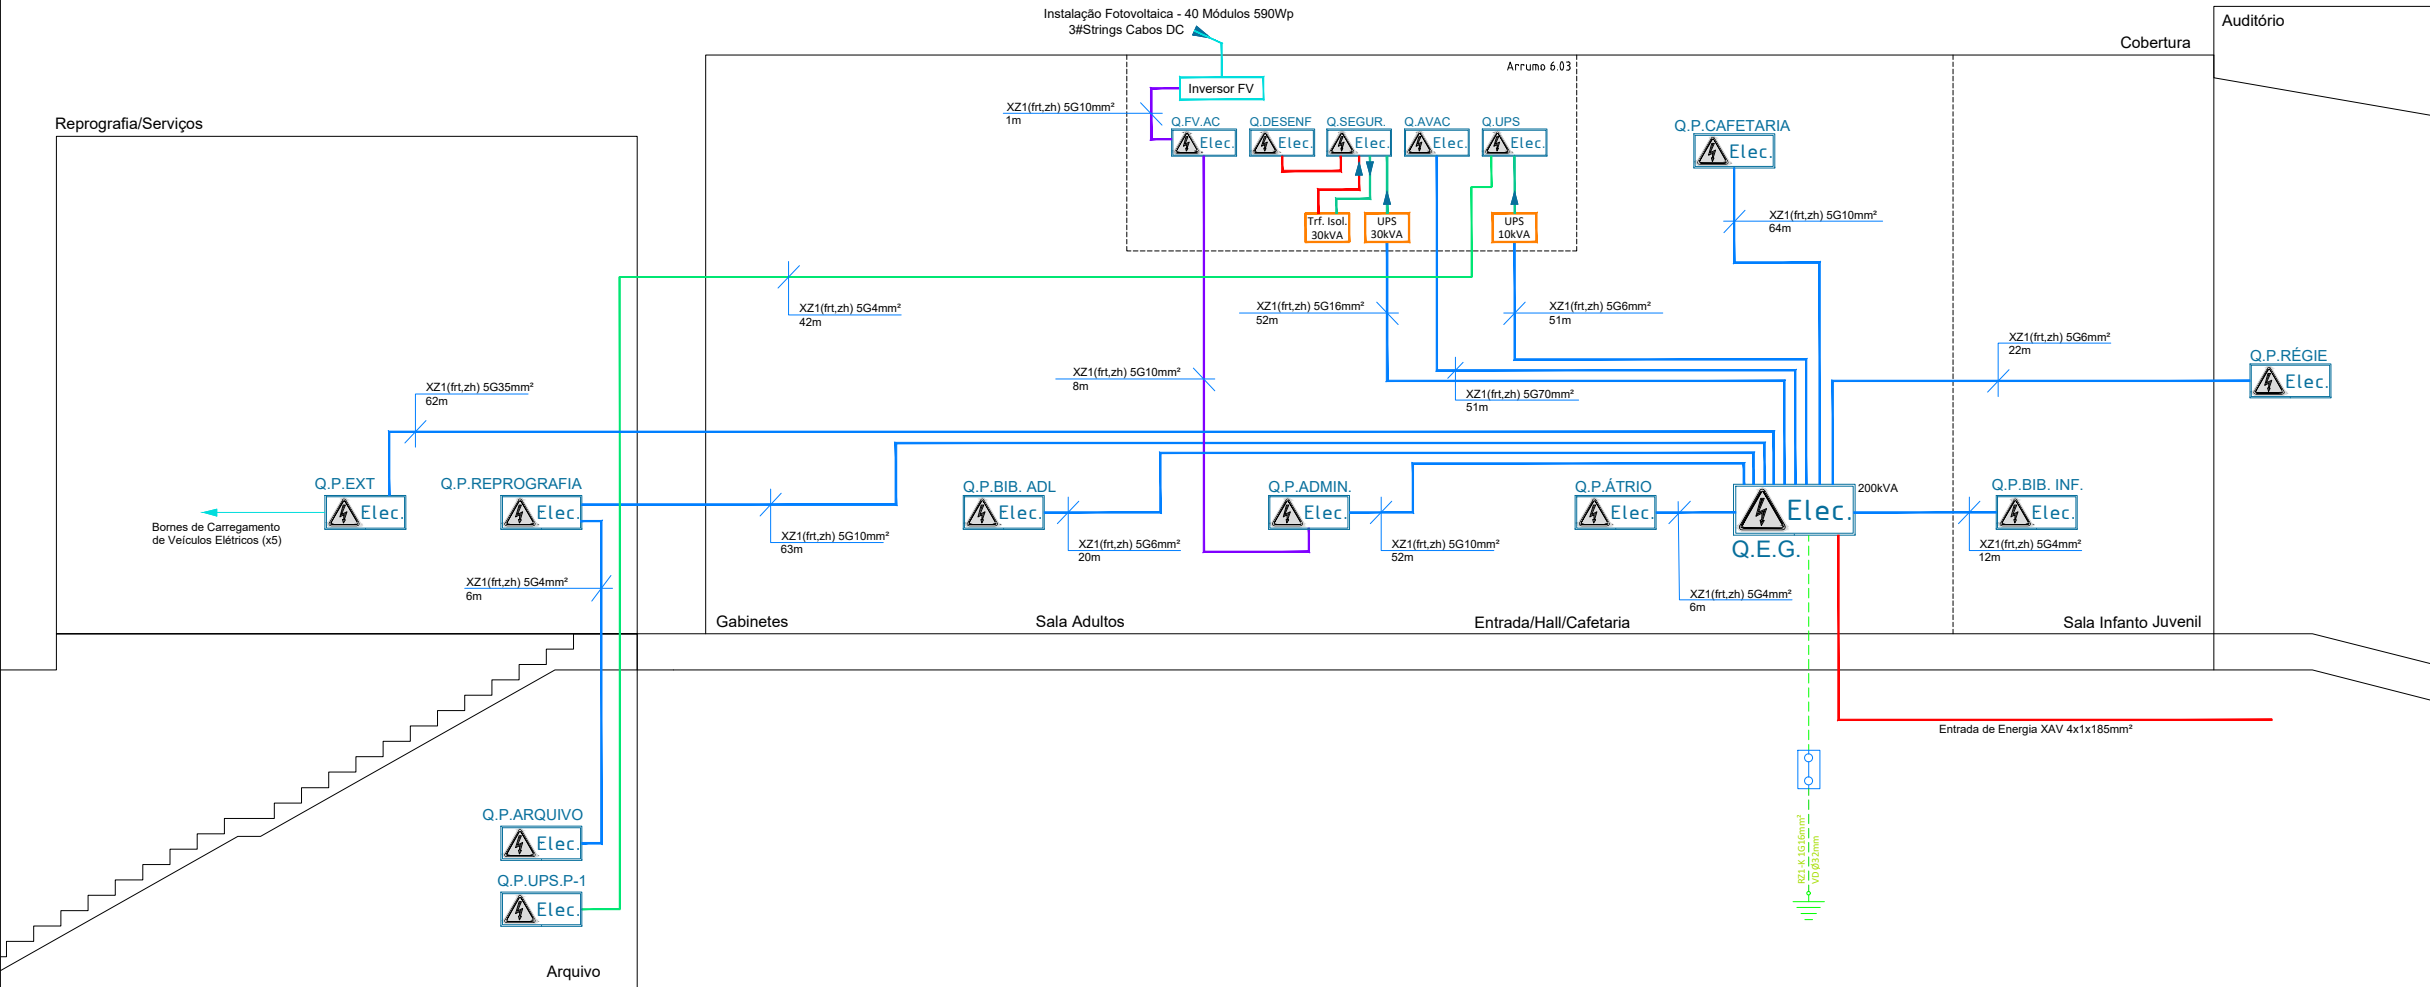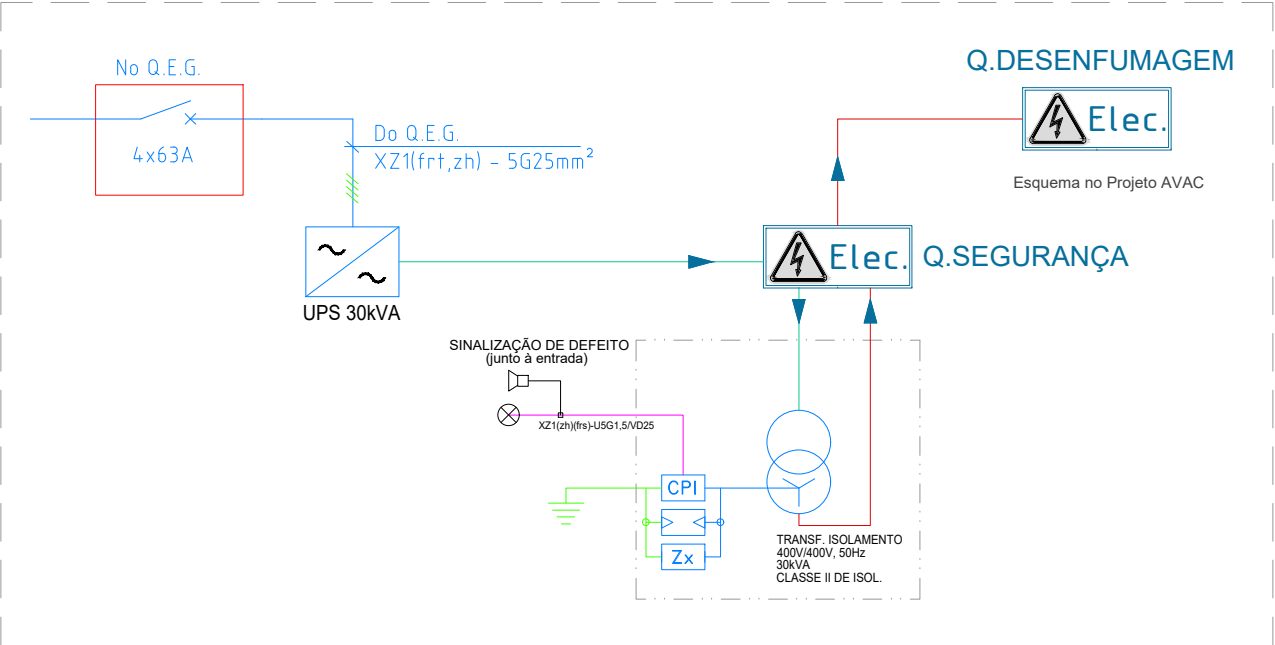

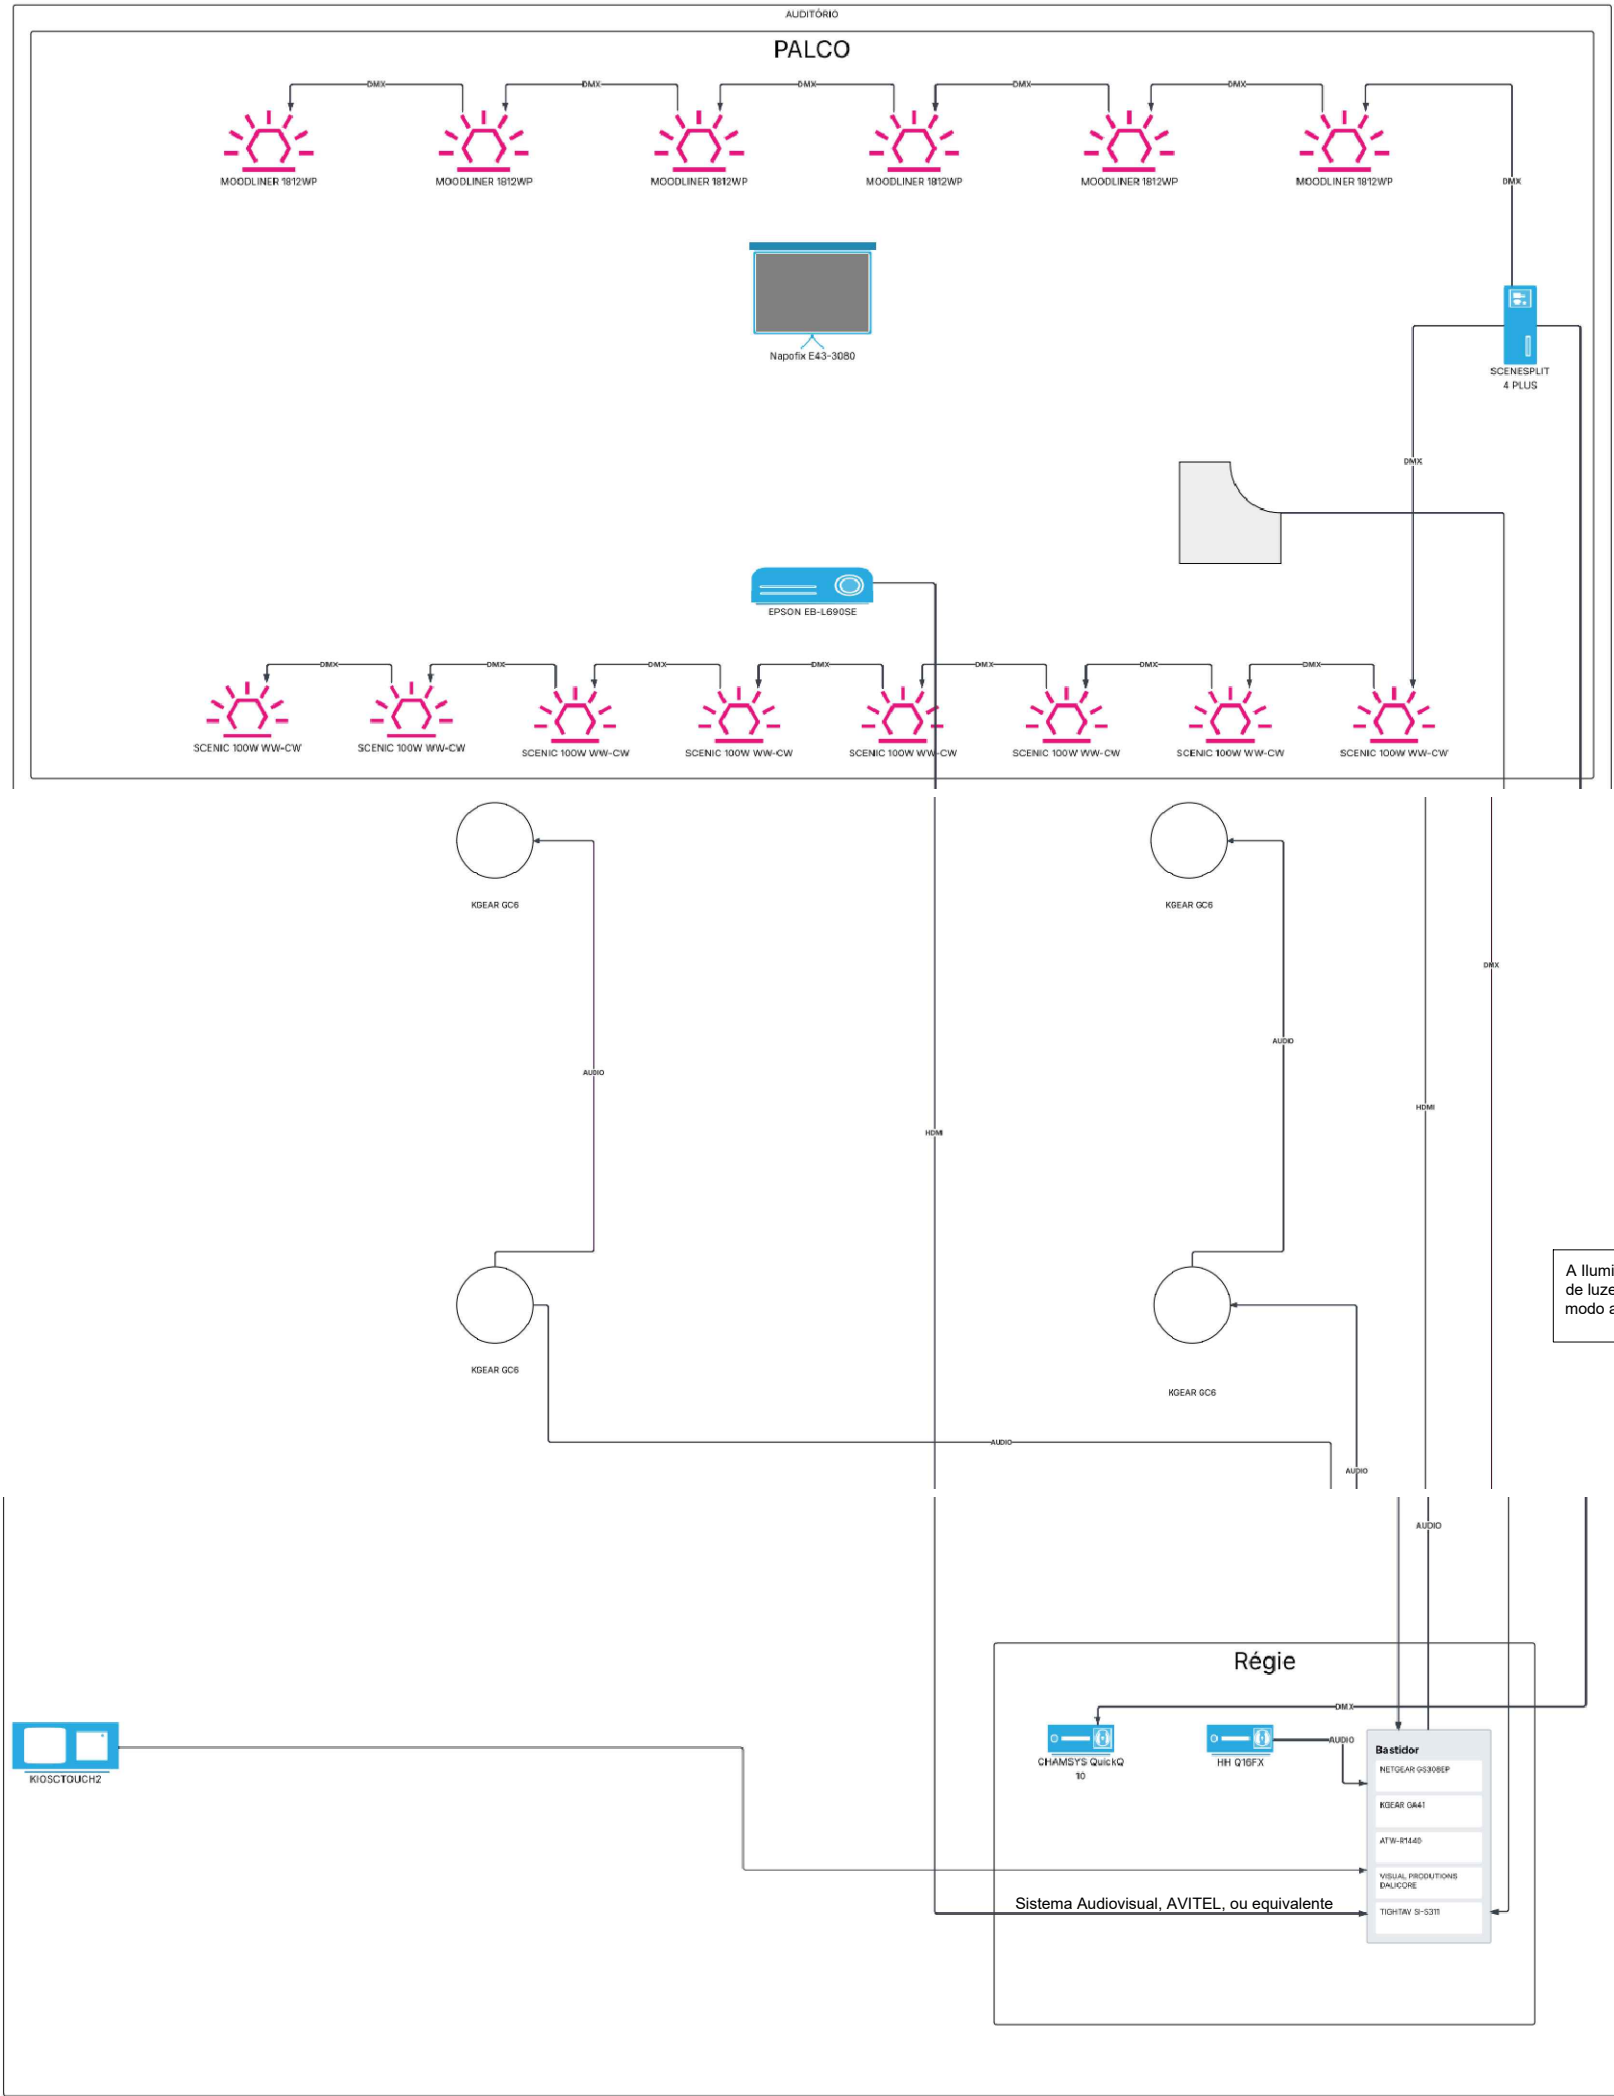

01	Modificações diversas	21.01.2026
00	Entrega do Projeto de Execução	19.12.2025
Revisão	Descrição	Data

TUU

Requerente
CÂMARA MUNICIPAL DE CANTANHEDE
Projeto
REQUALIFICAÇÃO E MODERNIZAÇÃO DA BIBLIOTECA MUNICIPAL DE CANTANHEDE

RUA EXEMPLO 11
000 000 4 CANTANHEDE

Especialidade
PROJETO DA INSTALAÇÃO ELÉTRICA

PROJETO DE EXECUÇÃO

Designação
ESQUEMA DE PRINCÍPIO DO SISTEMA AUDIOVISUAL DO AUDITÓRIO

JANEIRO 2026
S/E

EL023

Observações
ESTE PROJETO DEVERÁ SER LIDO EM CONJUNTO COM AS PEÇAS ESCRITAS, ASSIM COMO, O PROJETO DE ARQUITETURA E AS RESTANTES ESPECIALIDADES. QUAISQUER DISCREPÂNCIAS DEVERÃO SER COMUNICADAS AO PROJETISTA. TODAS AS MEDIDAS DESTES DESENHO SÃO DE PROJETO E MERAMENTE INDICATIVAS, NECESSITAM SER RETIFICADAS EM OBRA.











Nome Ficheiro
BIBLICA_PE_ELE_PD_V0.DWG

Código
39962025

Equipa
LUIS BALSAS | ENG ELETROTÉCNICO
LUIS BALSAS | ENG ELETROTÉCNICO

Reprodução proibida, Dec. Lei 45/85 de 17 de Setembro e código do direito de autor e direitos conexos.

TUU.BUILDING DESIGN MANAGEMENT
arquitetura@tuu.pt www.tuu.pt

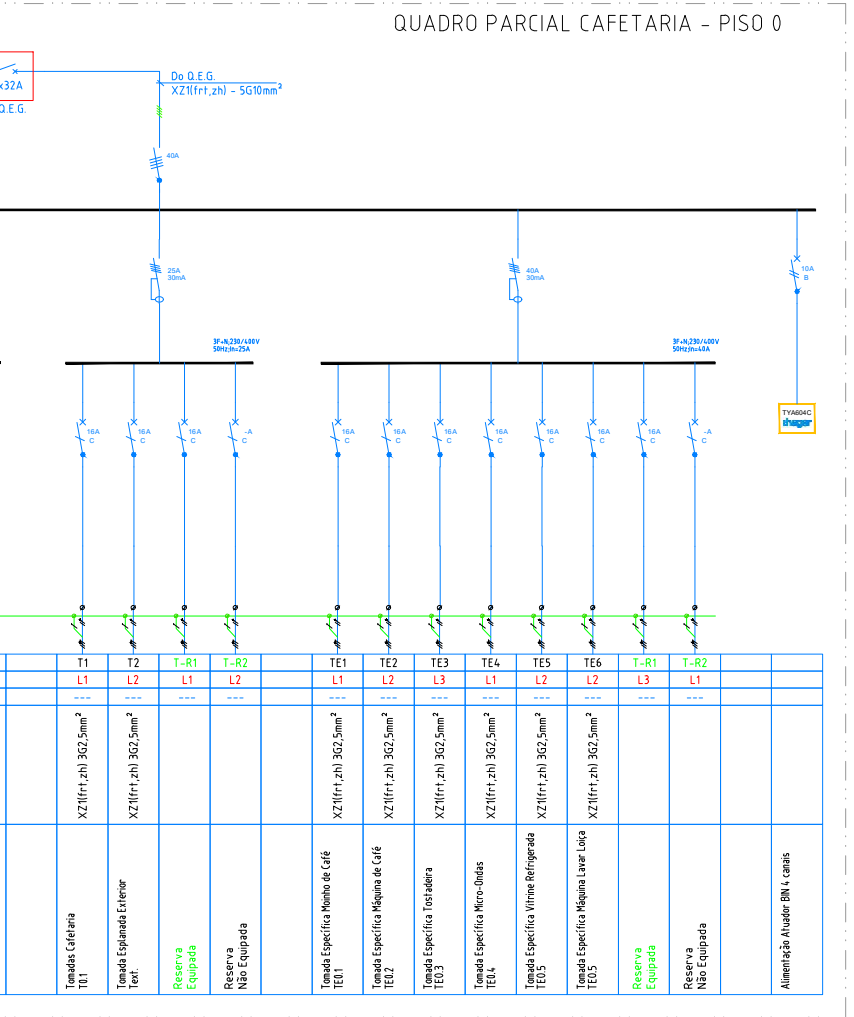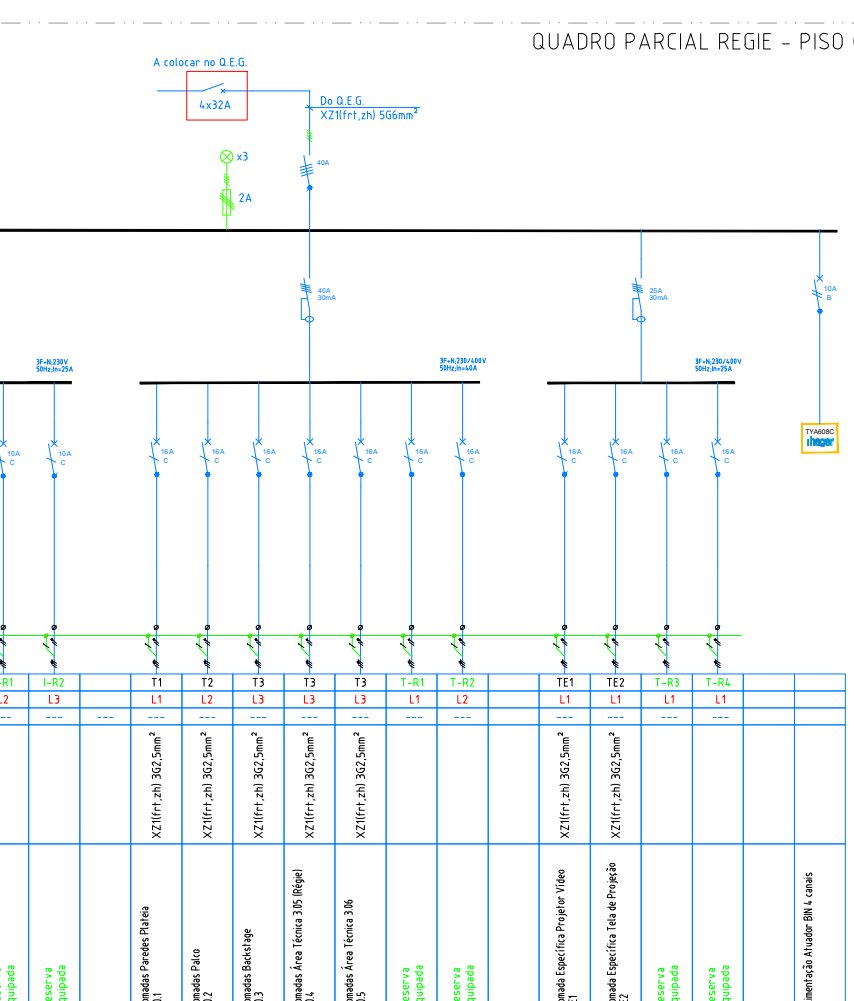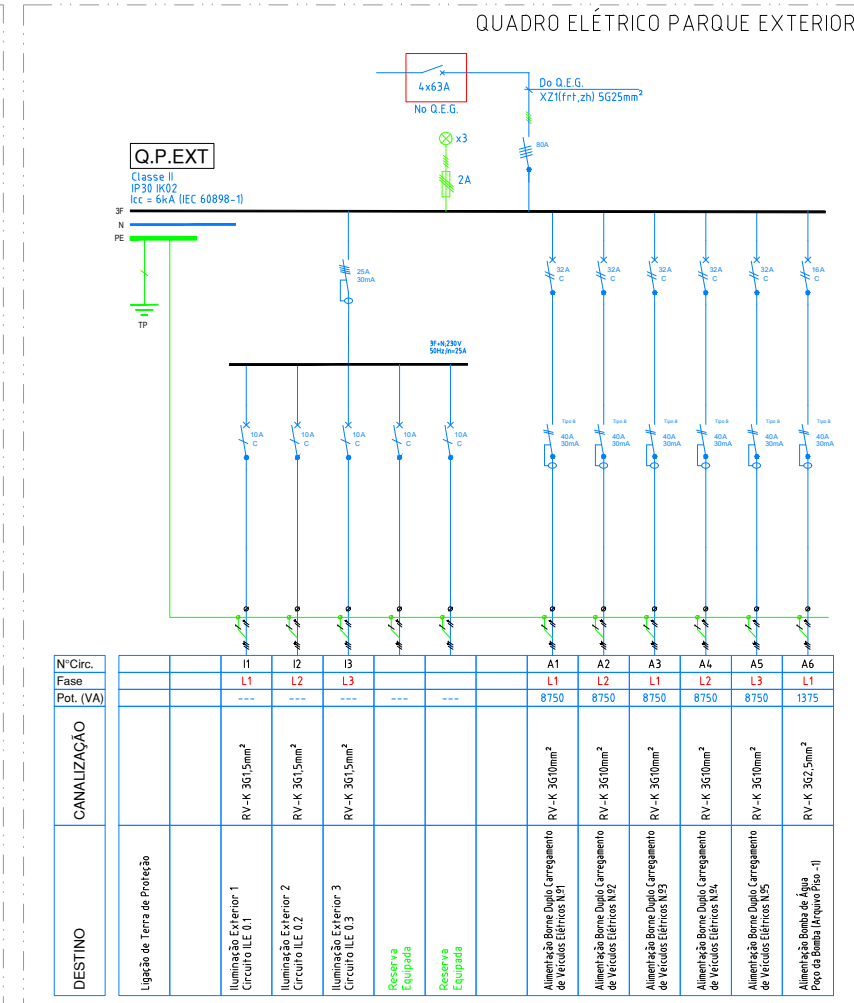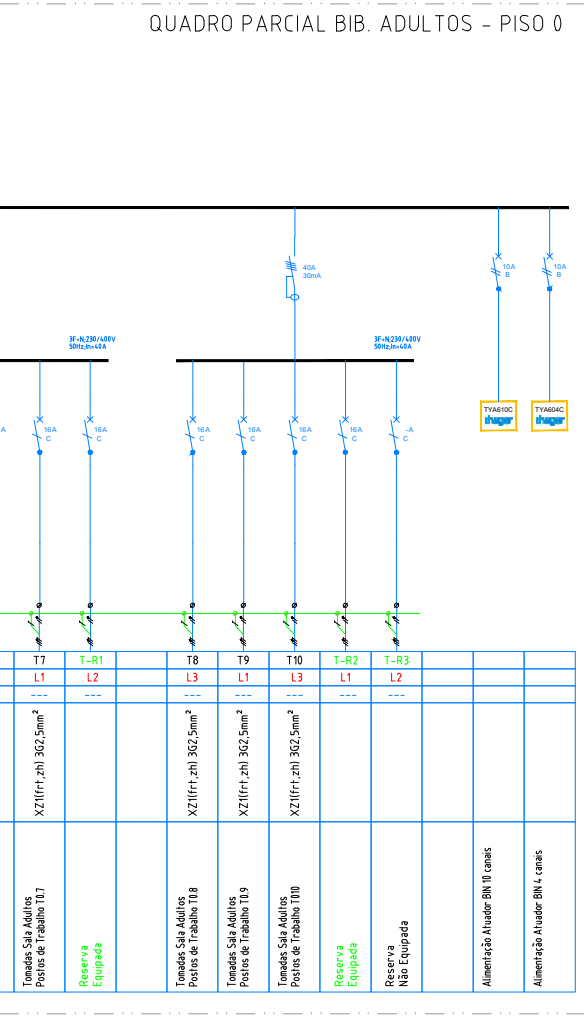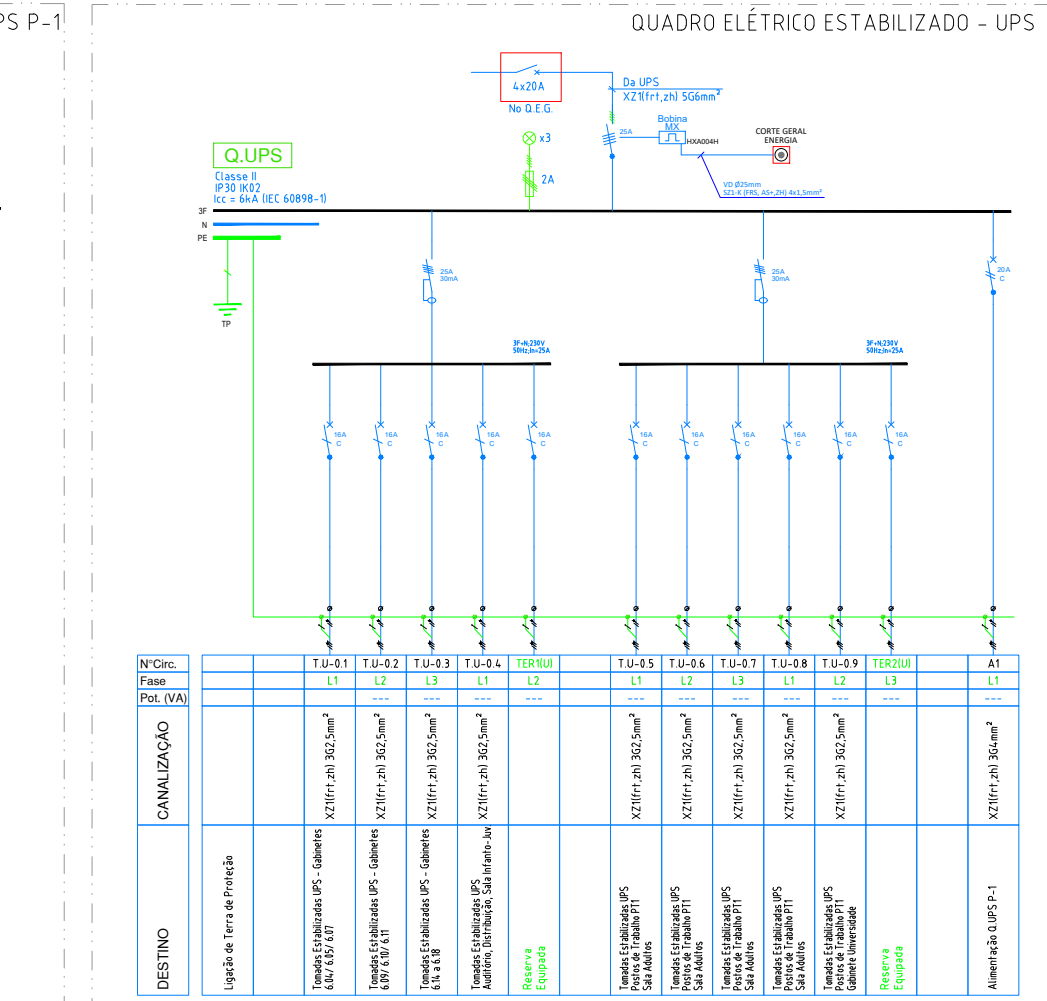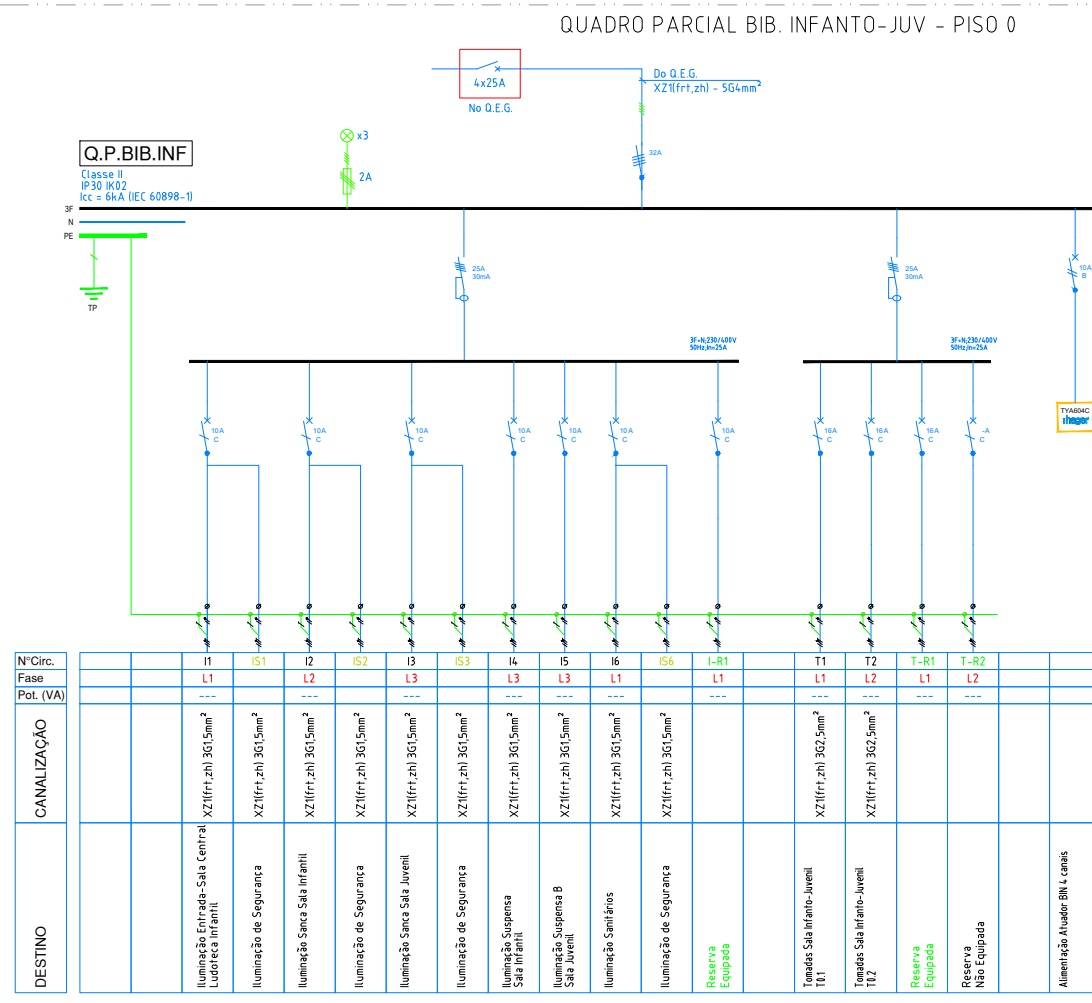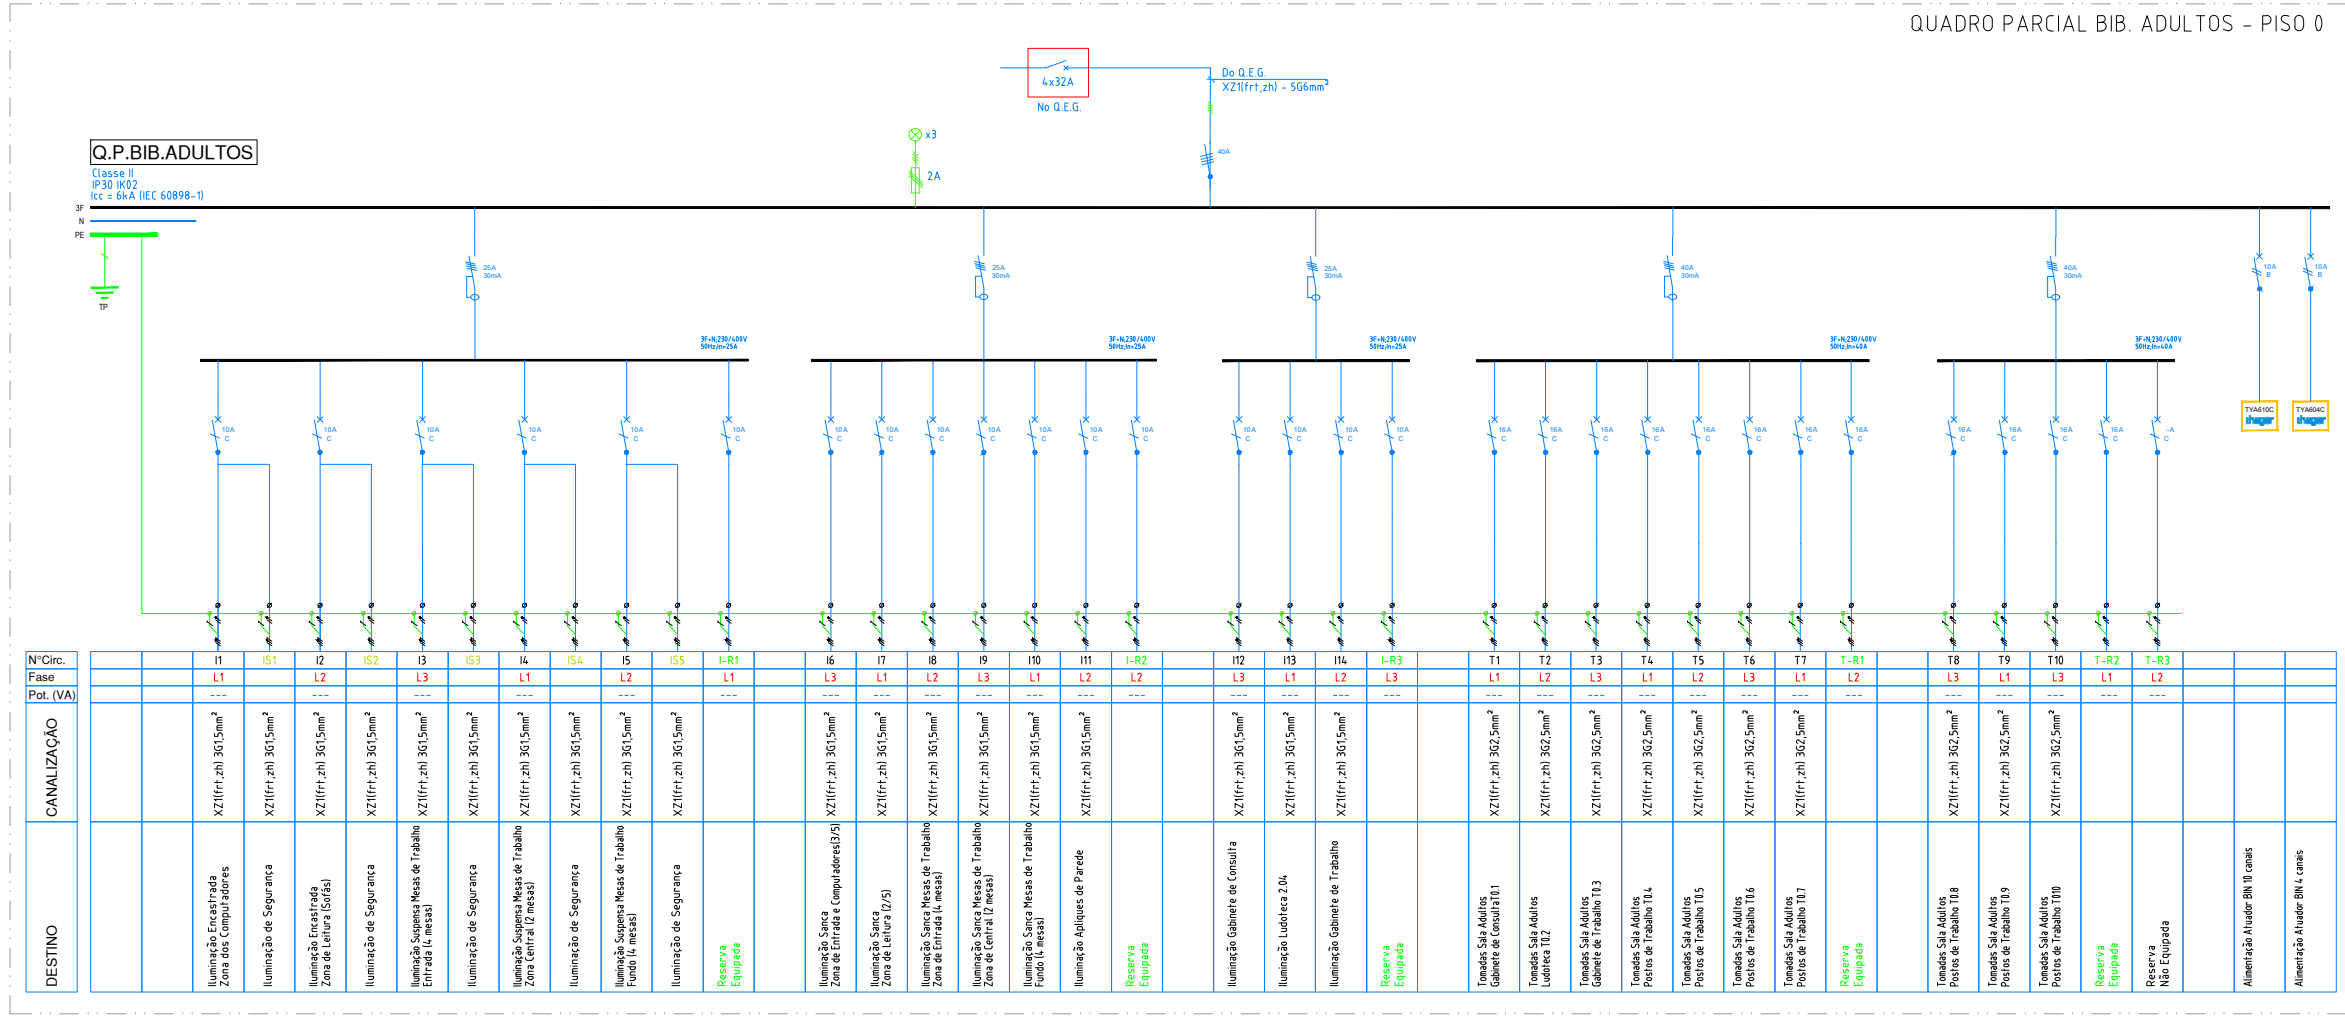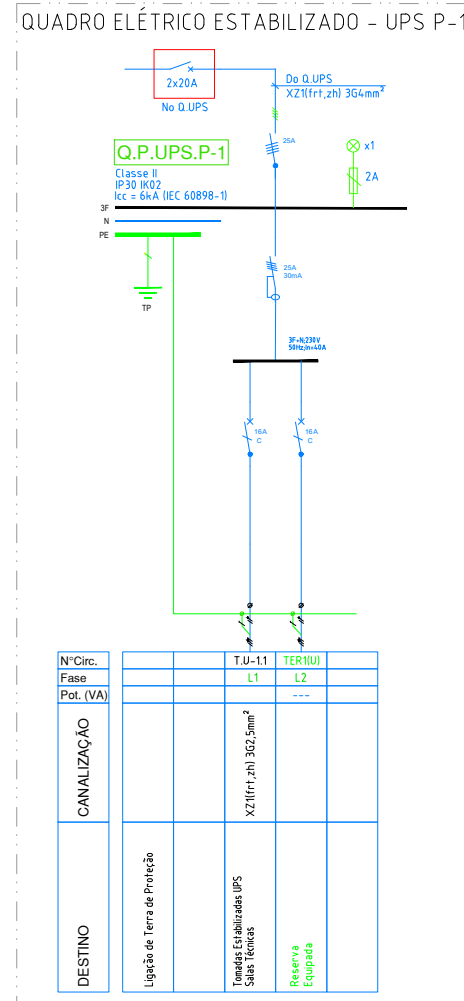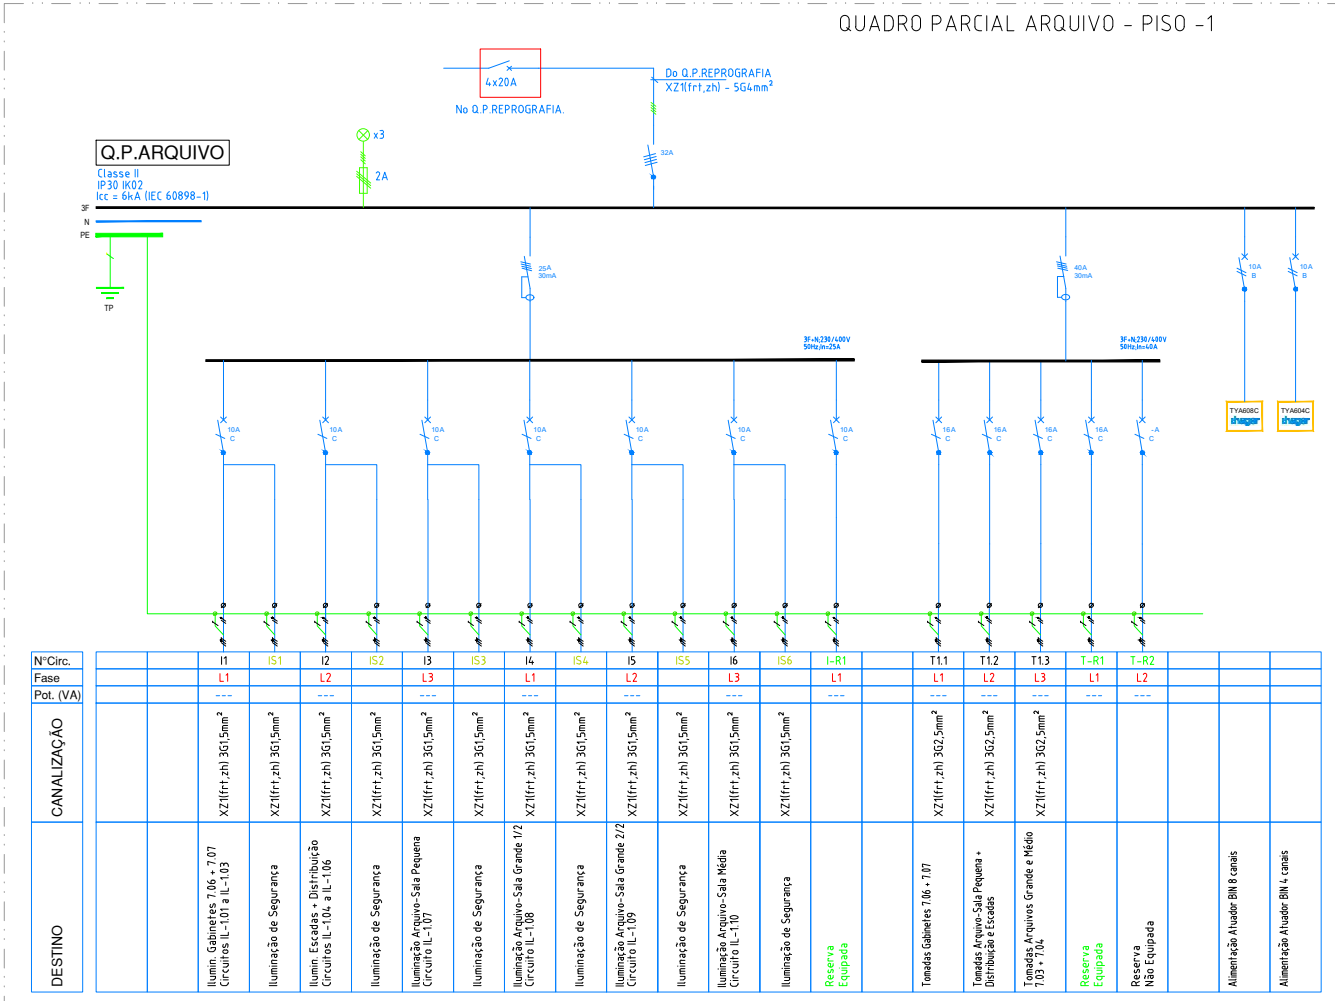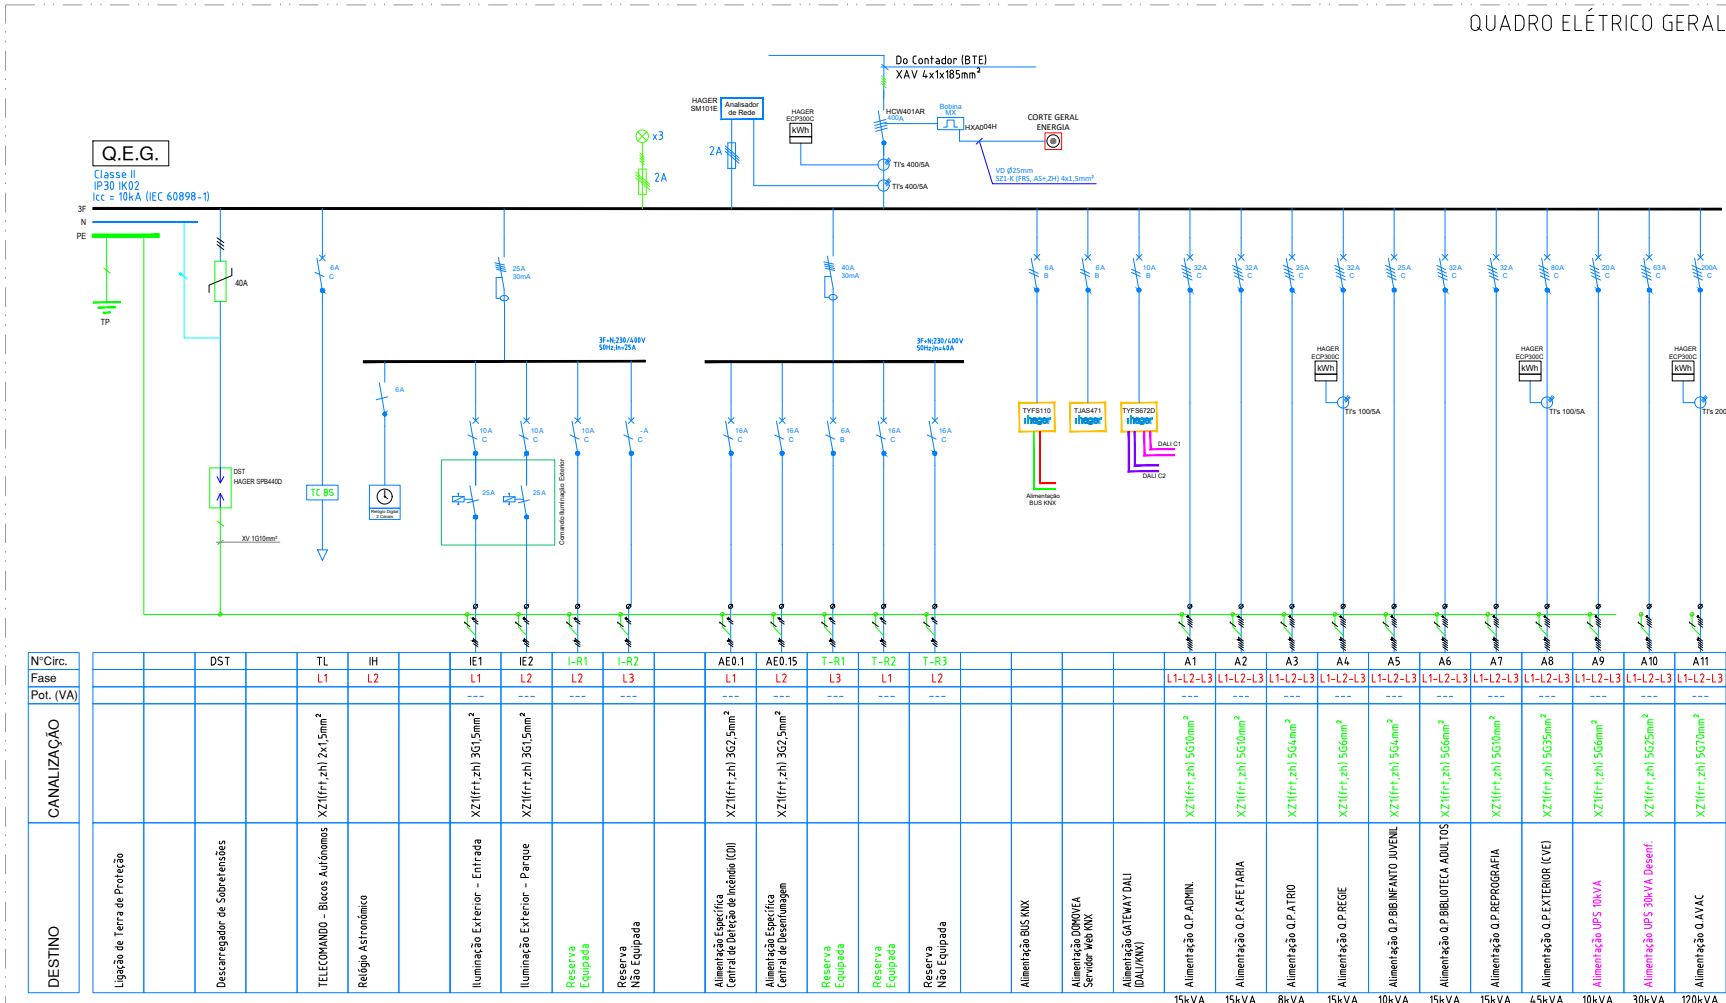

01	Modificações diversas	21.01.2020
02	Entrada do Projeto de Execução	19.12.2025
Revisão	Descrição	Data

TUU

Requerente
CÂMARA MUNICIPAL DE CANTANHEDE
Projeto
REQUALIFICAÇÃO E MODERNIZAÇÃO DA BIBLIOTECA MUNICIPAL DE CANTANHEDE

RU EXE UP 011
CANTANHEDE

Especialidade
PROJETO DA INSTALAÇÃO ELÉTRICA

Projeto de Execução
ESQUEMA UNIFILARES DOS QUADROS ELÉTRICOS

JANEIRO 2026
1:100

EL024

Observações
ESTE PROJETO DEVERÁ SER LIDO EM CONJUNTO COM AS PEÇAS ESCRITAS, ASSIM COMO, O PROJETO DE ARQUITETURA E AS RESTANTES ESPECIALIDADES.
QUAISQUER DISCREPÂNCIAS DEVERÃO SER COMUNICADAS AO PROJETISTA, TODAS AS MEDIDAS DESTE DESENHO SÃO DE PROJETO E MERAMENTE INDICATIVAS, NECESSITAM SER RETIFICADAS EM OBRA.

Nome Ficheiro
BIBLICA_PE_ELE_PD_V0.DWG

Código
39962025

Equipa
AN A E M EL ENG ELETROTÉCNICO
LUIS BALSAS | ENG ELETROTÉCNICO

Reprodução proibida, Dec. Lei 49185 de 17 de Setembro e código do direito de autor e direitos conexos.

TUU.BUILDING DESIGN MANAGEMENT
arquitetura@tuu.pt www.tuu.pt



Especialidade

PROJETO DA INSTALAÇÃO ELÉTRICA

ESQUEMA UNIFILARES DOS QUADROS ELÉTRICOS

EL025

Nome Ficheiro
BIBLICA_PE_ELE_PD_V0.DWG



Equipa

AN A EX EM PL O | ENG ELETROTÉCNICO
LUÍS BALSAS | ENG ELETROTÉCNICO


TUU.BUILDING DESIGN MANAGEMENT

arquitetura@tuu.pt www.tuu.pt


arquitetura@tuu.pt www.tuu.pt

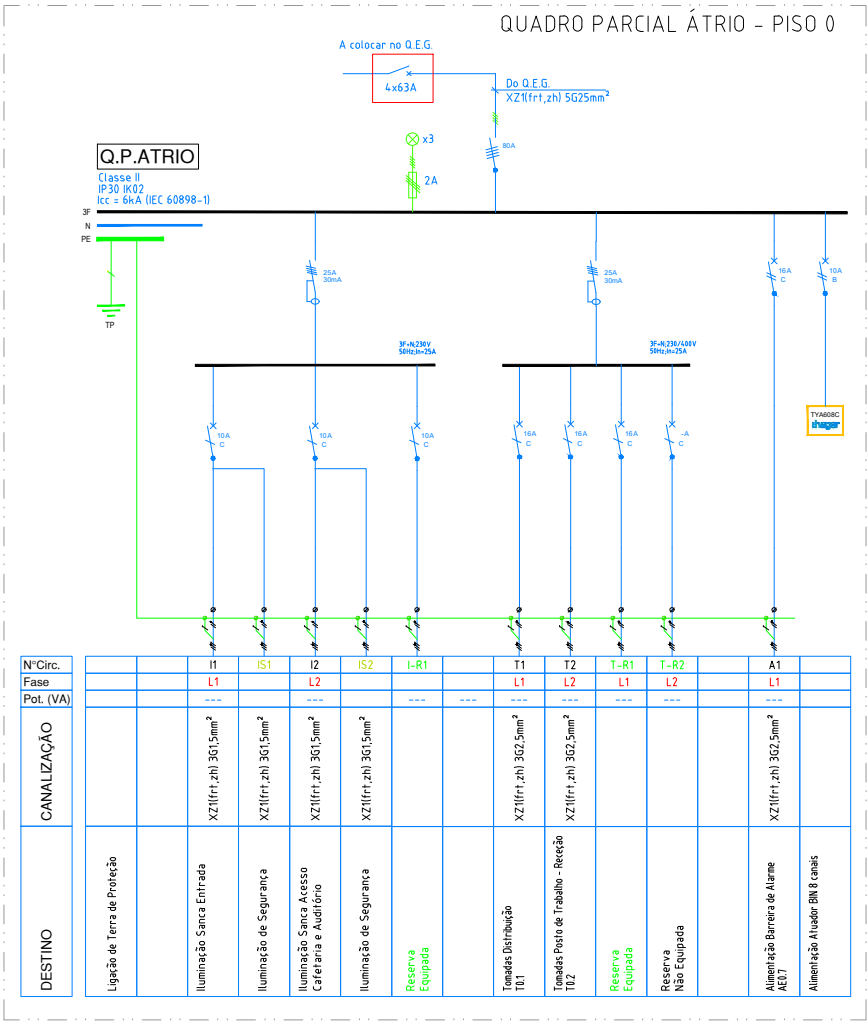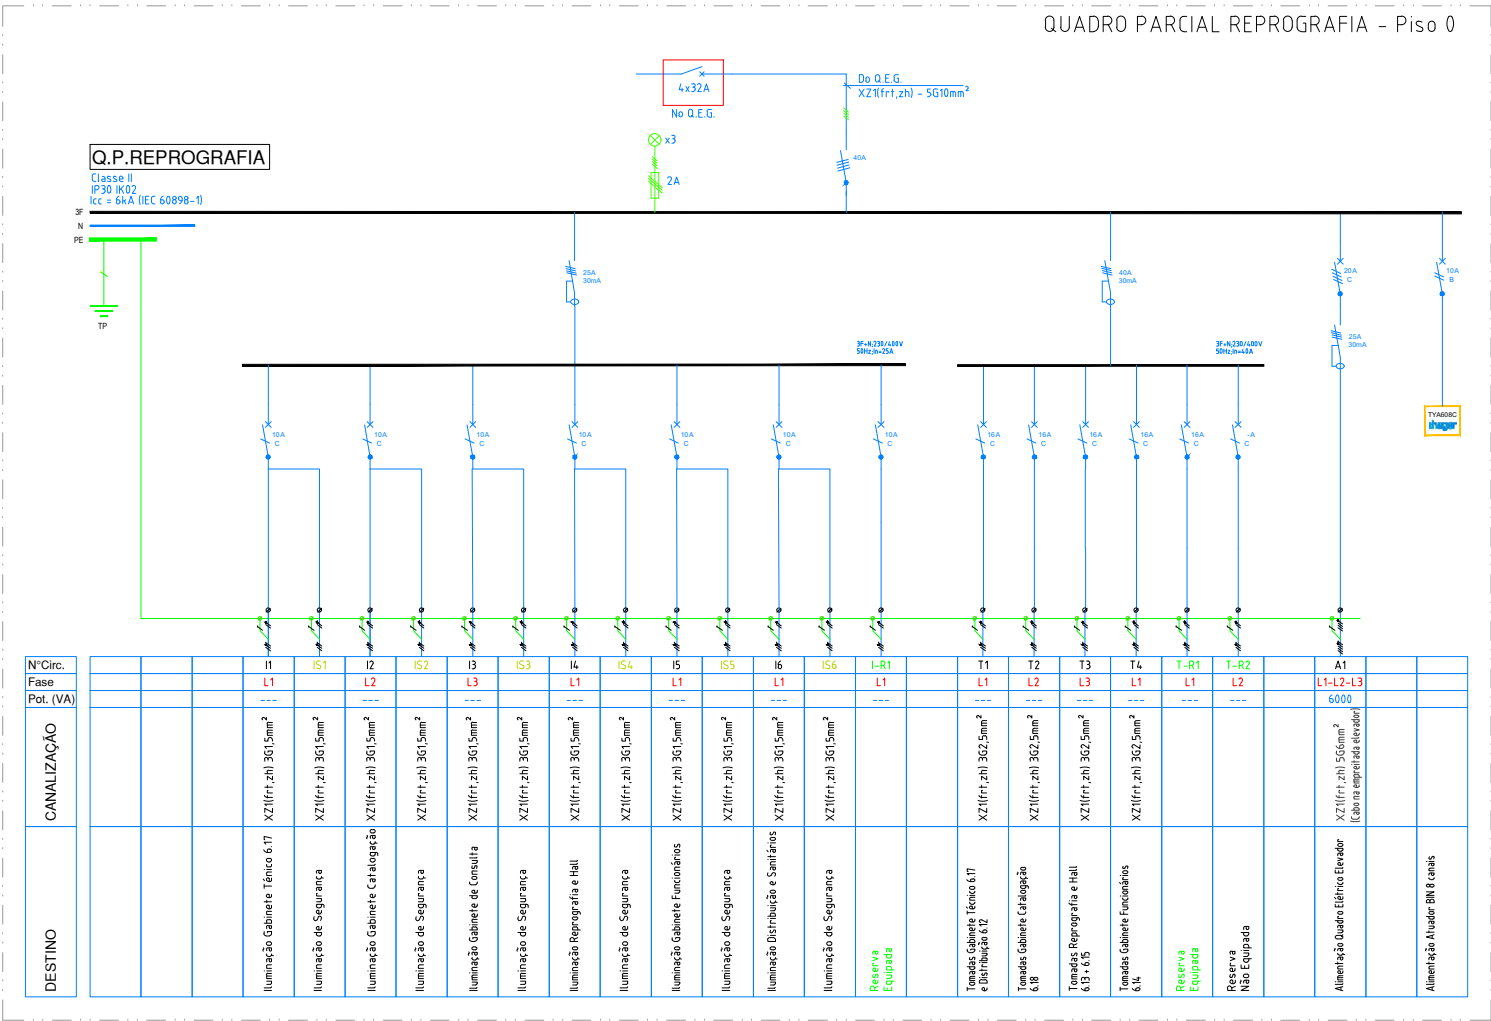

QUADRO PARCIAL REGIE - PISO 0

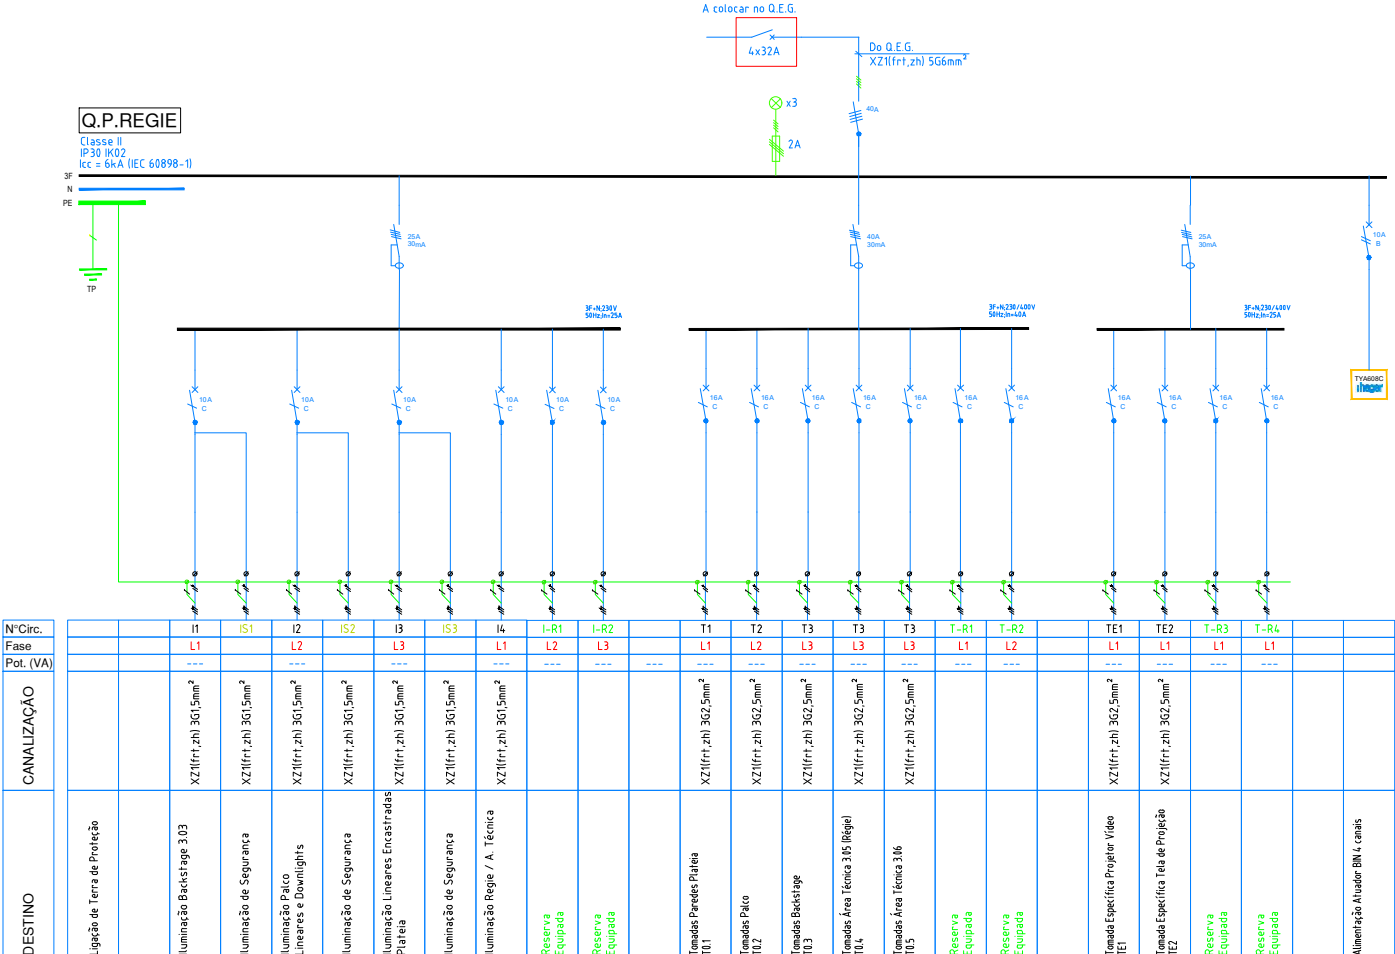

QUADRO DE SEGURANÇA - Piso 0

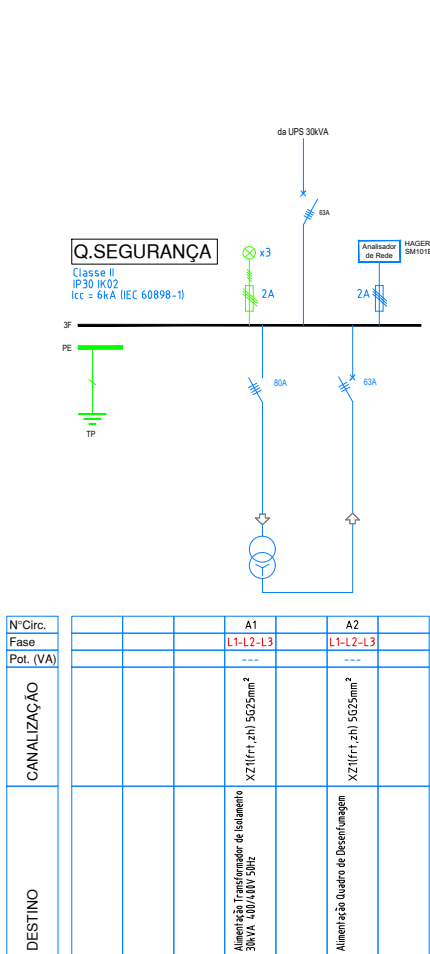

01	Modificações diversas	21.01.2026
00	Entrega do Projeto de Execução	19.12.2025
Revisão	Descrição	Data

TUW

Requerente

CÂMARA MUNICIPAL DE
CANTANHEDE

Projeto

REQUALIFICAÇÃO E MODERNIZAÇÃO DA
BIBLIOTECA MUNICIPAL DE CANTANHEDE

CANTANHEDE

Especialidade

PROJETO DA INSTALAÇÃO ELÉTRICA

PROJETO DE EXECUÇÃO

Designação

ESQUEMA UNIFILARES DOS QUADROS ELÉTRICOS

JANEIRO 2026

6/E

EL026

Observações

ESTE PROJETO DEVERÁ SER LIDO EM CONJUNTO COM AS PEÇAS ESCRITAS, ASSIM COMO, O PROJETO DE ARQUITETURA E AS RESTANTES ESPECIALIDADES.

QUAISQUER DISCREPÂNCIAS DEVERÃO SER COMUNICADAS AO

PROJETISTA. TODAS AS MEDIDAS DESTES DESENHO SÃO DE

PROJETO E MERAMENTE INDICATIVAS, NECESSITAM SER

RETIFICADAS EM OBRA.

Nome Ficheiro

BIBLICA PE ELE PD V0.DWG

Código

39962025

Equipa

ANEXO | ENG ELETROTÉCNICO
LUÍS BALSAS | ENG ELETROTÉCNICO


Reprodução proibida, Dec. Lei 45\85 de 17 de Setembro e código do direito de autor e direitos conexos.

TUU.BUILDING DESIGN MANAGEMENT

arquitetura@tuu.pt

www.tuu.pt

DIAGRAMA DE PRINCIPIO KNX

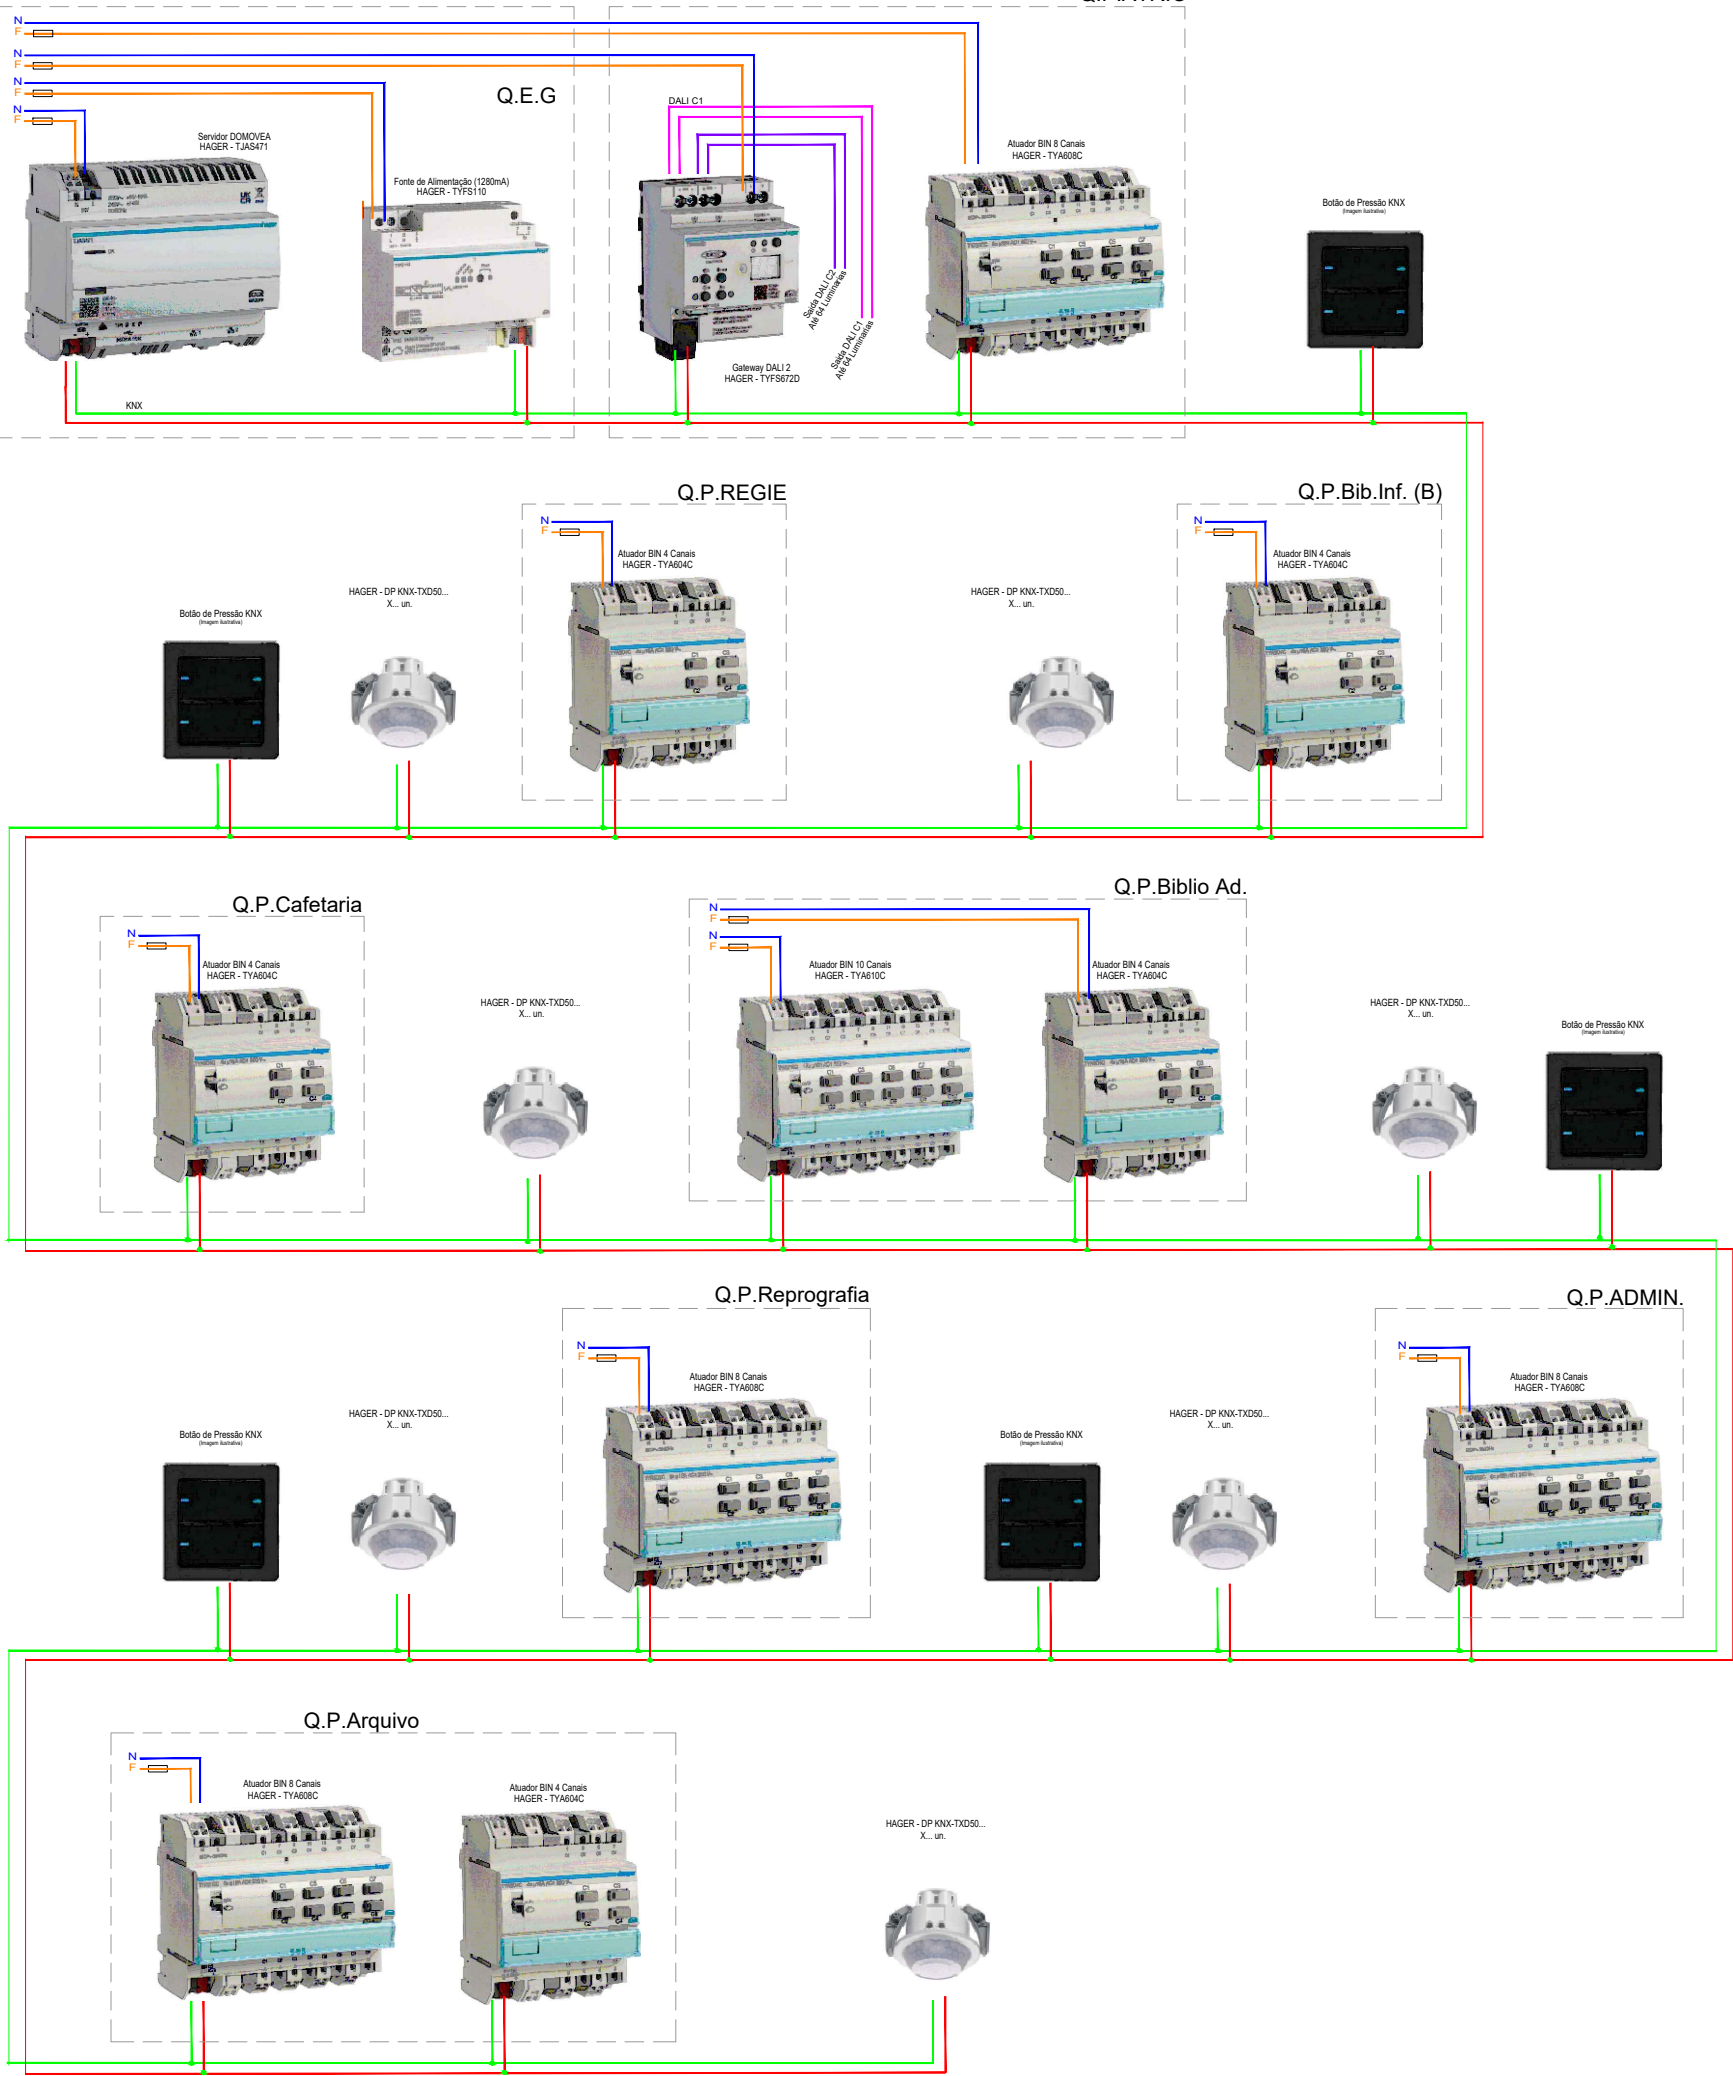

01	Modificações diversas	21.01.2026
00	Entrega do Projeto de Execução	19.12.2025
Revisão	Descrição	Data

TUU

Requerente
CÂMARA MUNICIPAL DE
CANTANHEDE
Projeto
REQUALIFICAÇÃO E MODERNIZAÇÃO DA
BIBLIOTECA MUNICIPAL DE CANTANHEDE

RU A EXE MP LO 11
000 0-00 4 CANTANHEDE

Especialidade
PROJETO DA INSTALAÇÃO ELÉTRICA

PROJETO DE EXECUÇÃO

Designação
DIAGRAMA DA INSTALAÇÃO
KNX Controlo da Iluminação

JANEIRO 2026
S/E

EL027

Observações
ESTE PROJETO DEVERÁ SER LIDO EM CONJUNTO COM AS PEÇAS
ESCRITAS, ASSIM COMO, O PROJETO DE ARQUITETURA E AS
REstantes ESPECIALIDADES.
QUAISQUER DISCREPÂNCIAS DEVERÃO SER COMUNICADAS AO
PROJETISTA. TODAS AS MEDIDAS DESTES DESENHO SÃO DE
PROJETO E MERAMENTE INDICATIVAS, NECESSITAM SER
RETIFICADAS EM OBRA.

Nome Ficheiro
BIBLICA_PE_ELE_PD_V0.DWG

Código
39962025

Equipa
AN A EXE MP LO 11 | ENG ELETROTÉCNICO
LUIS BALSAS | ENG ELETROTÉCNICO

Reprodução proibida, Dec. Lei 45/85 de 17 de
Setembro e código do direito de autor e
direitos conexos.

TUU.BUILDING DESIGN MANAGEMENT
arquitetura@tuu.pt www.tuu.pt